

PROJECT TITLE- BAR DESIGN

DATE- 08/12/2022

DRAWN BY- YASH VARDHAN


ADMISSION NO.- 20210634


SHEET TITLE- FLOOR PLAN


SHEET NO.- 01


SUBJECT- INTERIOR ARCHITECTURE

SCALE-1:75

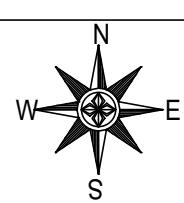

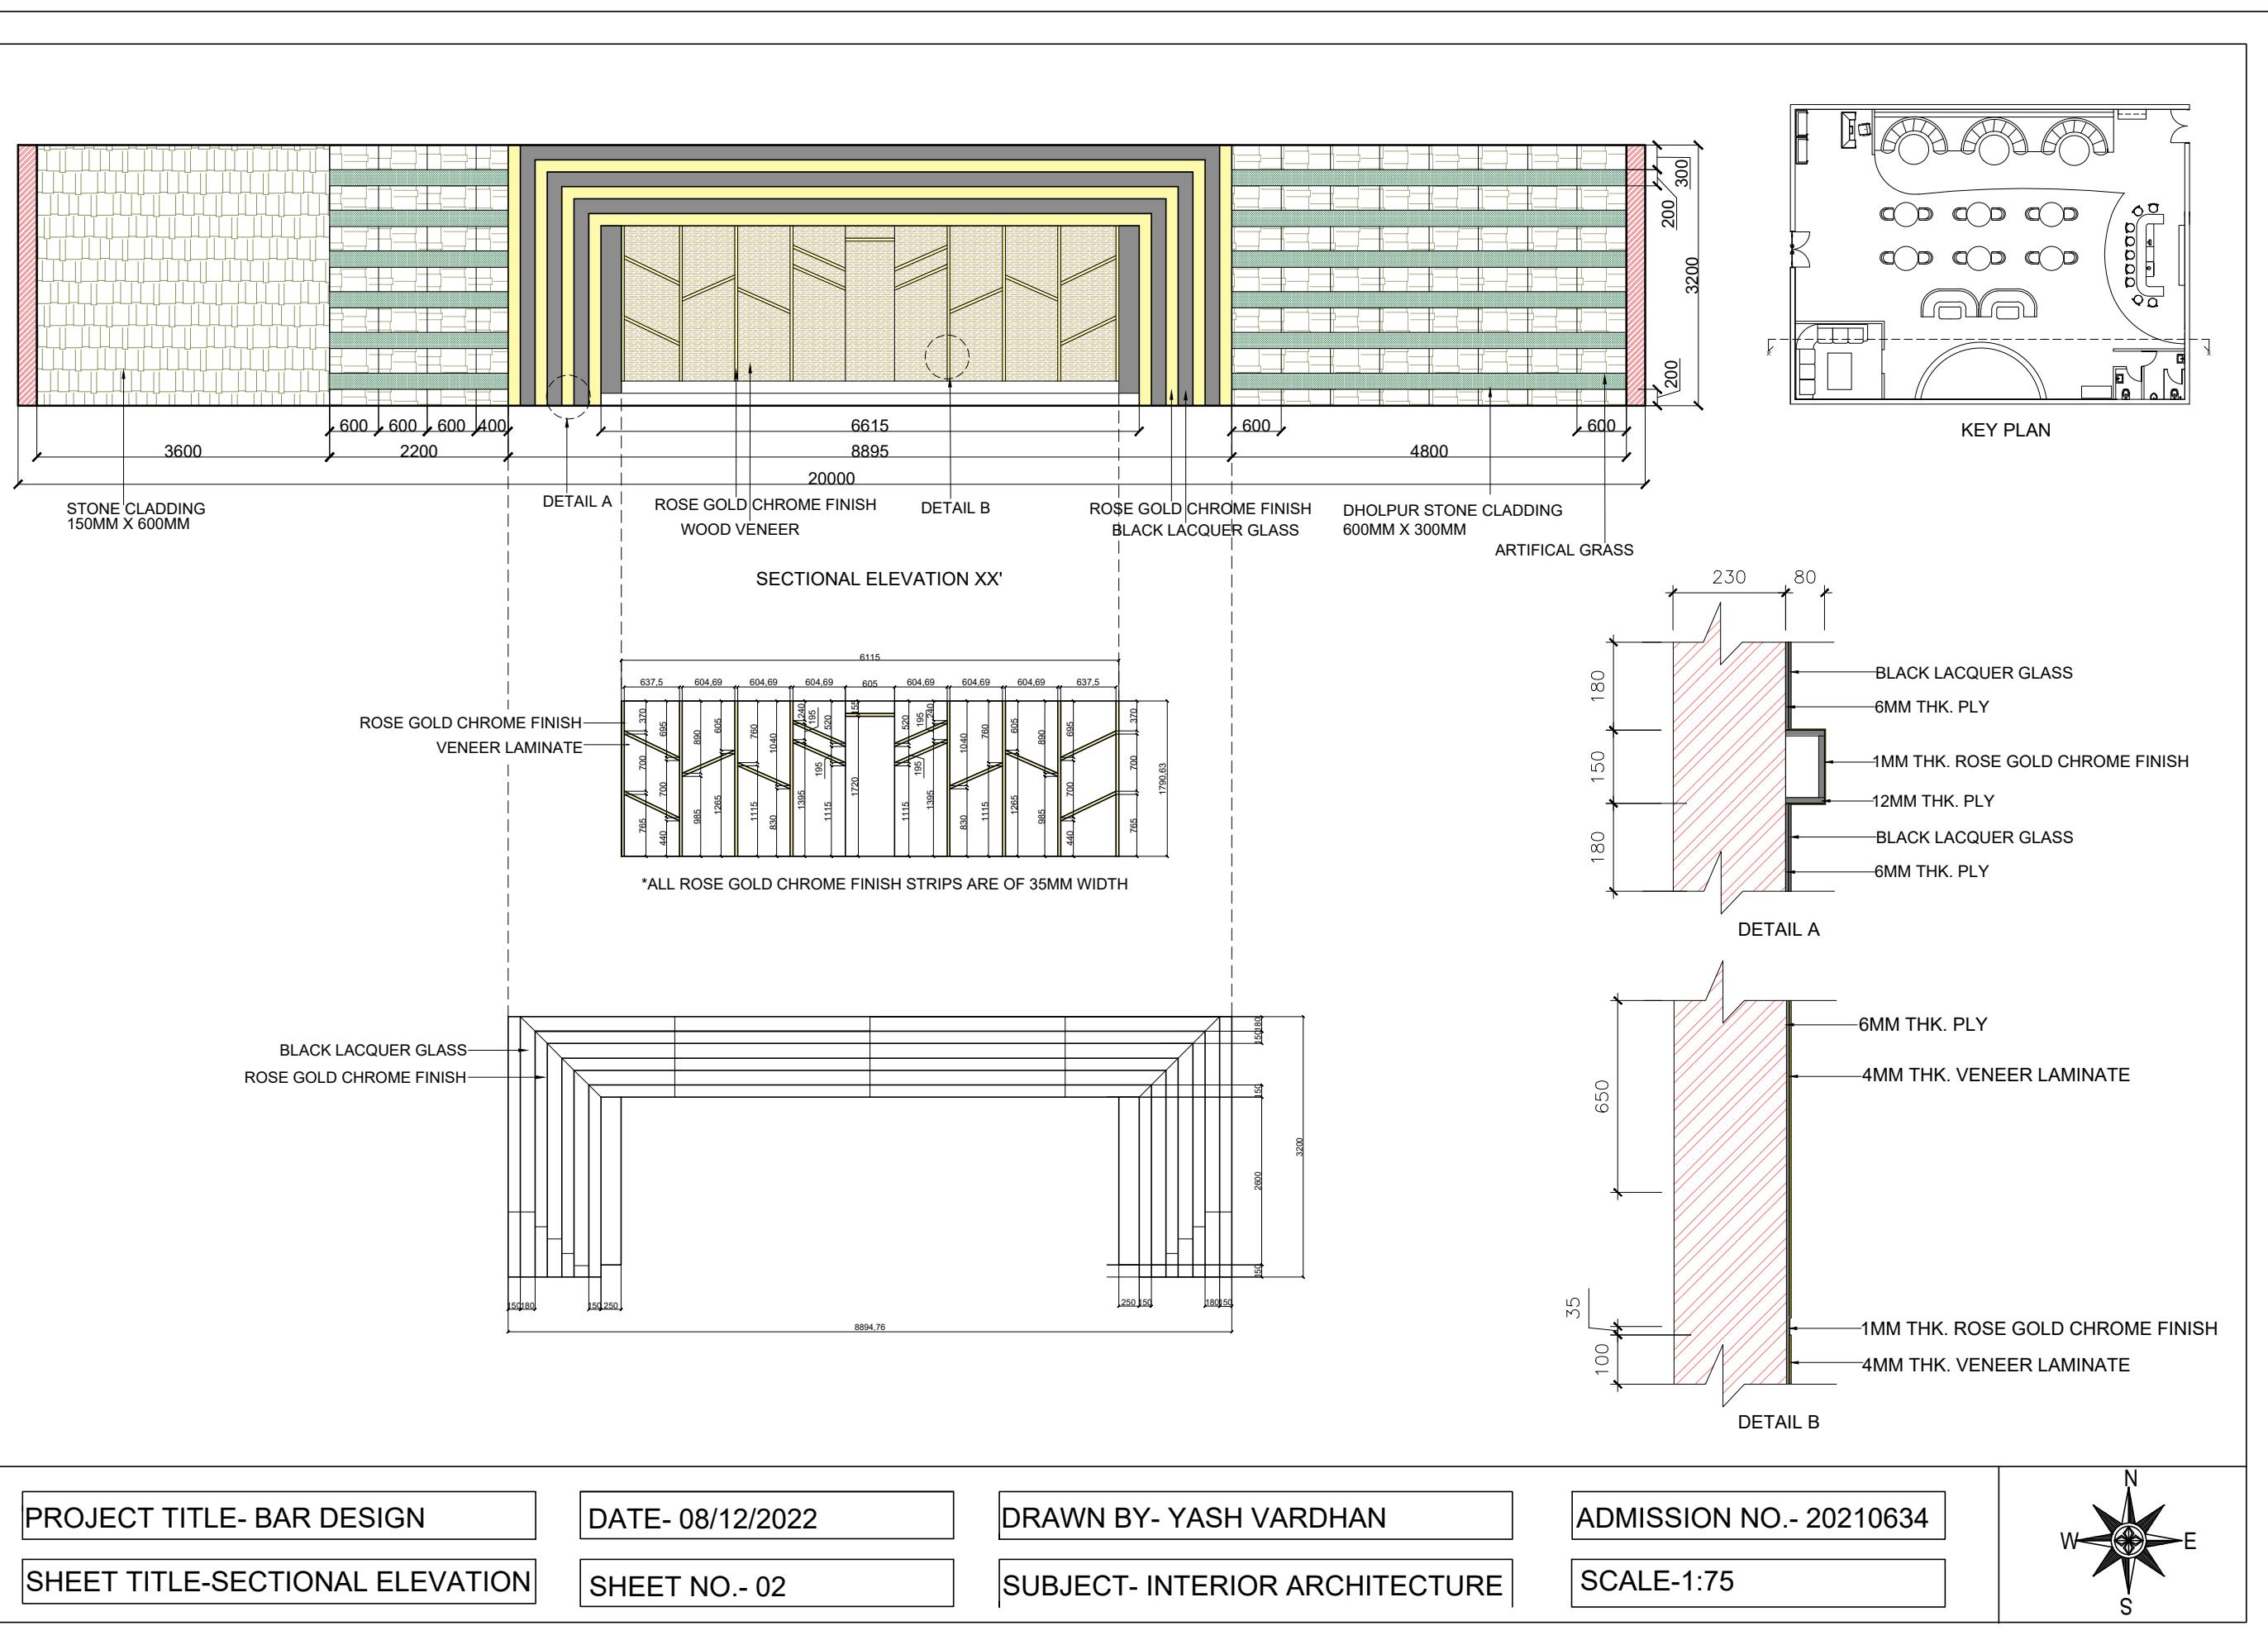


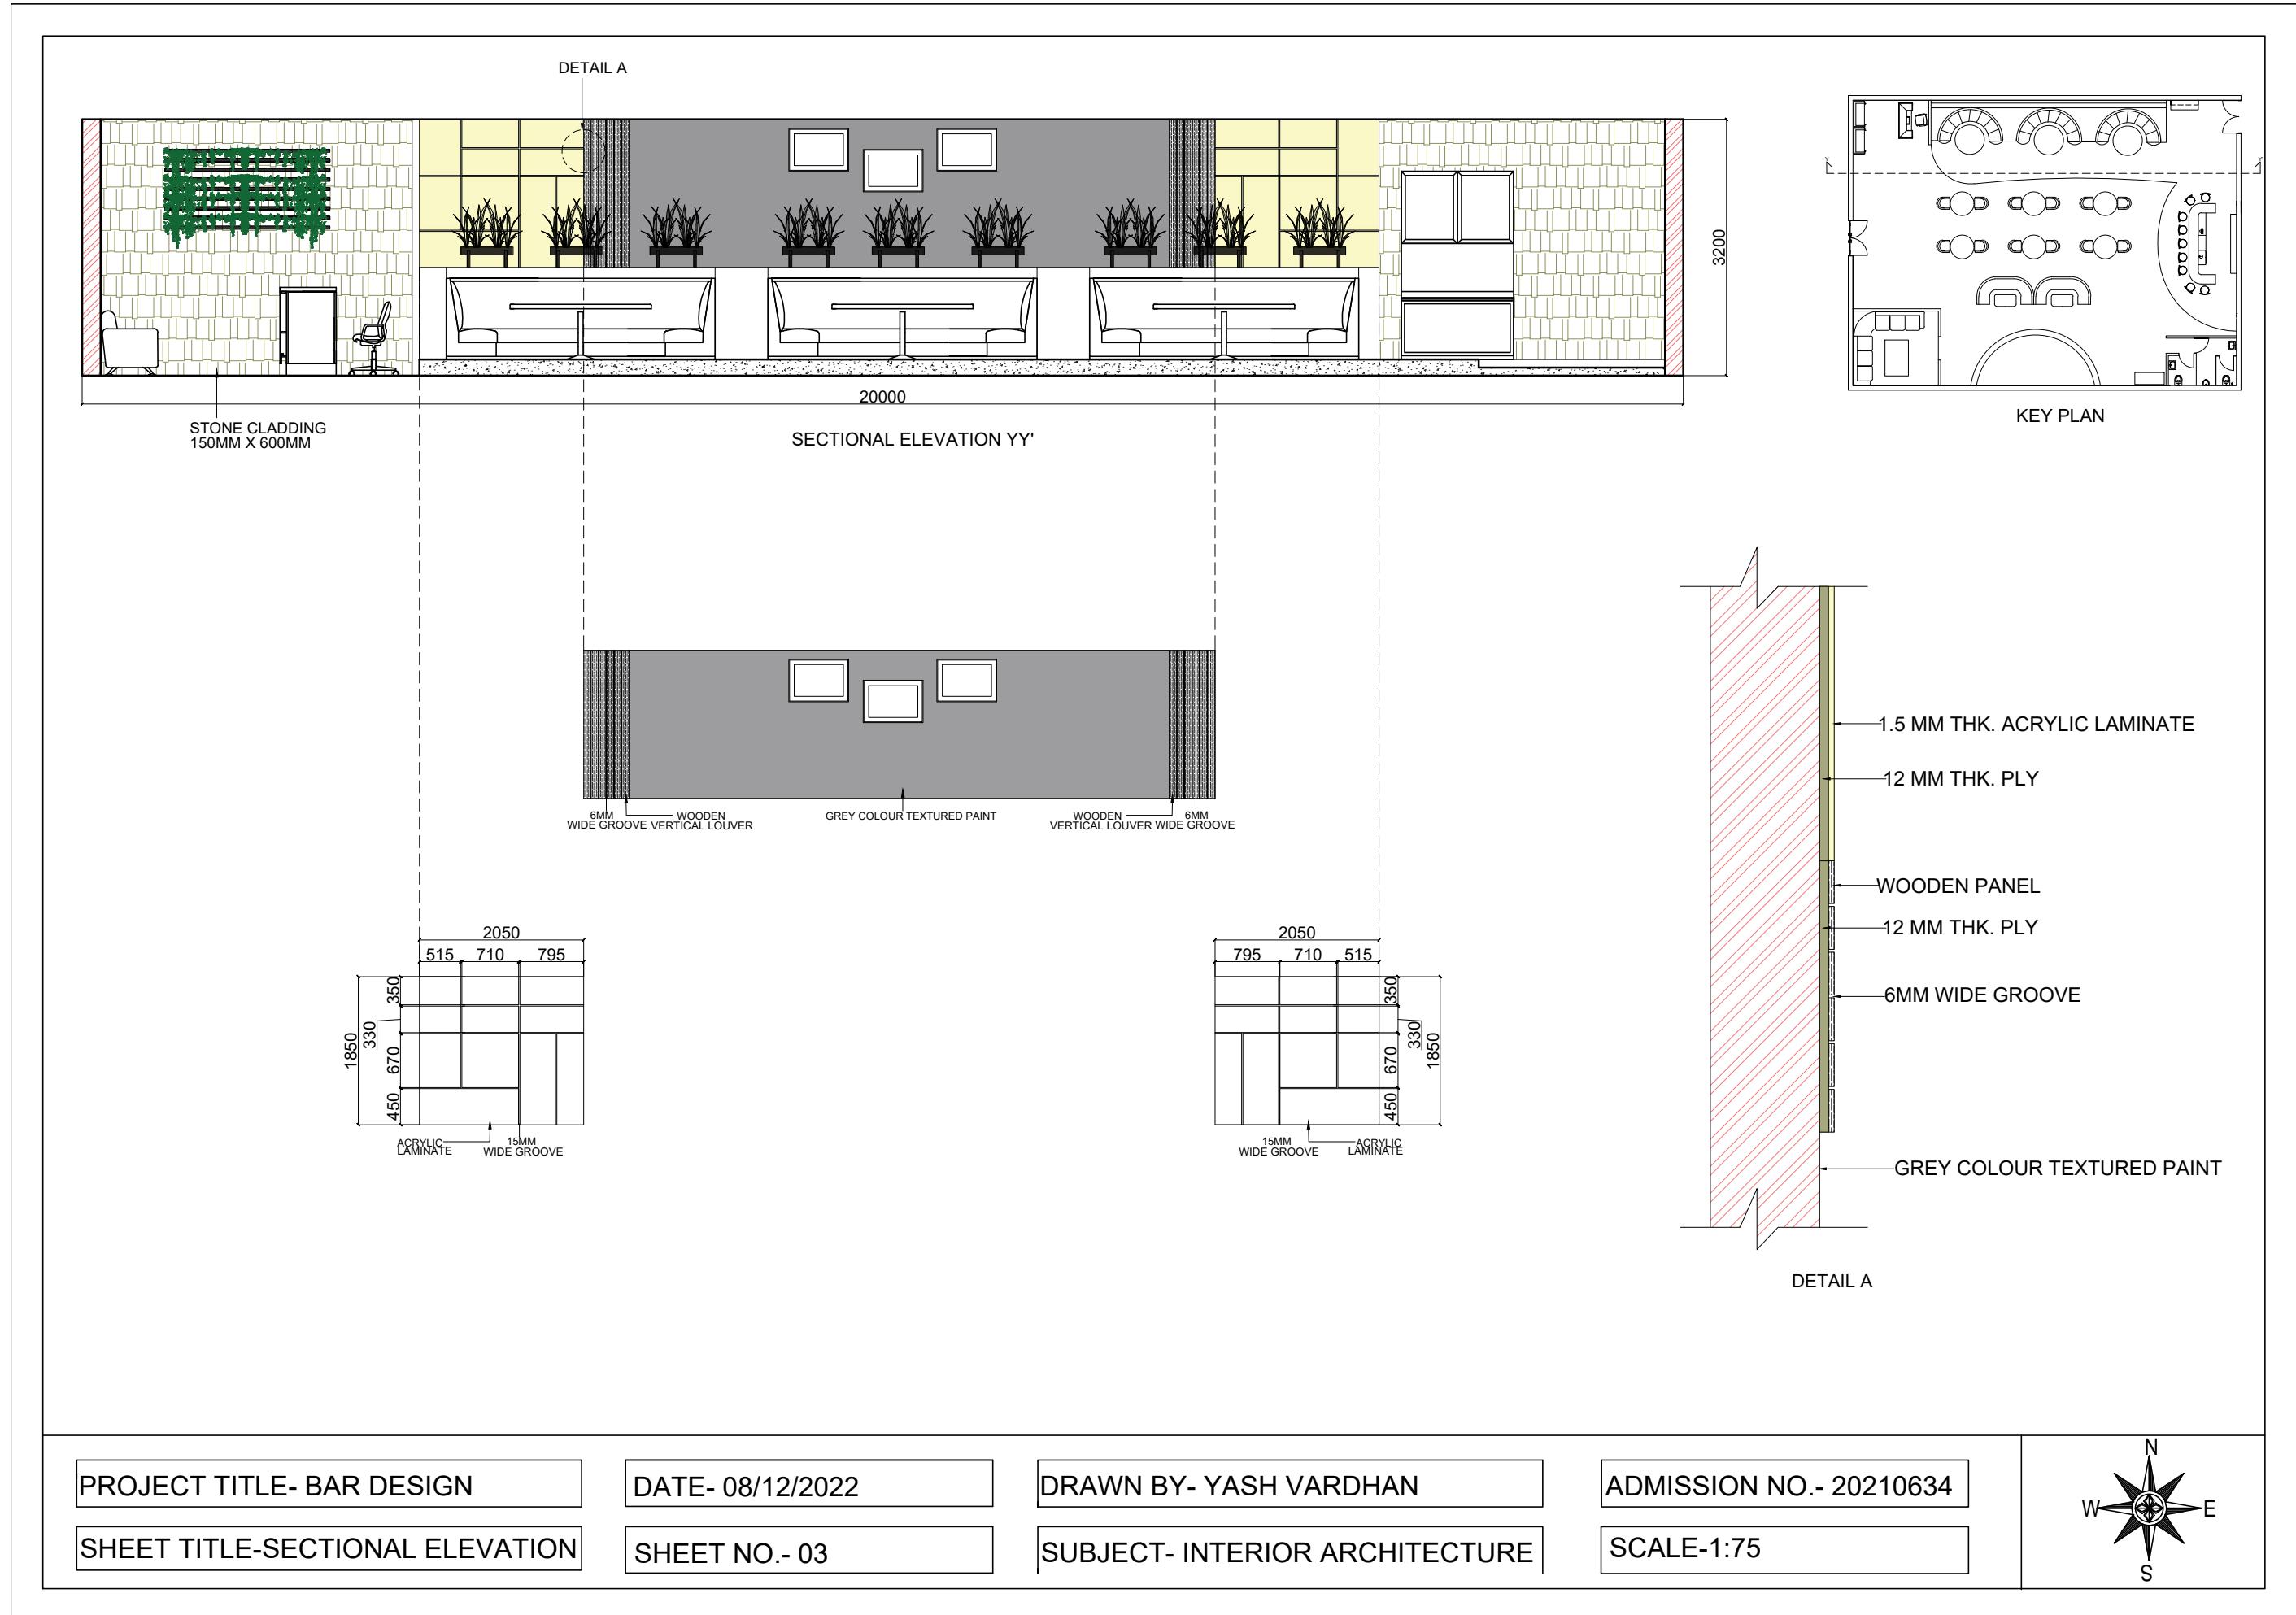

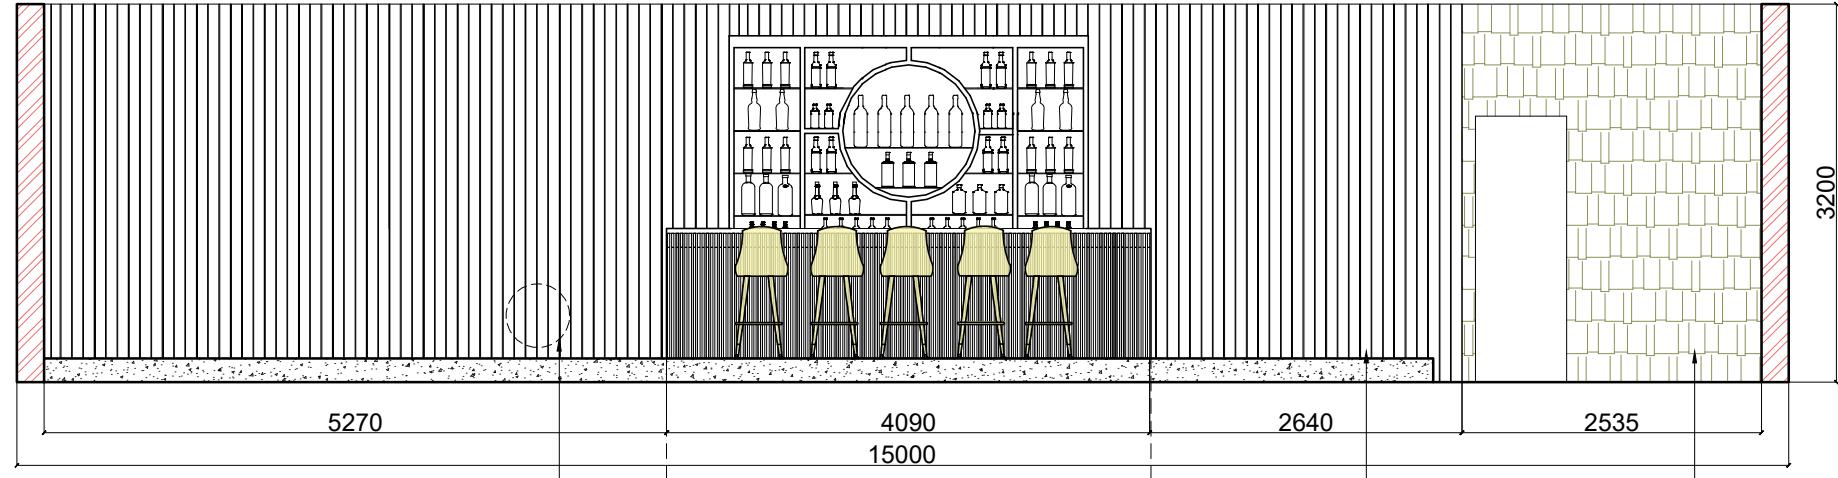


DETAIL A

SECTIONAL ELEVATION YY'

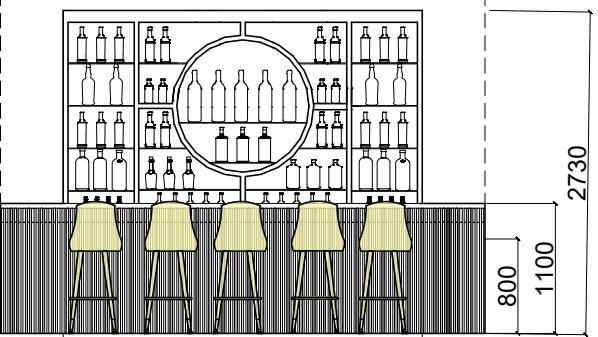
WOODEN
VERTICAL LOUVERSTONE CLADDING
300MM X 600MM

ROSE GOLD CHROME FINISH

BLACK LACQUER GLASS

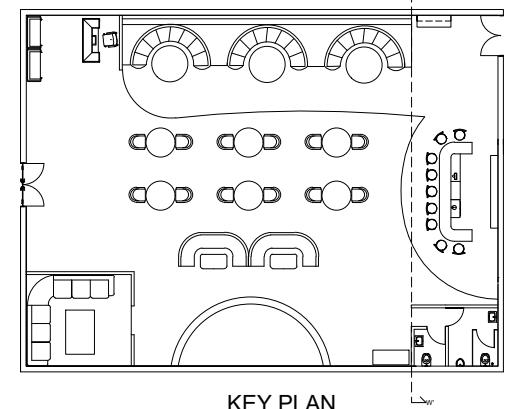

KEY PLAN

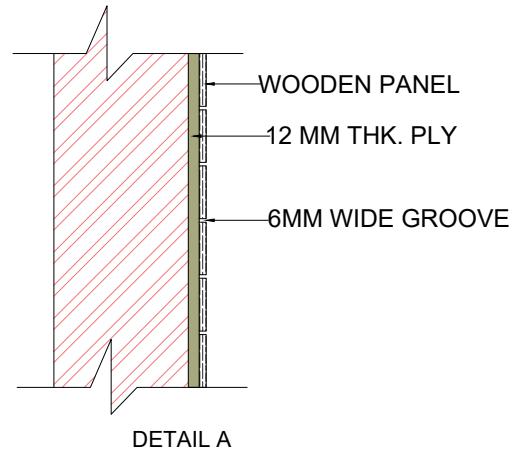

DETAIL A

PROJECT TITLE- BAR DESIGN

DATE- 08/12/2022

DRAWN BY- YASH VARDHAN


ADMISSION NO.- 20210634




SHEET TITLE-SECTIONAL ELEVATION

SHEET NO.- 04

SUBJECT- INTERIOR ARCHITECTURE

SCALE-1:75

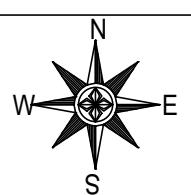

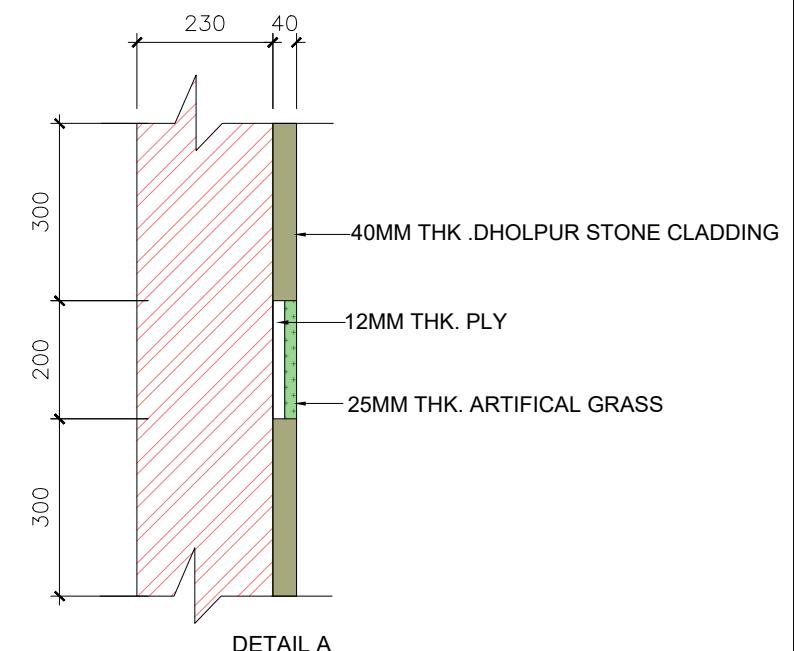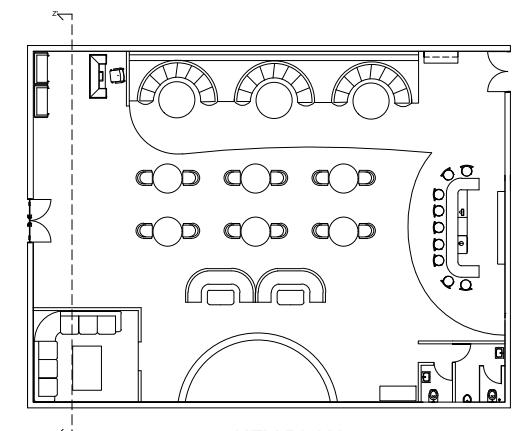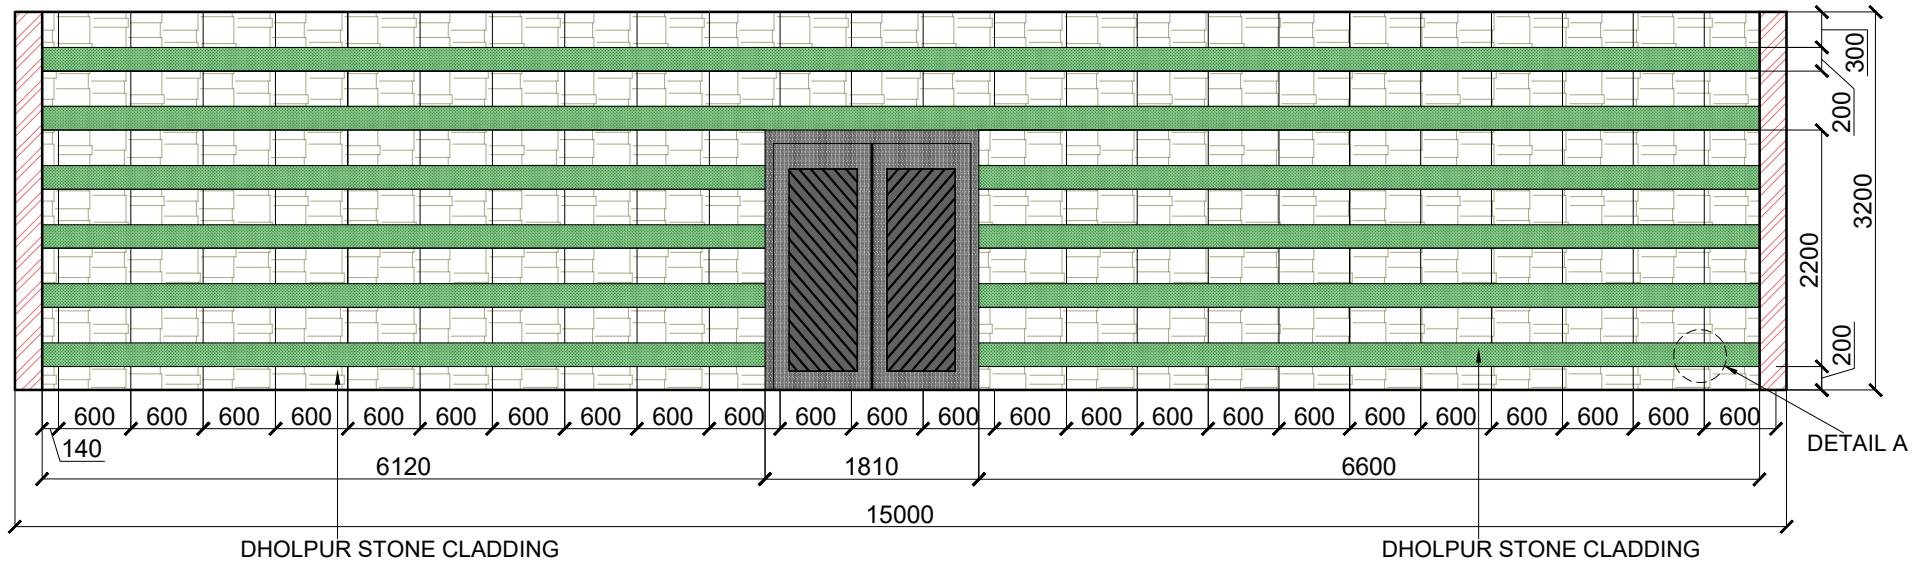

PROJECT TITLE- BAR DESIGN

DATE- 08/12/2022

DRAWN BY- YASH VARDHAN


ADMISSION NO.- 20210634





SHEET TITLE-SECTIONAL ELEVATION

SHEET NO.- 05

SUBJECT- INTERIOR ARCHITECTURE

SCALE-1:75

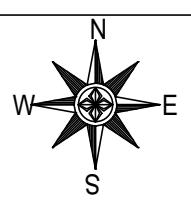

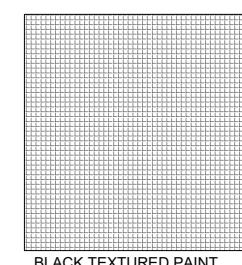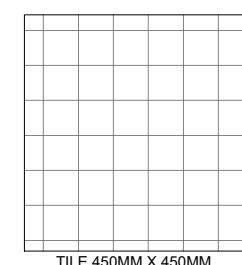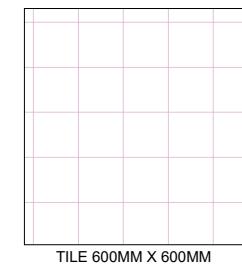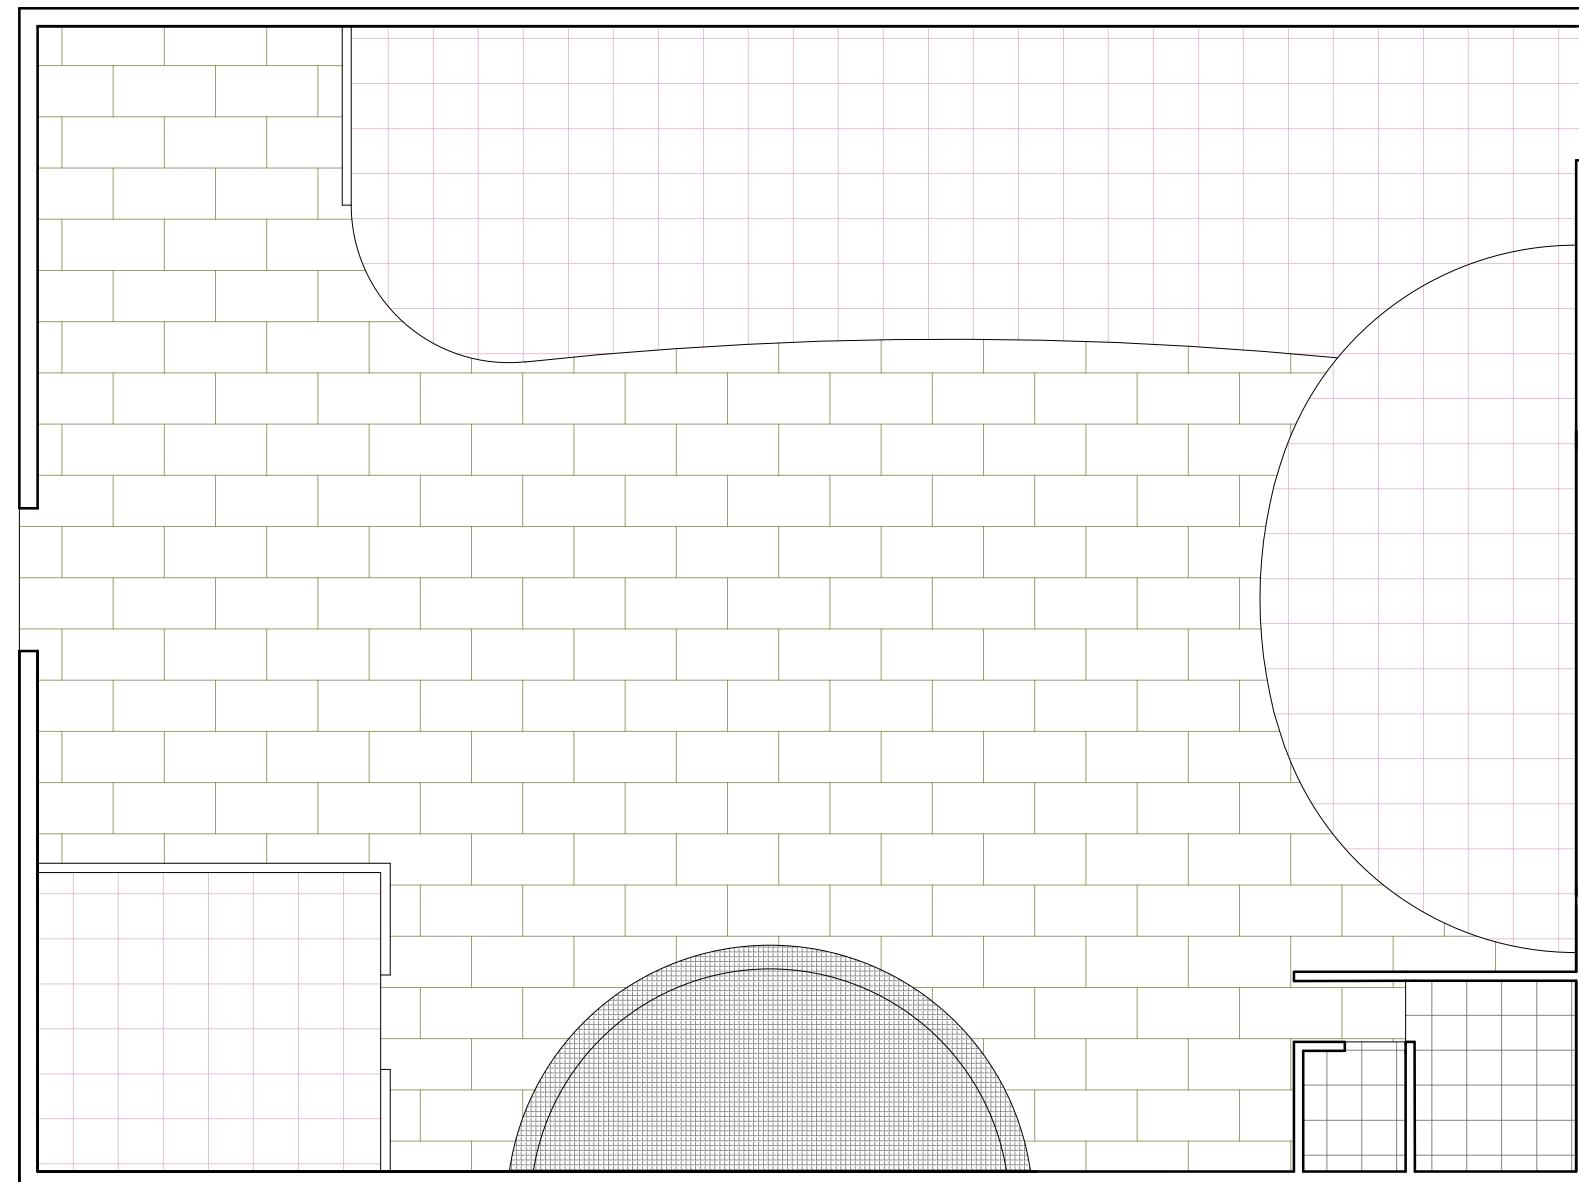

PROJECT TITLE- BAR DESIGN

DATE- 08/12/2022

DRAWN BY- YASH VARDHAN


ADMISSION NO.- 20210634


SHEET TITLE- FLOORING PLAN

SHEET NO.- 07

SUBJECT- INTERIOR ARCHITECTURE

SCALE-1:75

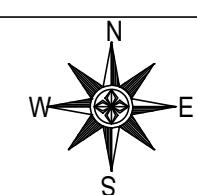

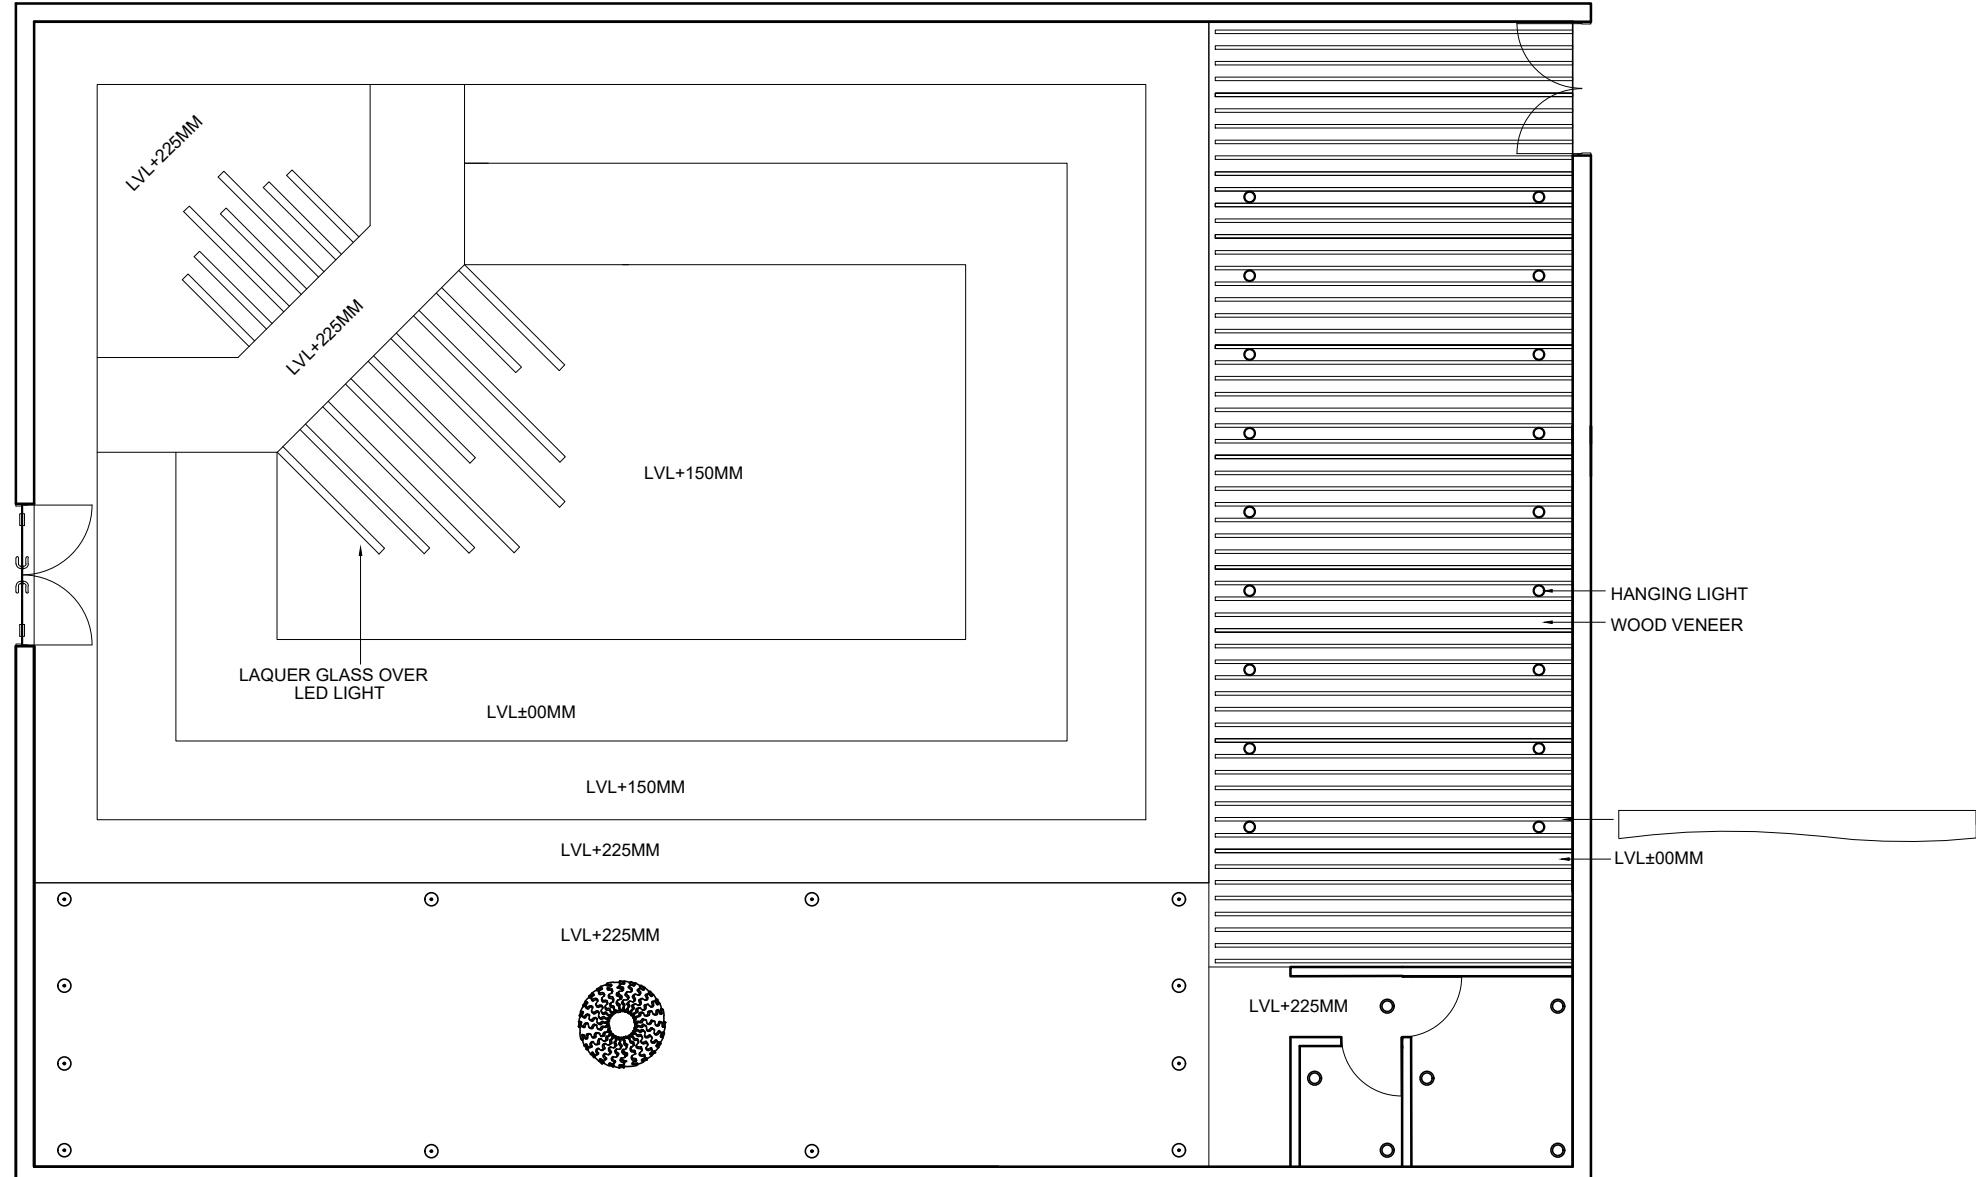

PROJECT TITLE- BAR DESIGN

DATE- 08/12/2022

DRAWN BY- YASH VARDHAN

ADMISSION NO.- 20210634

SHEET TITLE- CEILING PLAN

SHEET NO.- 06

SUBJECT- INTERIOR ARCHITECTURE

SCALE-1:75

