

UID-SOA

NOTES

LEGENDS

KEY PLAN

SHEET TITLE


LIST OF DRAWINGS

SHEET NO.: 00
SCALE : 1:100PROJECT
HOSTEL WORKING DRW.DRAWN BY
YASH VARDHAN

CHECKED BY

HOSTEL WORKING DRAWINGS :

DRG. NO.	DRAWING TITLE	REV.	SCALE
PLANS			
01	SETTING OUT PLAN	4	1:200
02	GRID PLAN	1	1:150
03	COLUMN LAYOUT	3	1:150
04	EXCAVATION PLAN	2	1:150
05	BASEMENT PLAN	2	1:150
06	GROUND FLOOR PLAN	6	1:150
07	FIRST FLOOR PLAN	-	1:150
08	SECOND FLOOR PLAN	-	1:150
09	THIRD FLOOR PLAN	-	1:150
10	FOURTH FLOOR PLAN	-	1:150
11	TERRACE FLOOR PLAN	-	1:150
12	SECTION XX'	3	1:100
13	SECTION YY'	3	1:100
14	ELEVATIONS	1	1:150
15	ELEVATIONS	1	1:150
16	WASHROOM DETAIL	1	1:20
17	KITCHEN DETAIL- RESIDENCE	1	1:20
18	KITCHEN DETAIL- HOSTEL	1	1:20
19	STAIRCASE DETAIL	1	1:50
20	LIFT DETAIL	-	1:50

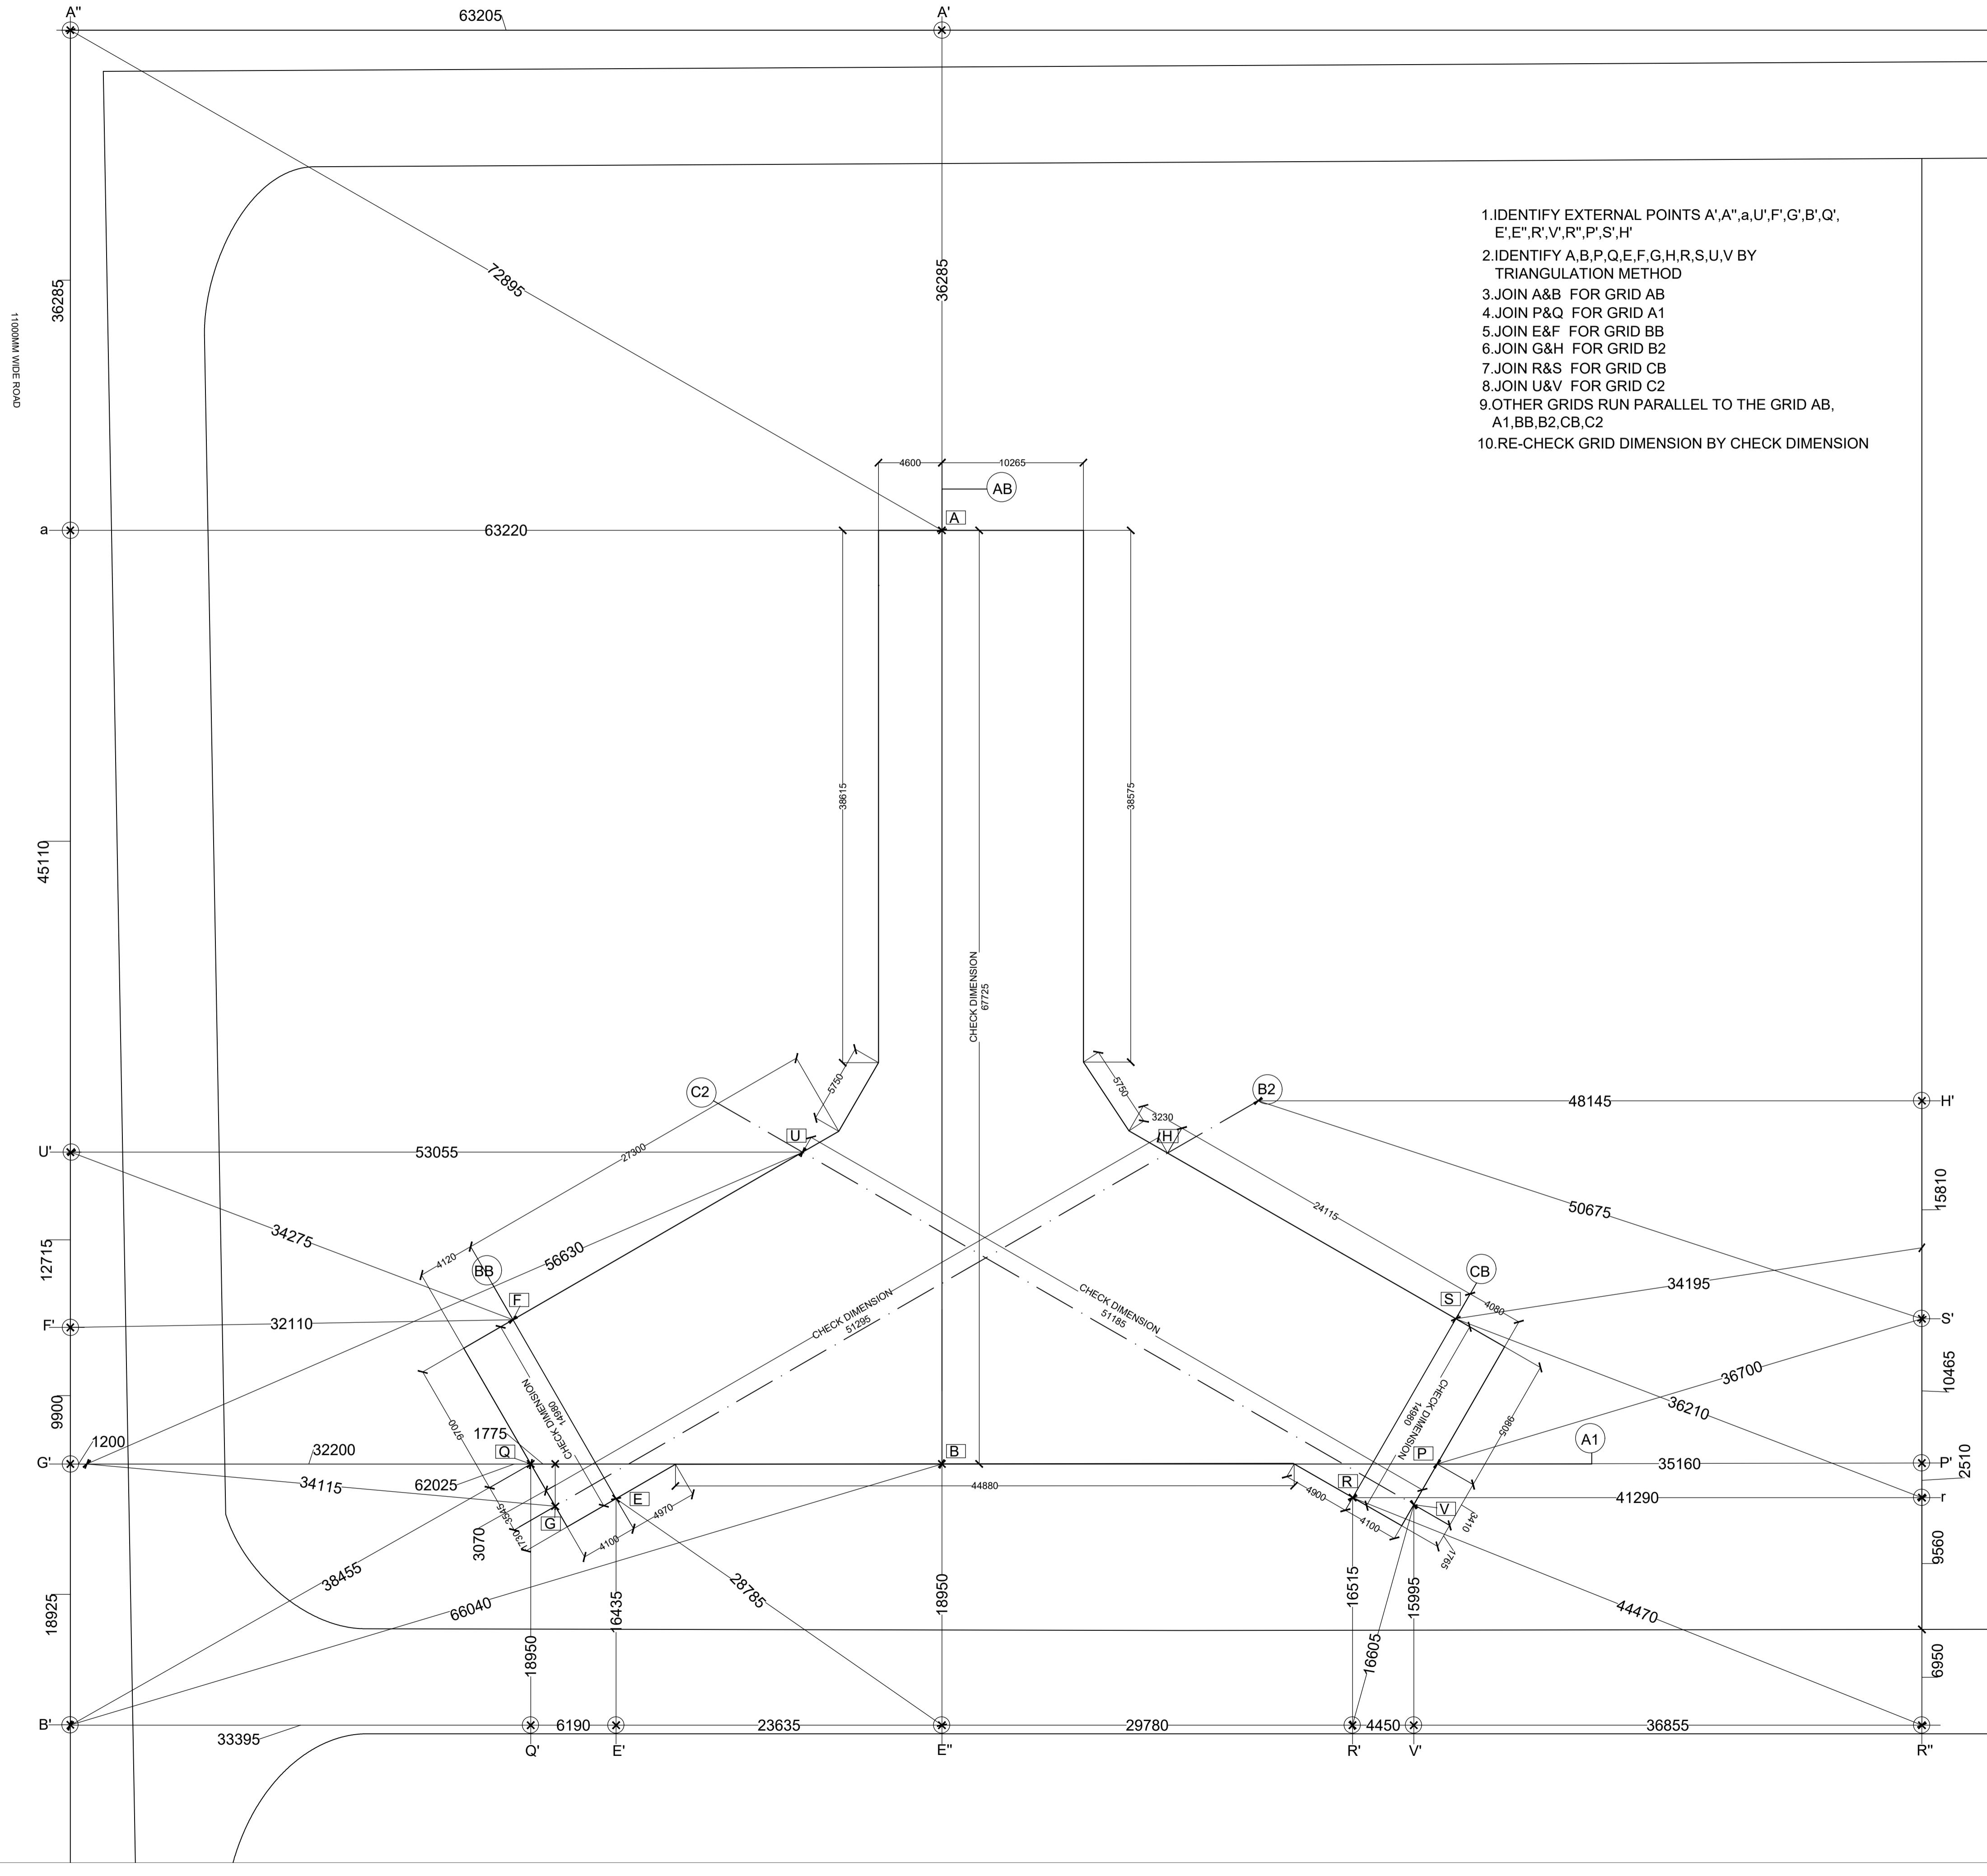

UID-SOA

NOTES :

ALL DIMENSIONS ARE IN MM
ALL DIMENSIONS TO BE READ NOT MEASURED

LEGENDS :

KEY PLAN :

SHEET TITLE :
SET-OUT PLAN

SHEET NO. : 01
SCALE : 1 :200

PROJECT TITLE :

HOSTEL WORKING DRW.

DRAWN BY :	CHECKED BY :
YASH VARDHAN	

UID-SOA

NOTES

ALL DIMENSIONS ARE IN MM
ALL DIMENSIONS TO BE READ NOT MEASURED

LEGENDS

KEY PLAN

SHEET TITLE


GRID PLAN

SHEET NO. : 02
SCALE : 1 :150

PROJECT

HOSTEL WORKING DRW.

DRAWN BY	CHECKED BY
YASH VARDHAN	

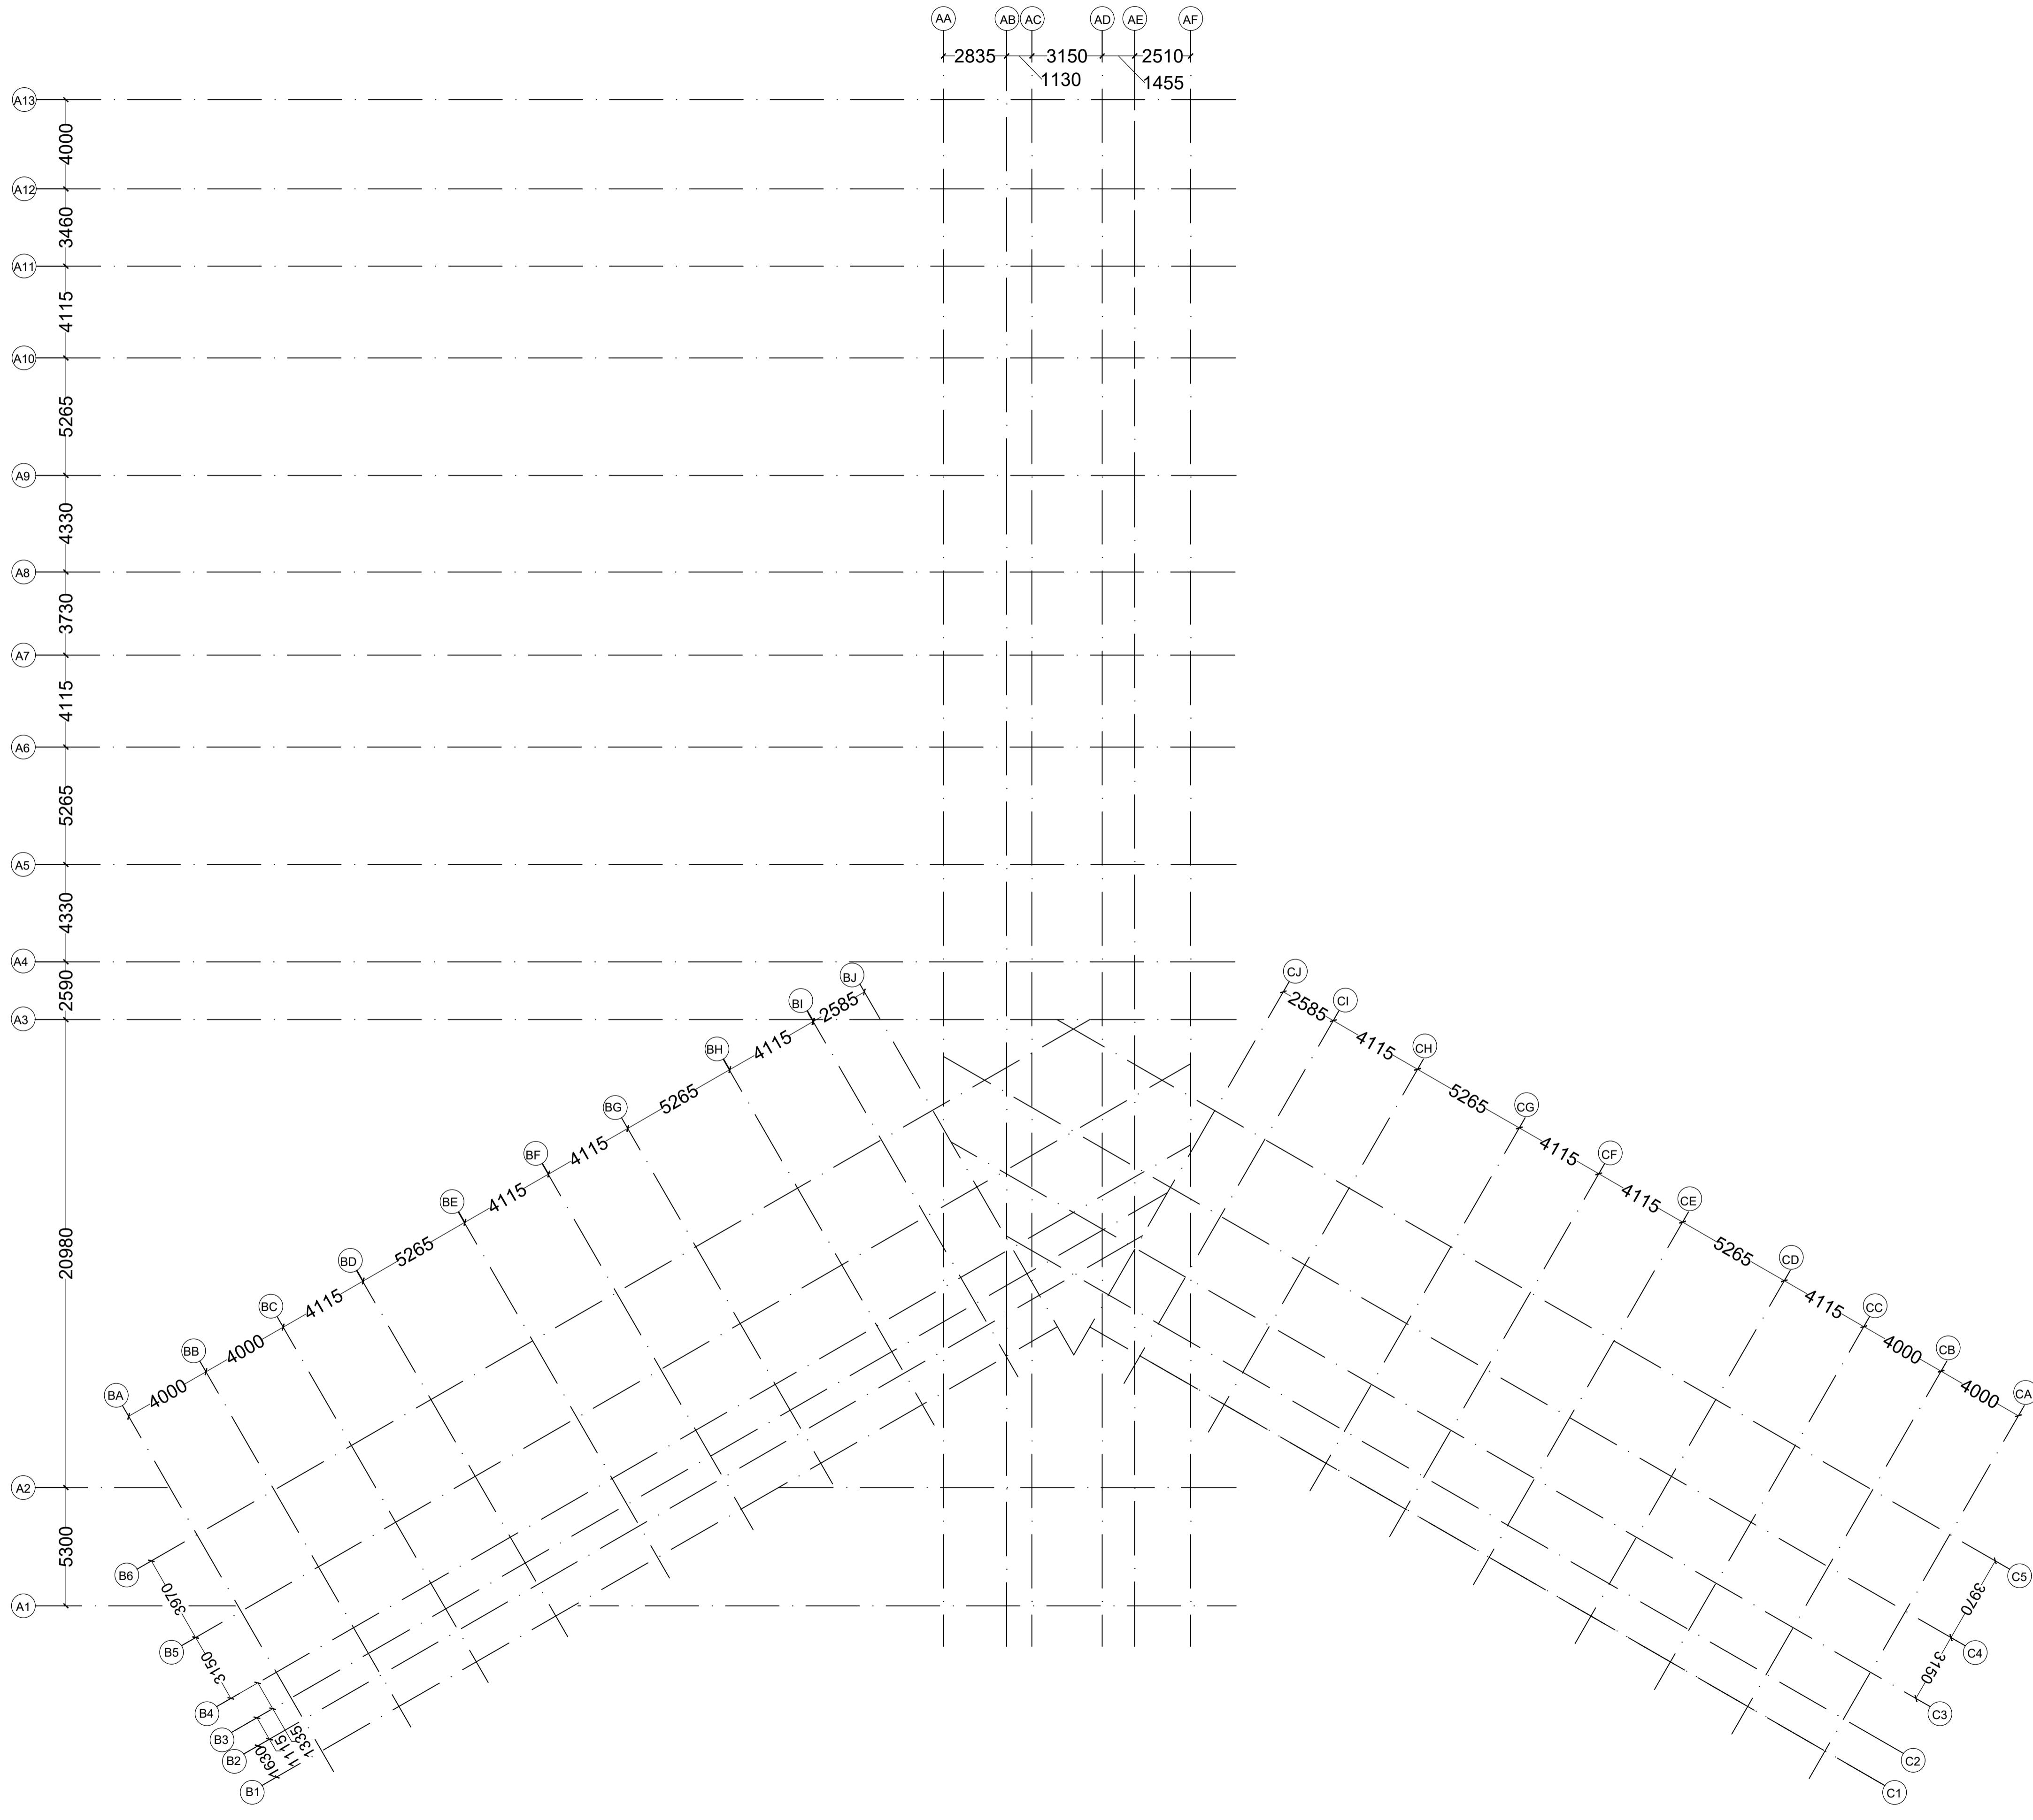

UID-SOA

NOTES

ALL DIMENSIONS ARE IN MM
ALL DIMENSIONS TO BE READ NOT MEASURED

LEGENDS

KEY PLAN


SHEET TITLE

COLUMN LAYOUT

SHEET NO. : 03
SCALE : 1 :150

PROJECT HOSTEL WORKING DRW.

DRAWN BY	CHECKED BY
YASH VARDHAN	

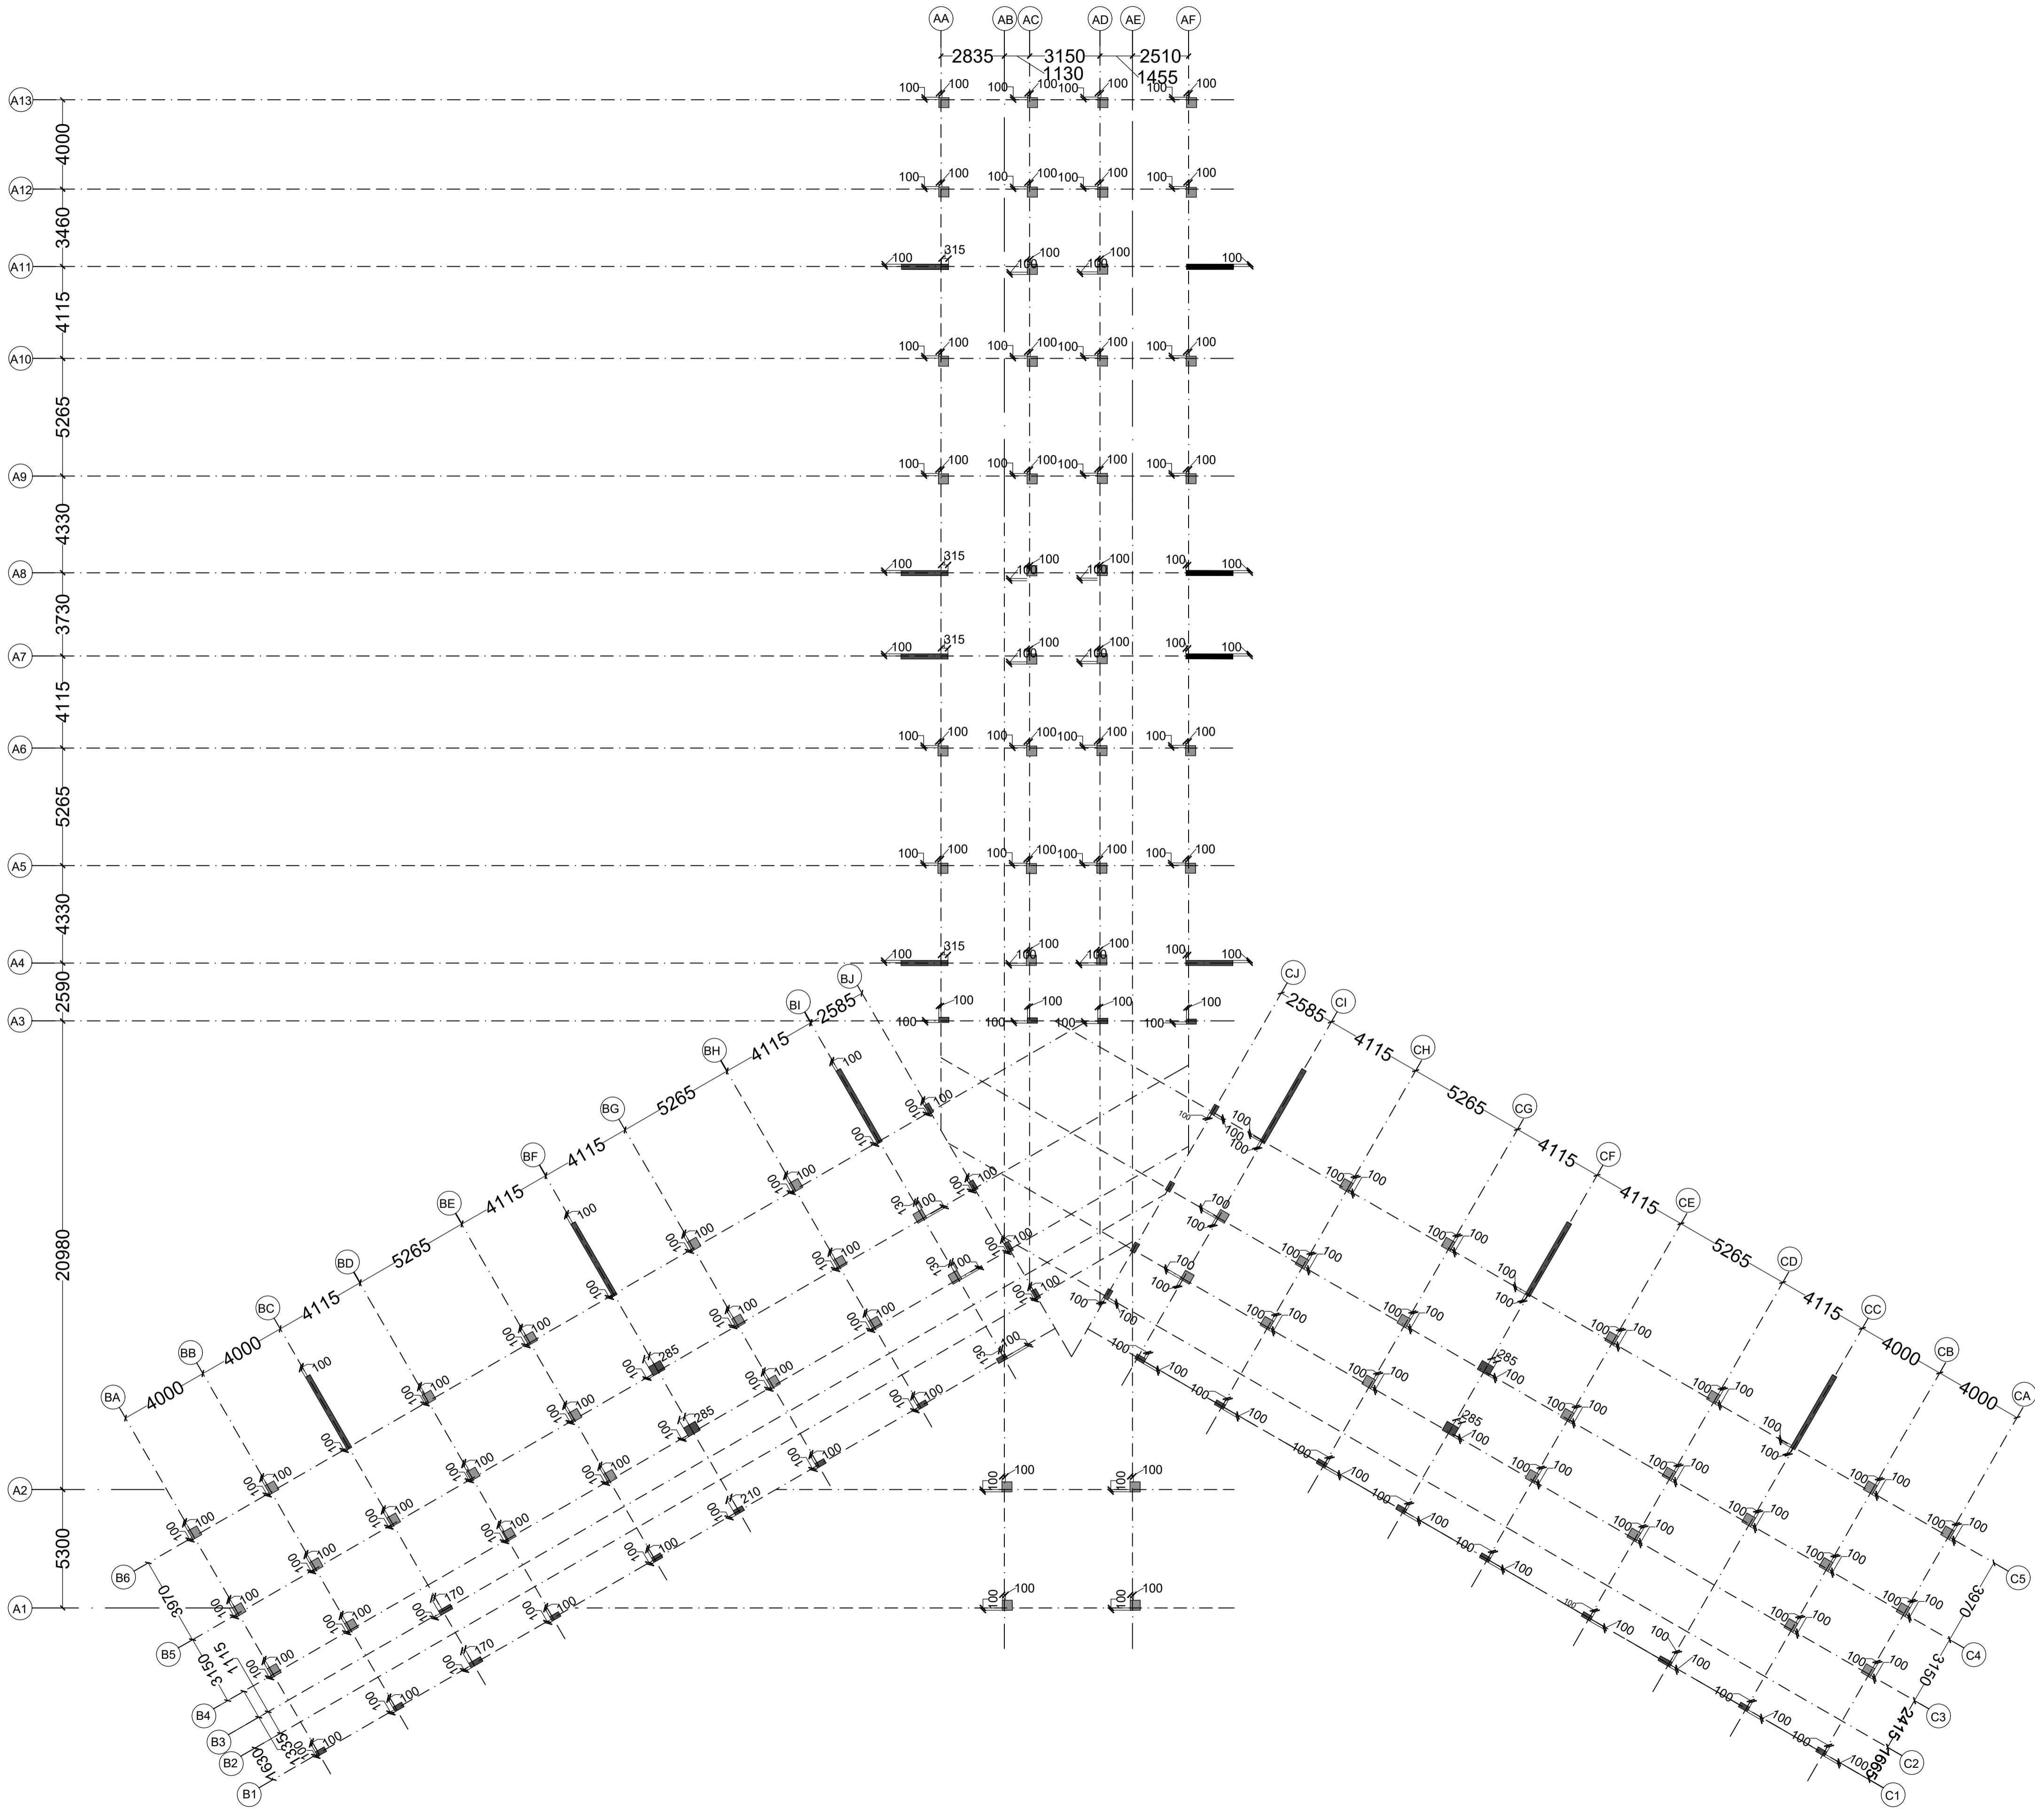

UID-SOA

NOTES

ALL DIMENSIONS ARE IN MM
ALL DIMENSIONS TO BE READ NOT MEASURED

LEGENDS

KEY PLAN

SHEET TITLE

EXCAVATION PLAN


SHEET NO. : 04

SCALE : 1 : 150



PROJECT
HOSTEL WORKING DRW.

DRAWN BY YASH VARDHAN | CHECKED BY

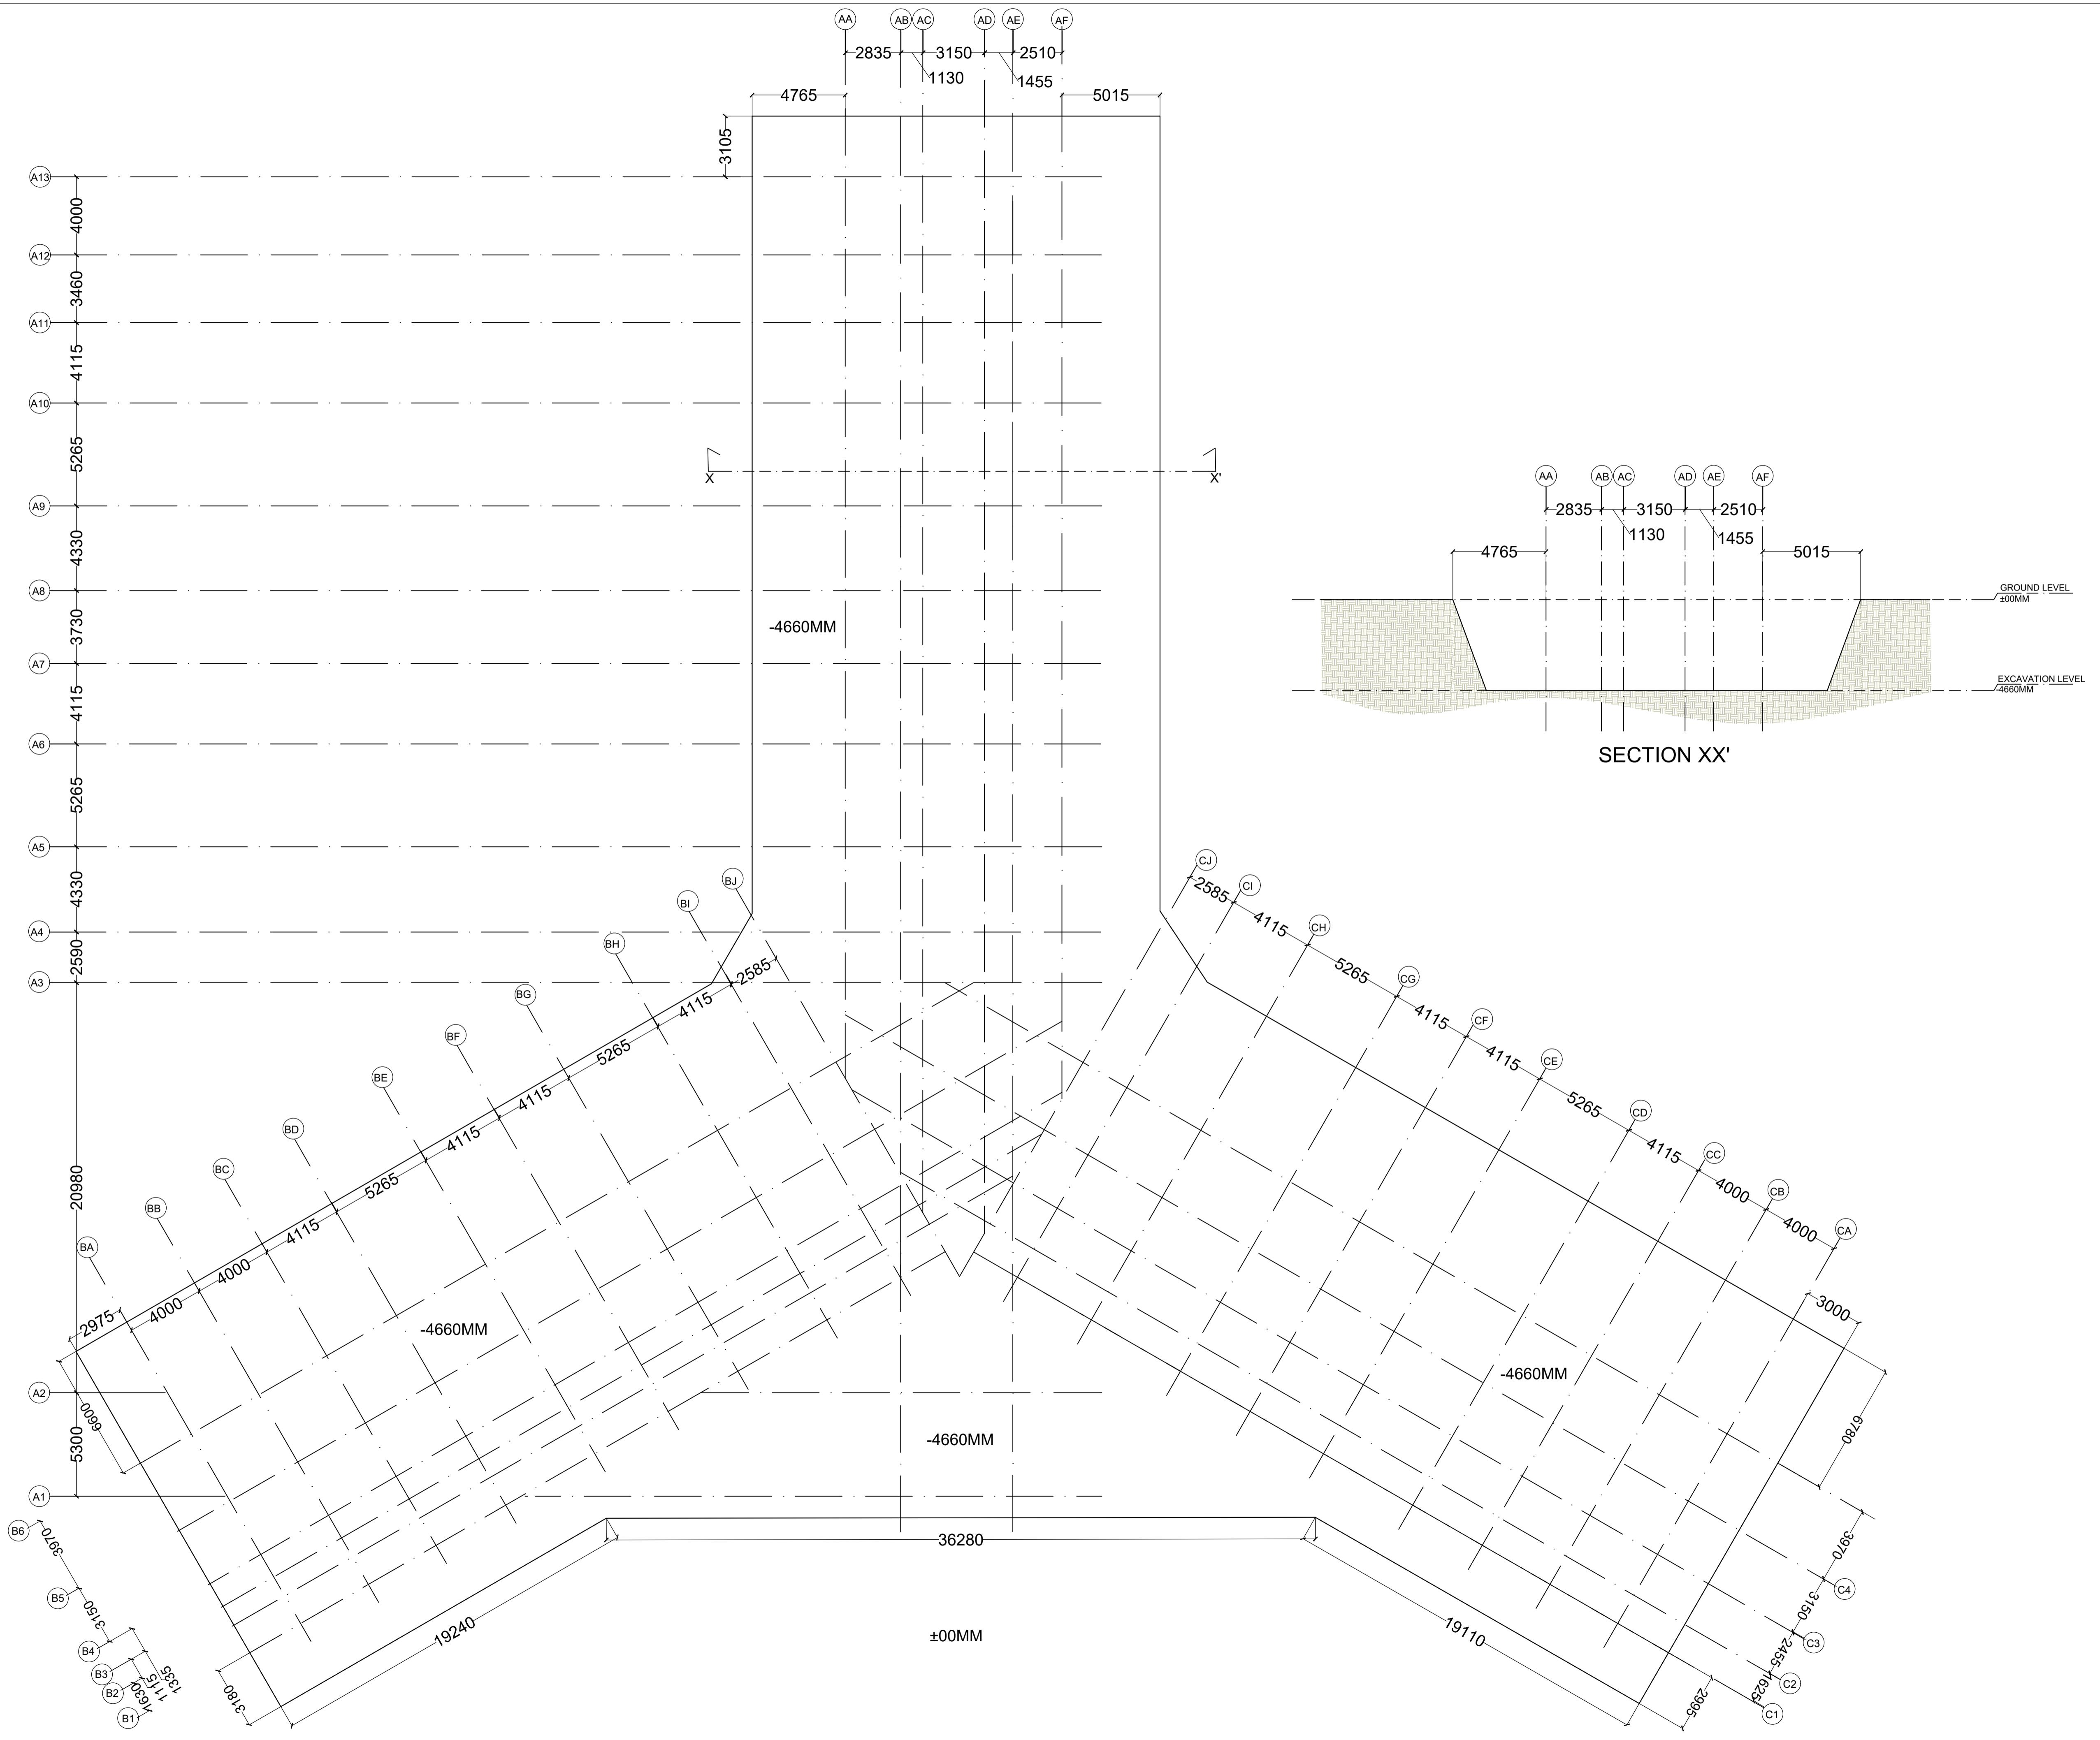

UID-SOA

NOTES

ALL DIMENSIONS ARE IN MM
ALL DIMENSIONS TO BE READ NOT MEASURED

LEGENDS

KEY PLAN

SHEET TITLE
BASEMENT PLAN


SHEET NO.: 05
SCALE : 1:150



PROJECT
HOSTEL WORKING DRW.

DRAWN BY
YASH VARDHAN

CHECKED BY

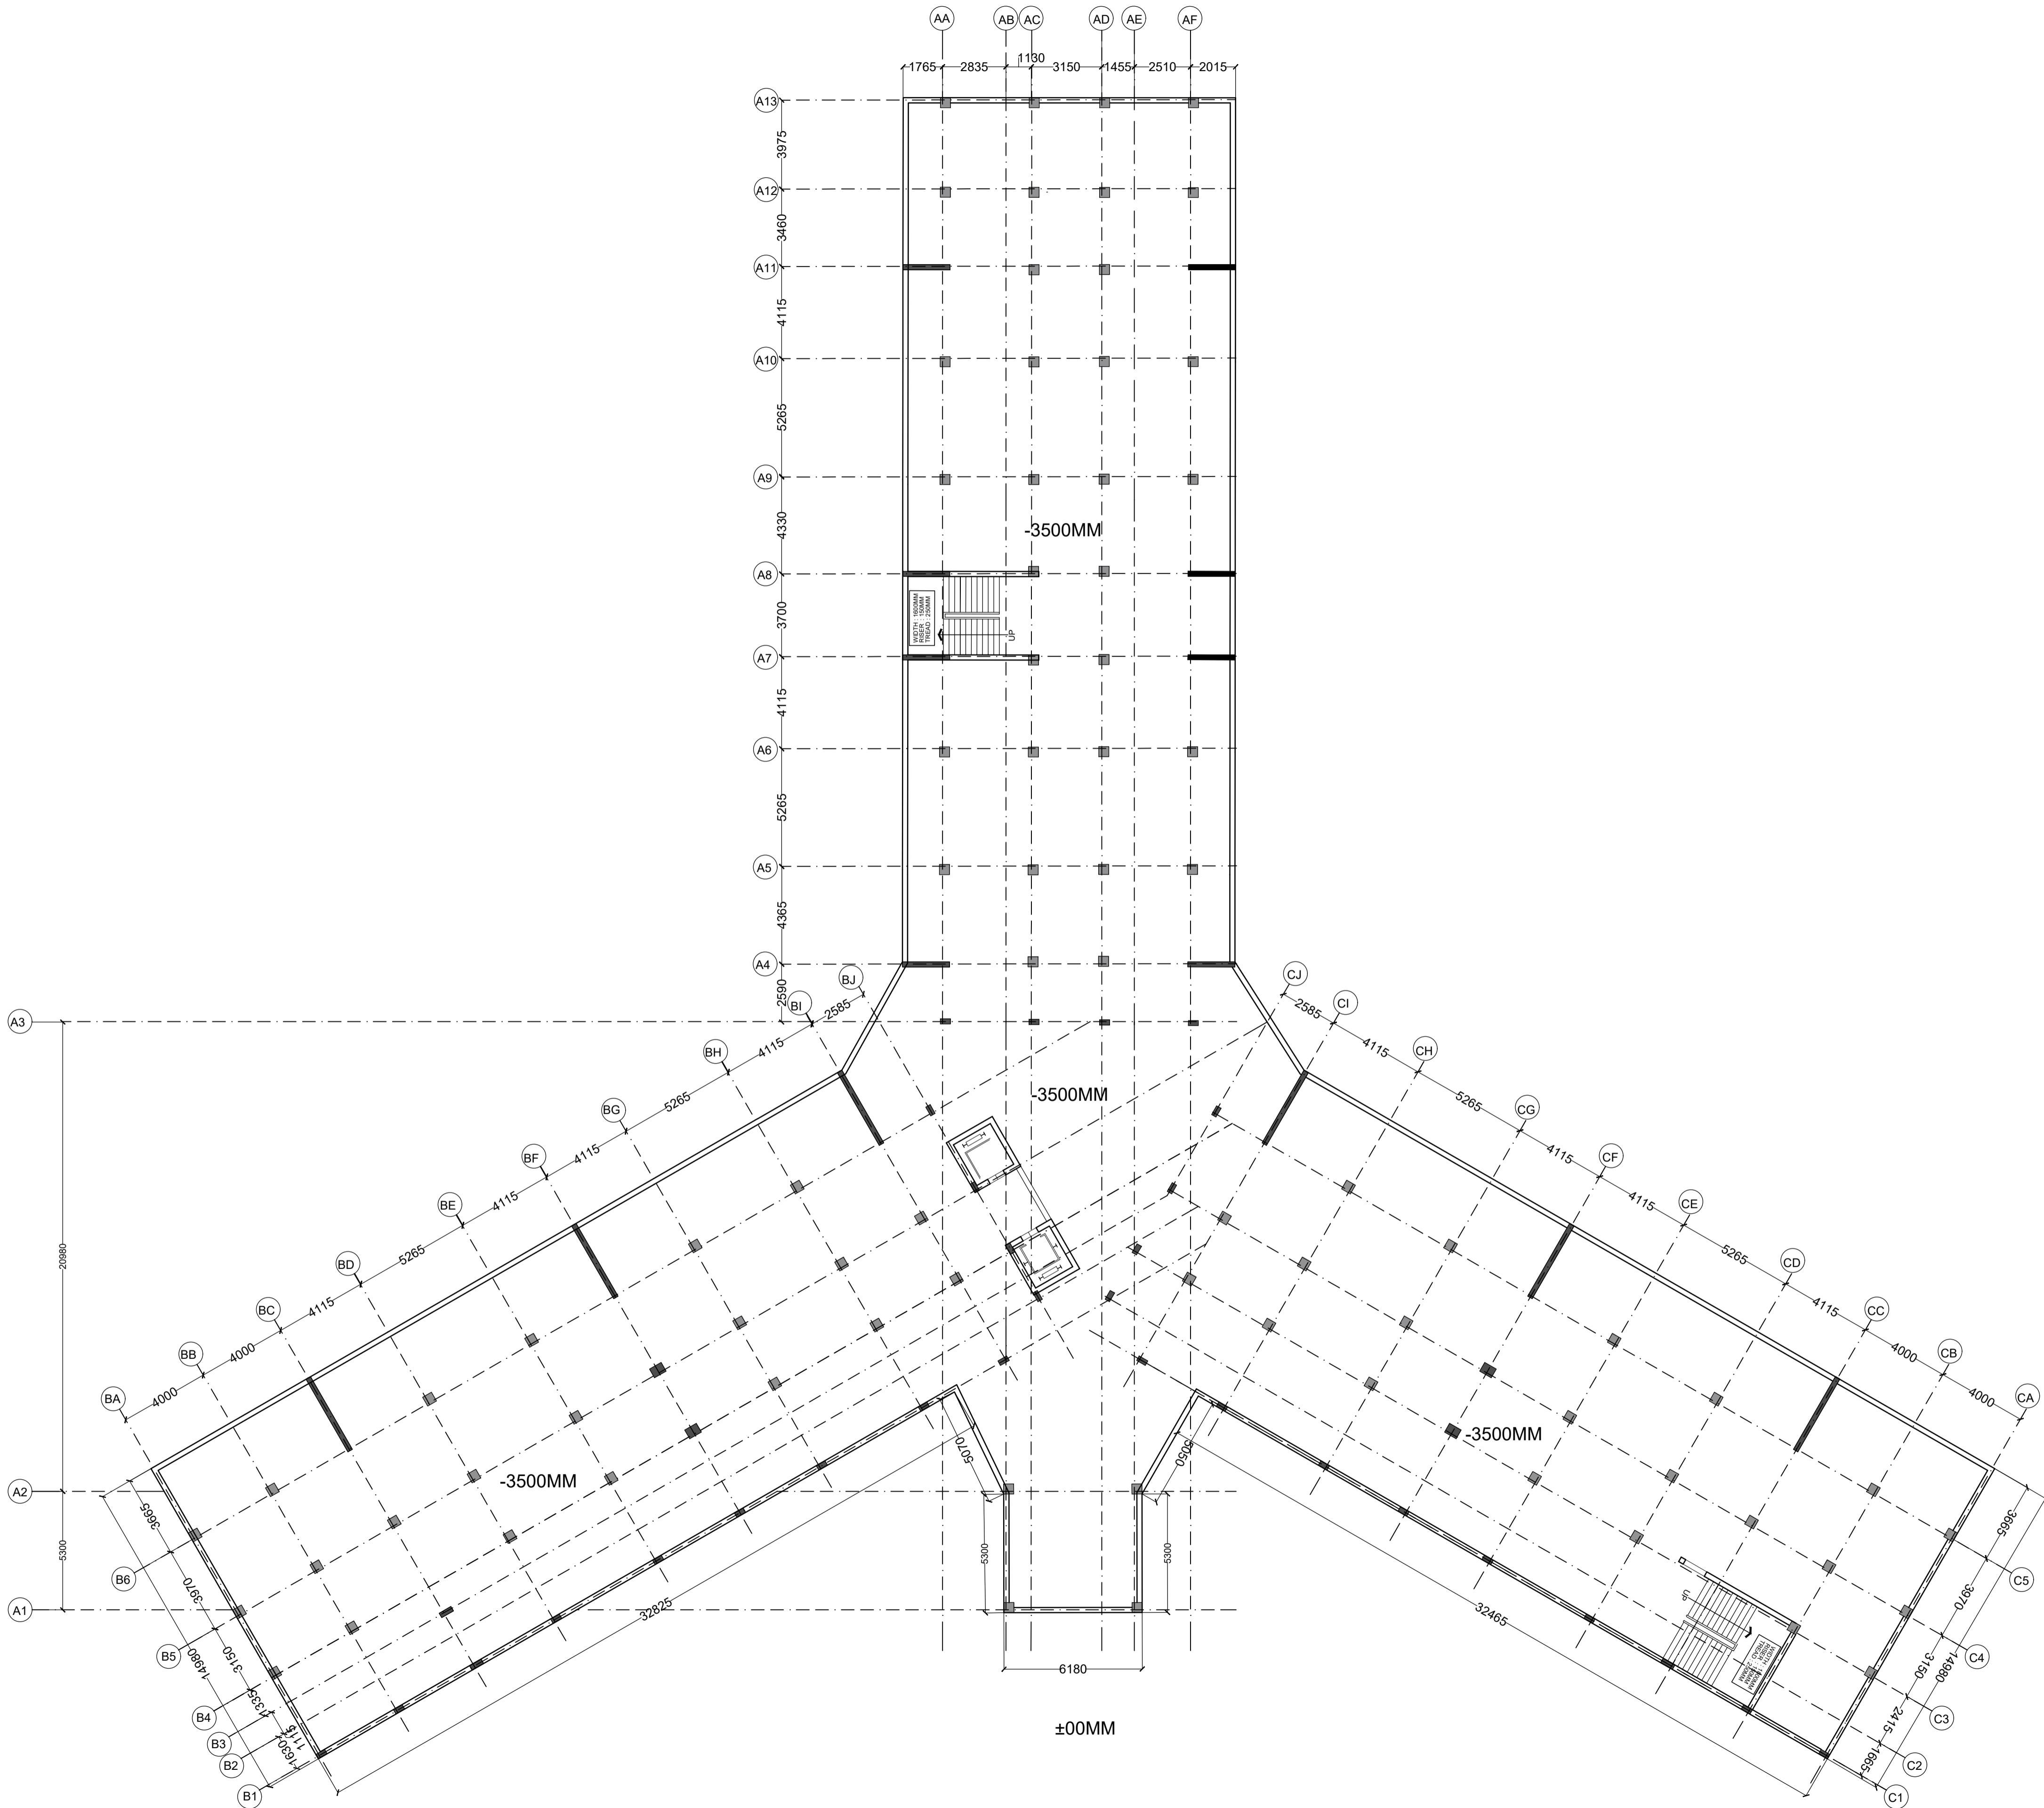


UID-SOA

NOTES

ALL DIMENSIONS ARE IN MM
ALL DIMENSIONS TO BE READ NOT MEASURED

LEGENDS

KEY PLAN

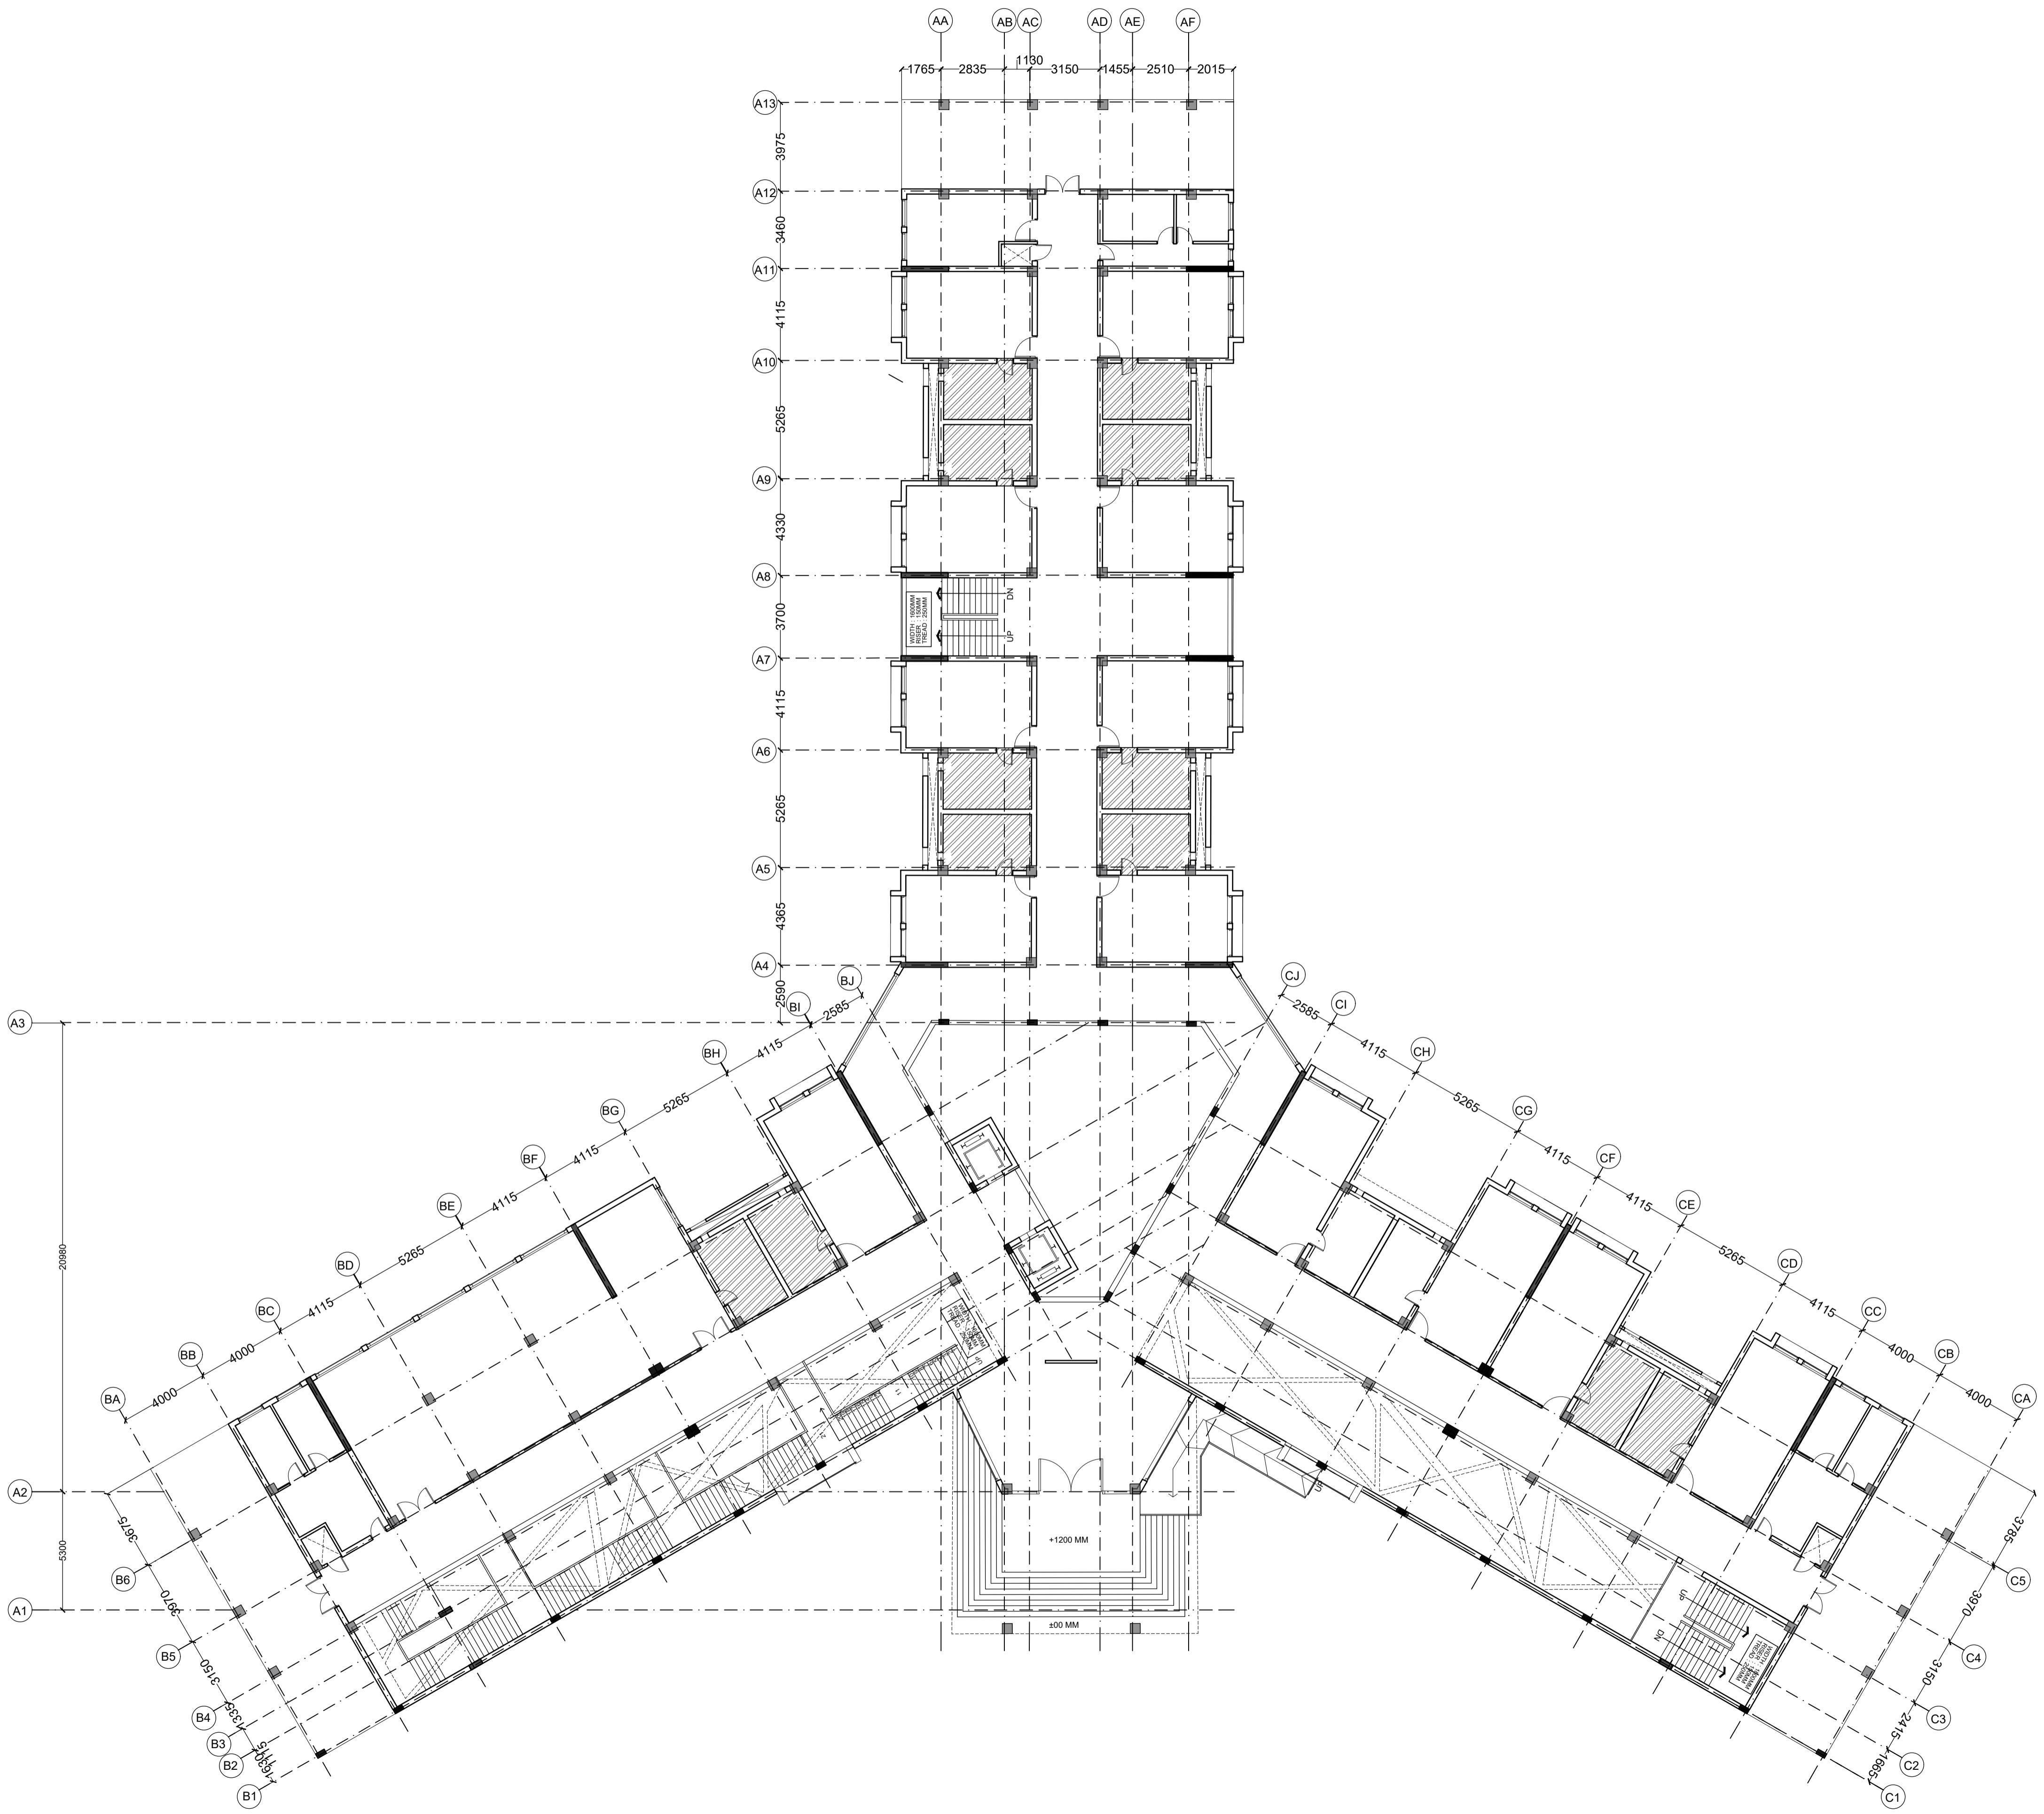

SHEET TITLE
GROUND FLOOR PLAN

SHEET NO.: 06
SCALE : 1:150



PROJECT
HOSTEL WORKING DRW.

DRAWN BY
YASH VARDHAN

CHECKED BY

UID-SOA

WINDOW SCHEDULE			
S.No.	Sill	Lintel	Width
W1	600	2300	1235
W2	600	2600	550
W3	600	2300	3000
W4	600	2300	1800
W5	600	2300	1400
W6	350	2600	2400
W7	00	2250	4040
W8	450	2600	2400



DOOR SCHEDULE			
S.No.	Sill	Lintel	Width
D1	0	2250	1000
D2	0	2250	850
D3	0	2250	1800
D4	0	2250	1800
D5	0	2250	3200

NOTES


ALL DIMENSIONS ARE IN MM
ALL DIMENSIONS TO BE READ NOT MEASURED

LEGENDS

KEY PLAN

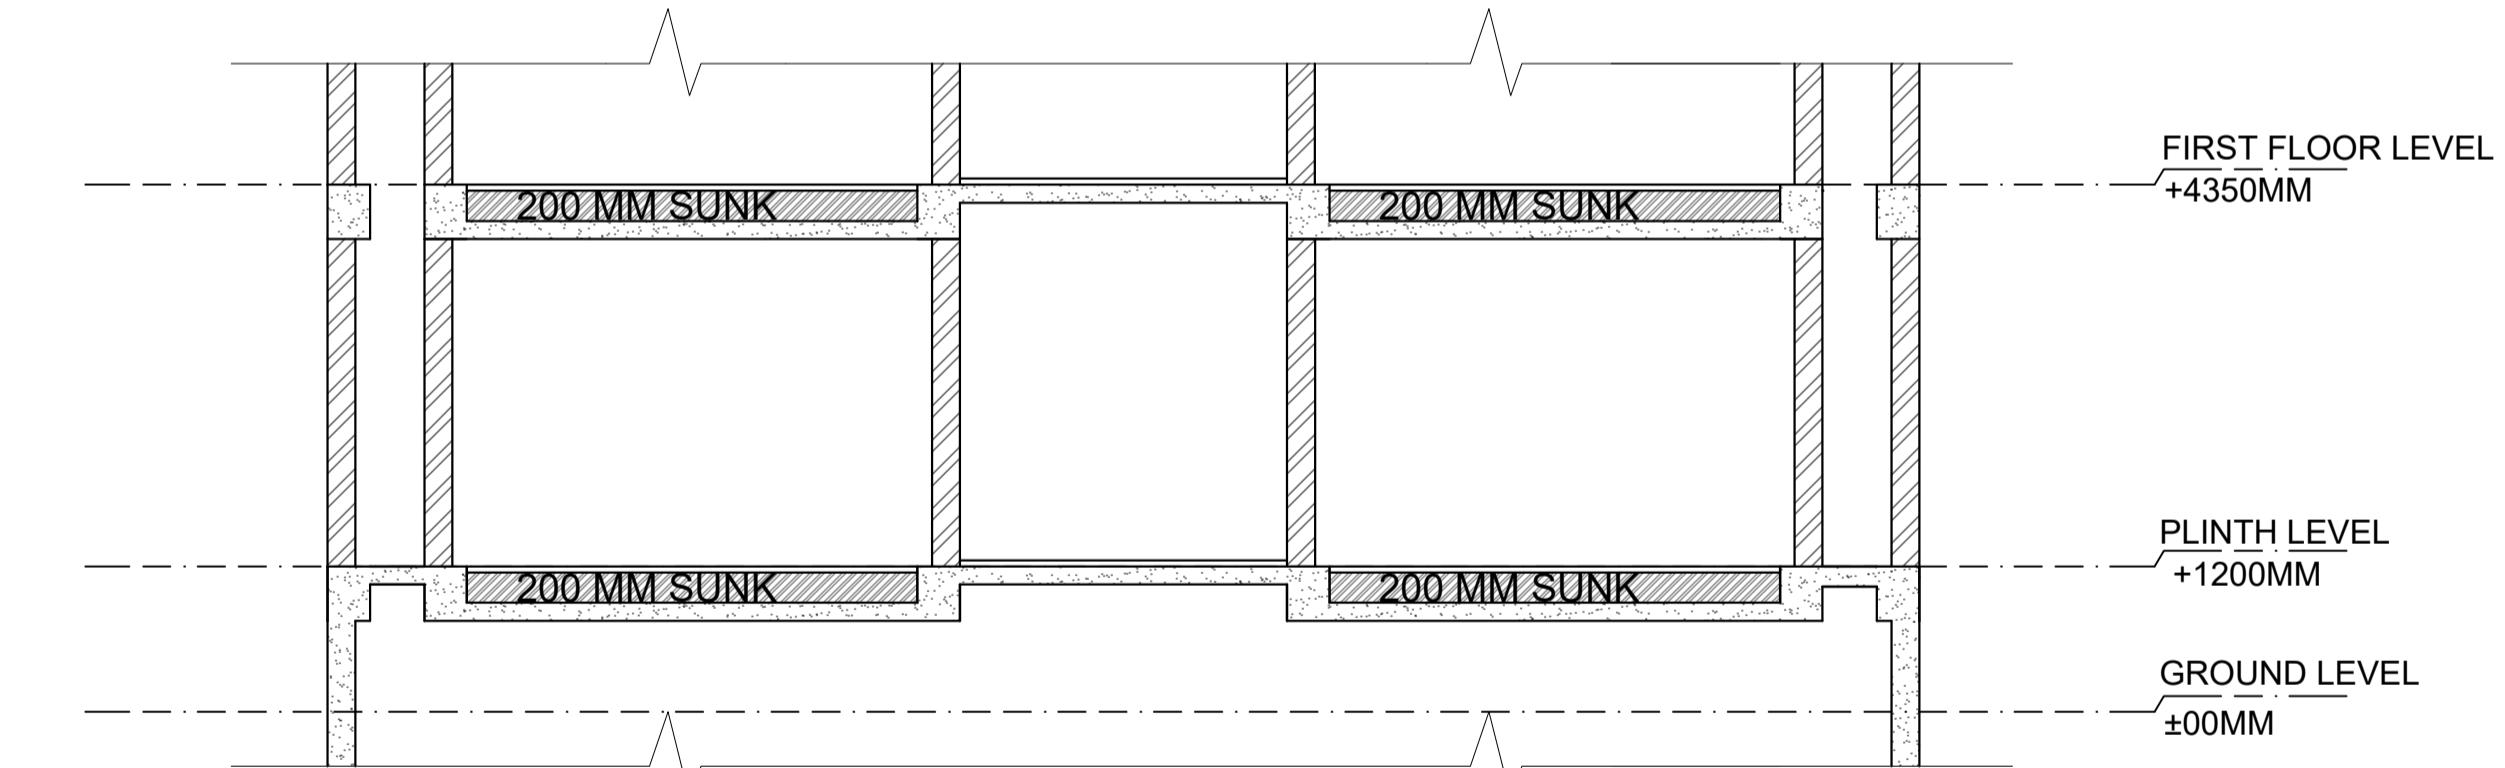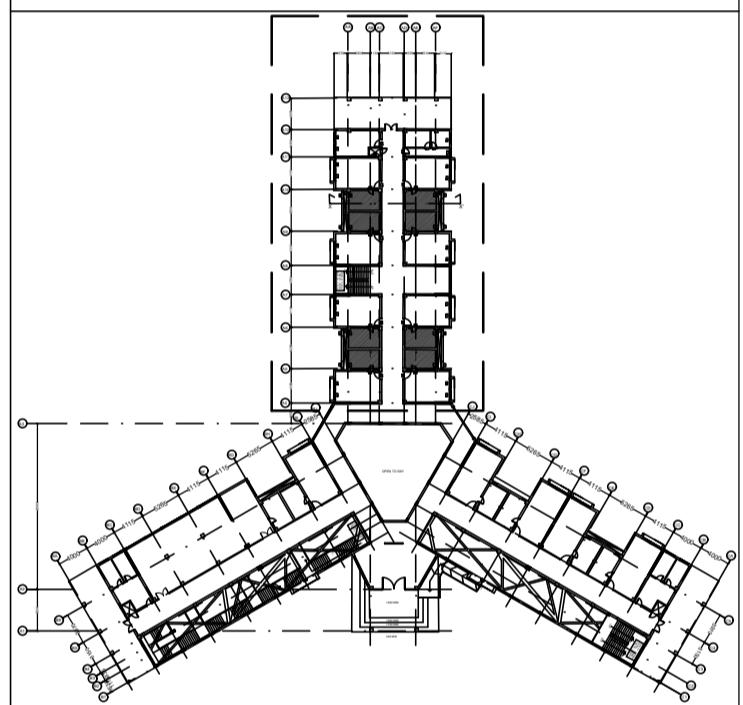

SECTION X

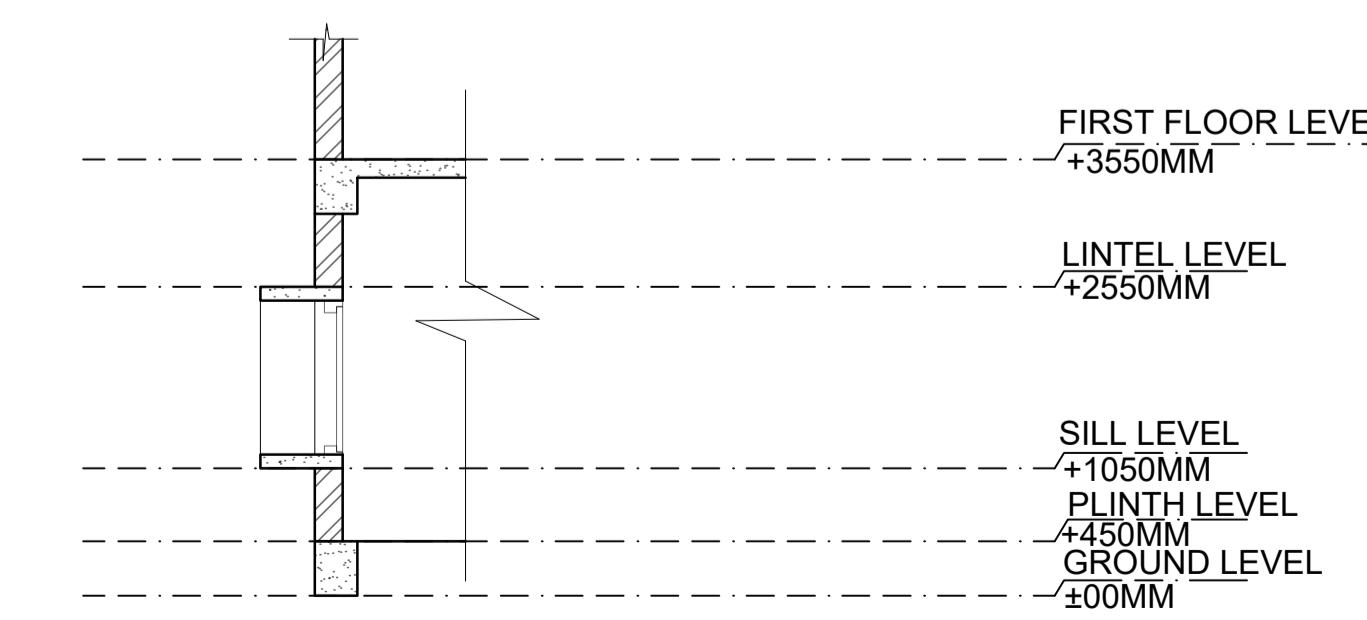

SECTION Y

SHEET TITLE

GROUND FLOOR

SHEET NO. : 06A

SCALE : 1 :100

PROJECT HOSTEL WORKING DRW

DRAWN BY
YASH VARDHAN

UID-SOA

WINDOW SCHEDULE			
S.No.	Sill	Lintel	Width
W1	600	2300	1235
W2	600	2600	550
W3	600	2300	3000
W4	600	2300	1800
W5	600	2300	1400
W6	350	2600	2400
W7	00	2250	4040
W8	450	2600	2400

NOTES



ALL DIMENSIONS ARE IN MM
ALL DIMENSIONS TO BE READ NOT MEASURED

DOOR SCHEDULE			
S.No.	Sill	Lintel	Width
D1	0	2250	1000
D2	0	2250	850
D3	0	2250	1800
D4	0	2250	1800
D5	0	2250	3200

SHAFT SCHEDULE		
S.No.	Length	Breadth
S1	450	4500
S2	1385	1000

LEGENDS

KEY PLAN

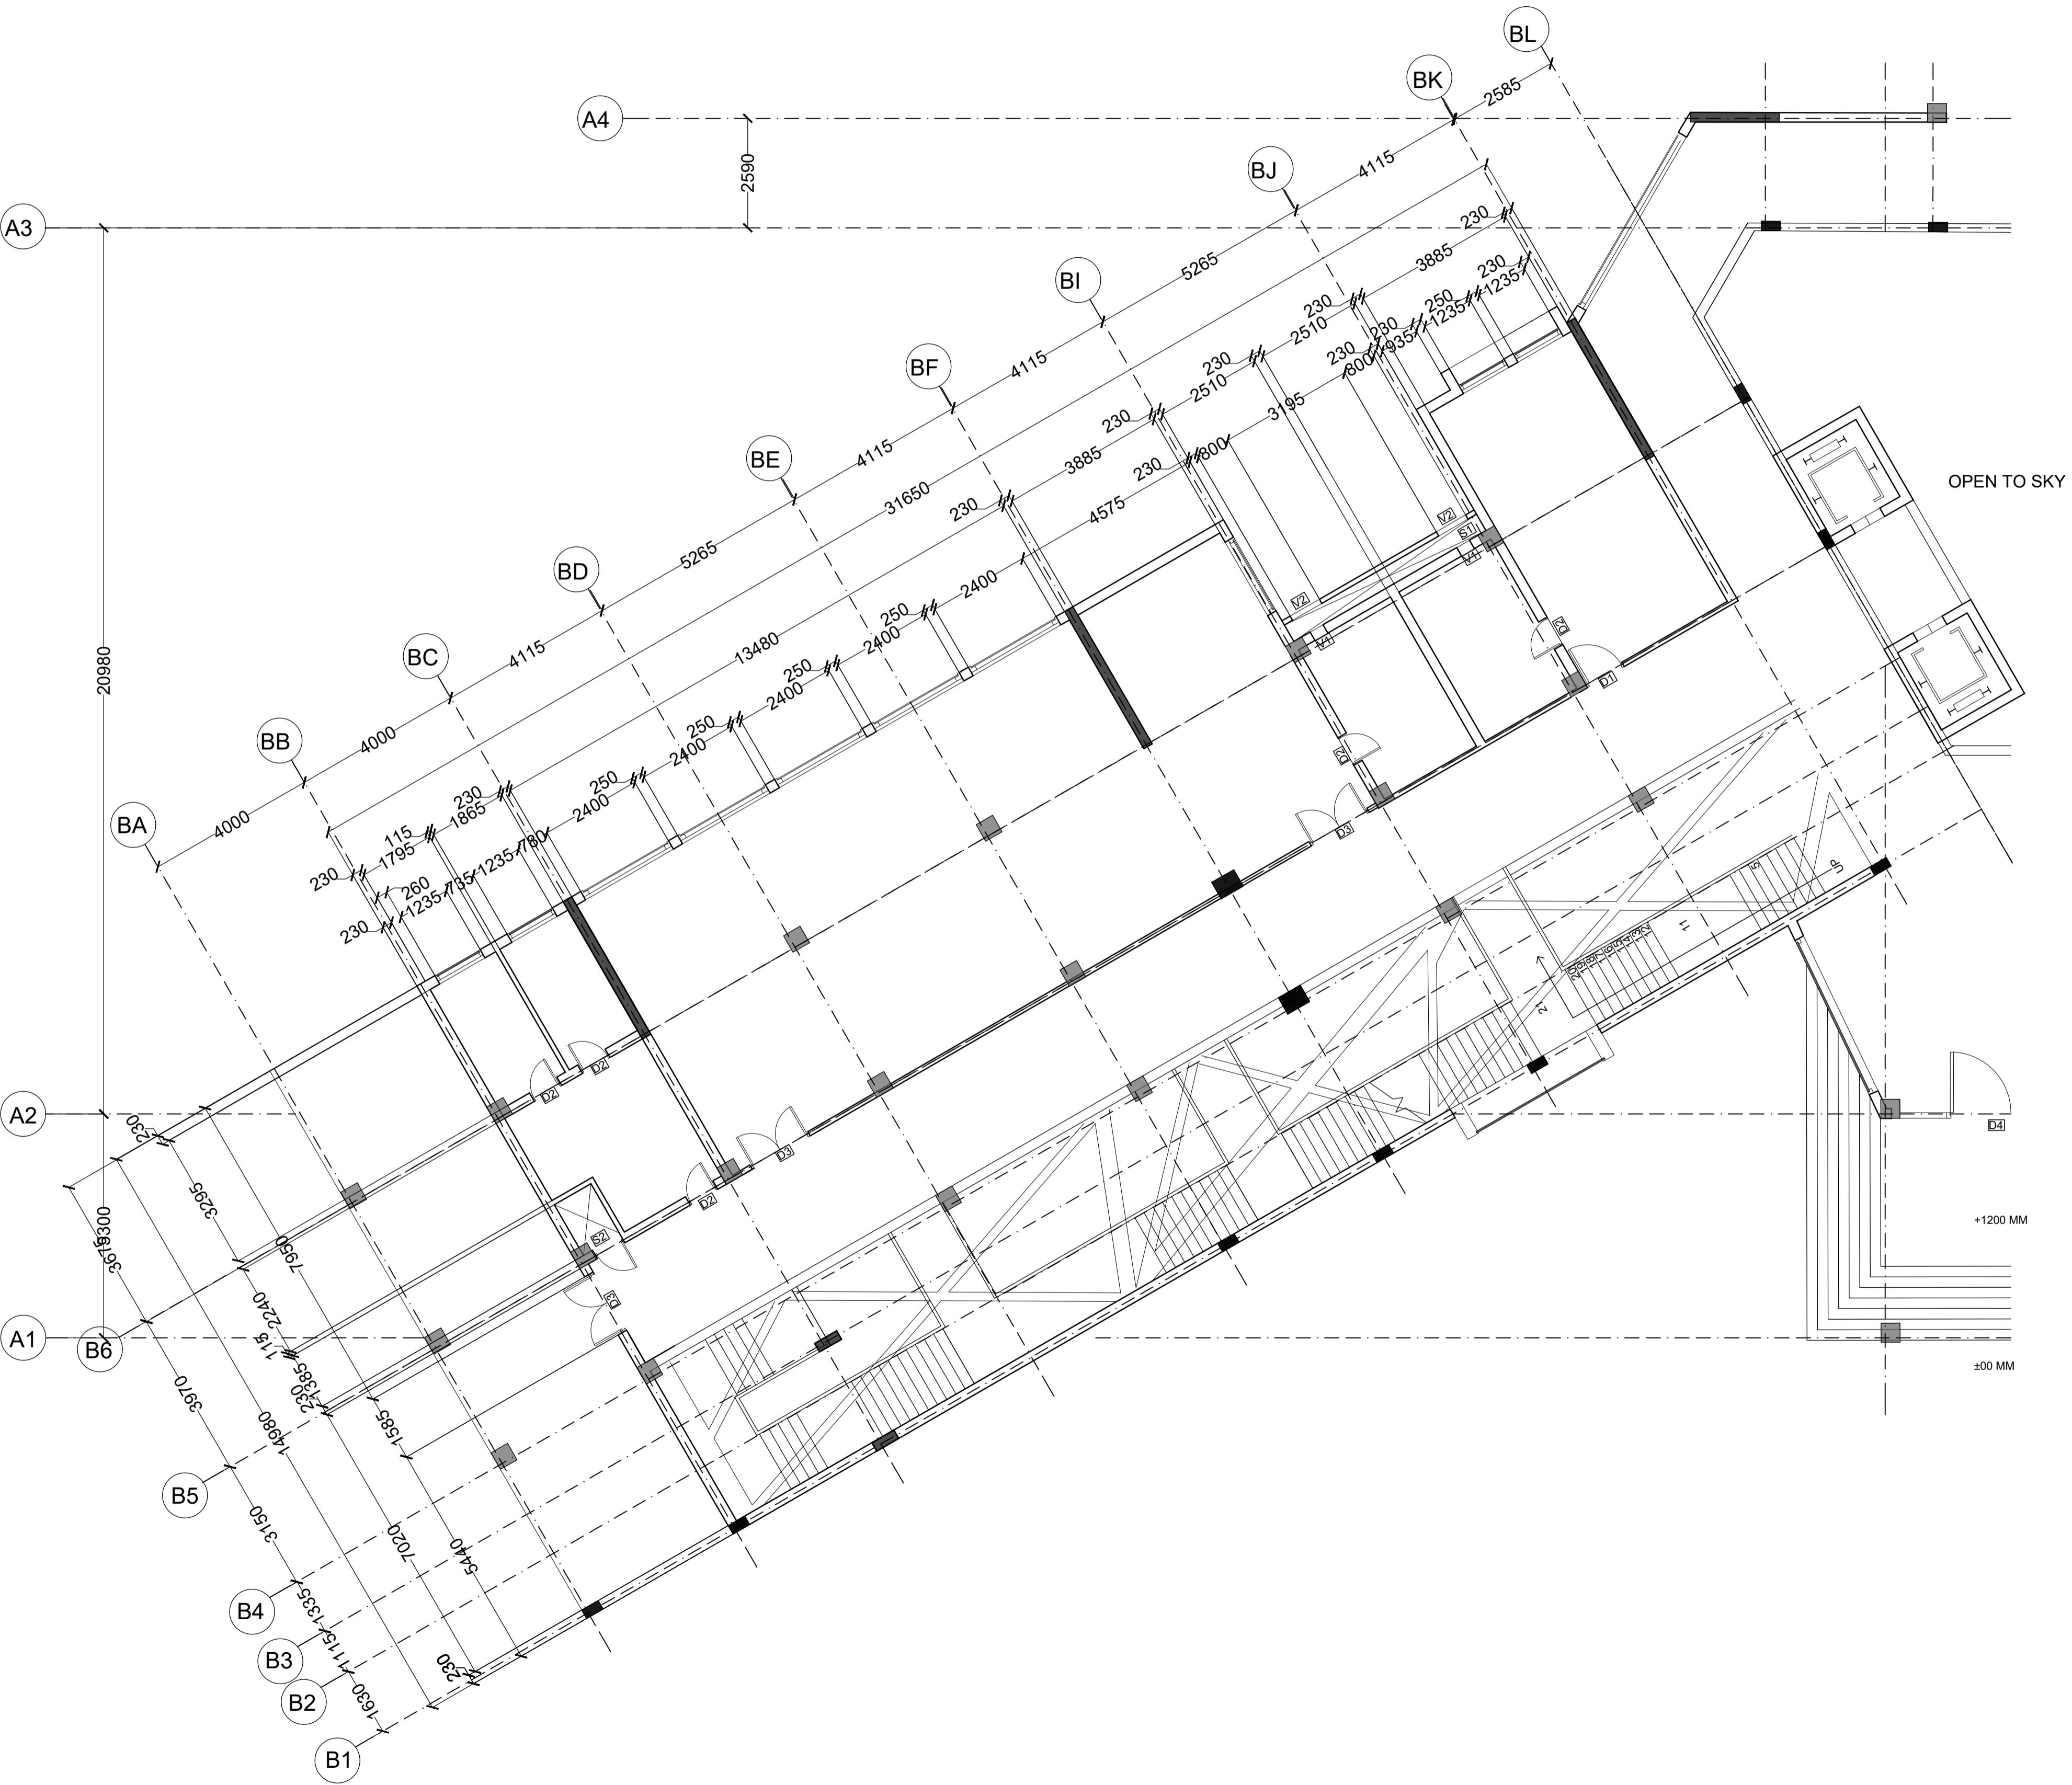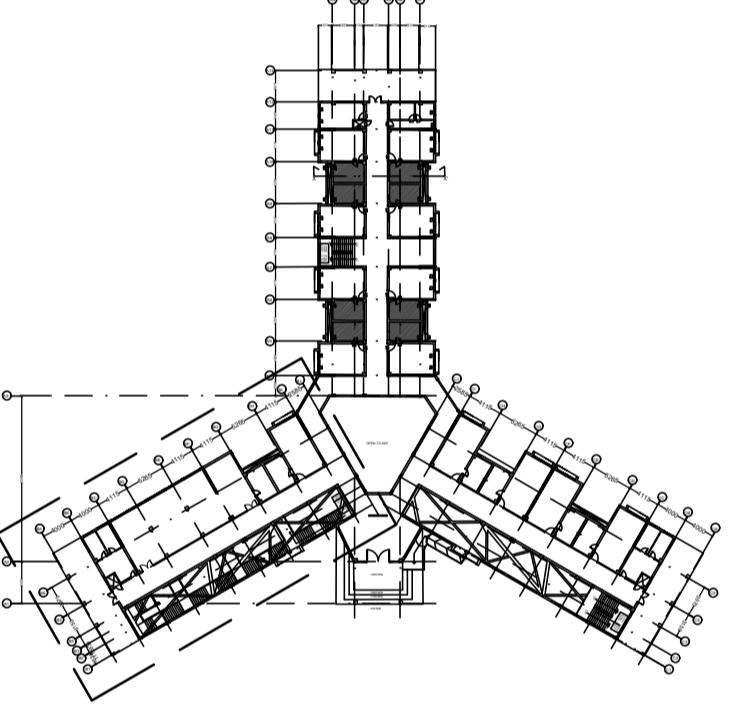

SHEET TITLE

GROUND FLOOR

SHEET NO. : 06B

PROJECT HOSTEL WORKING DRW.

DRAWN BY	CHECKED BY
YASH VARDHAN	



UID-SOA

NOTES

ALL DIMENSIONS ARE IN MM
ALL DIMENSIONS TO BE READ NOT MEASURED

LEGENDS

KEY PLAN

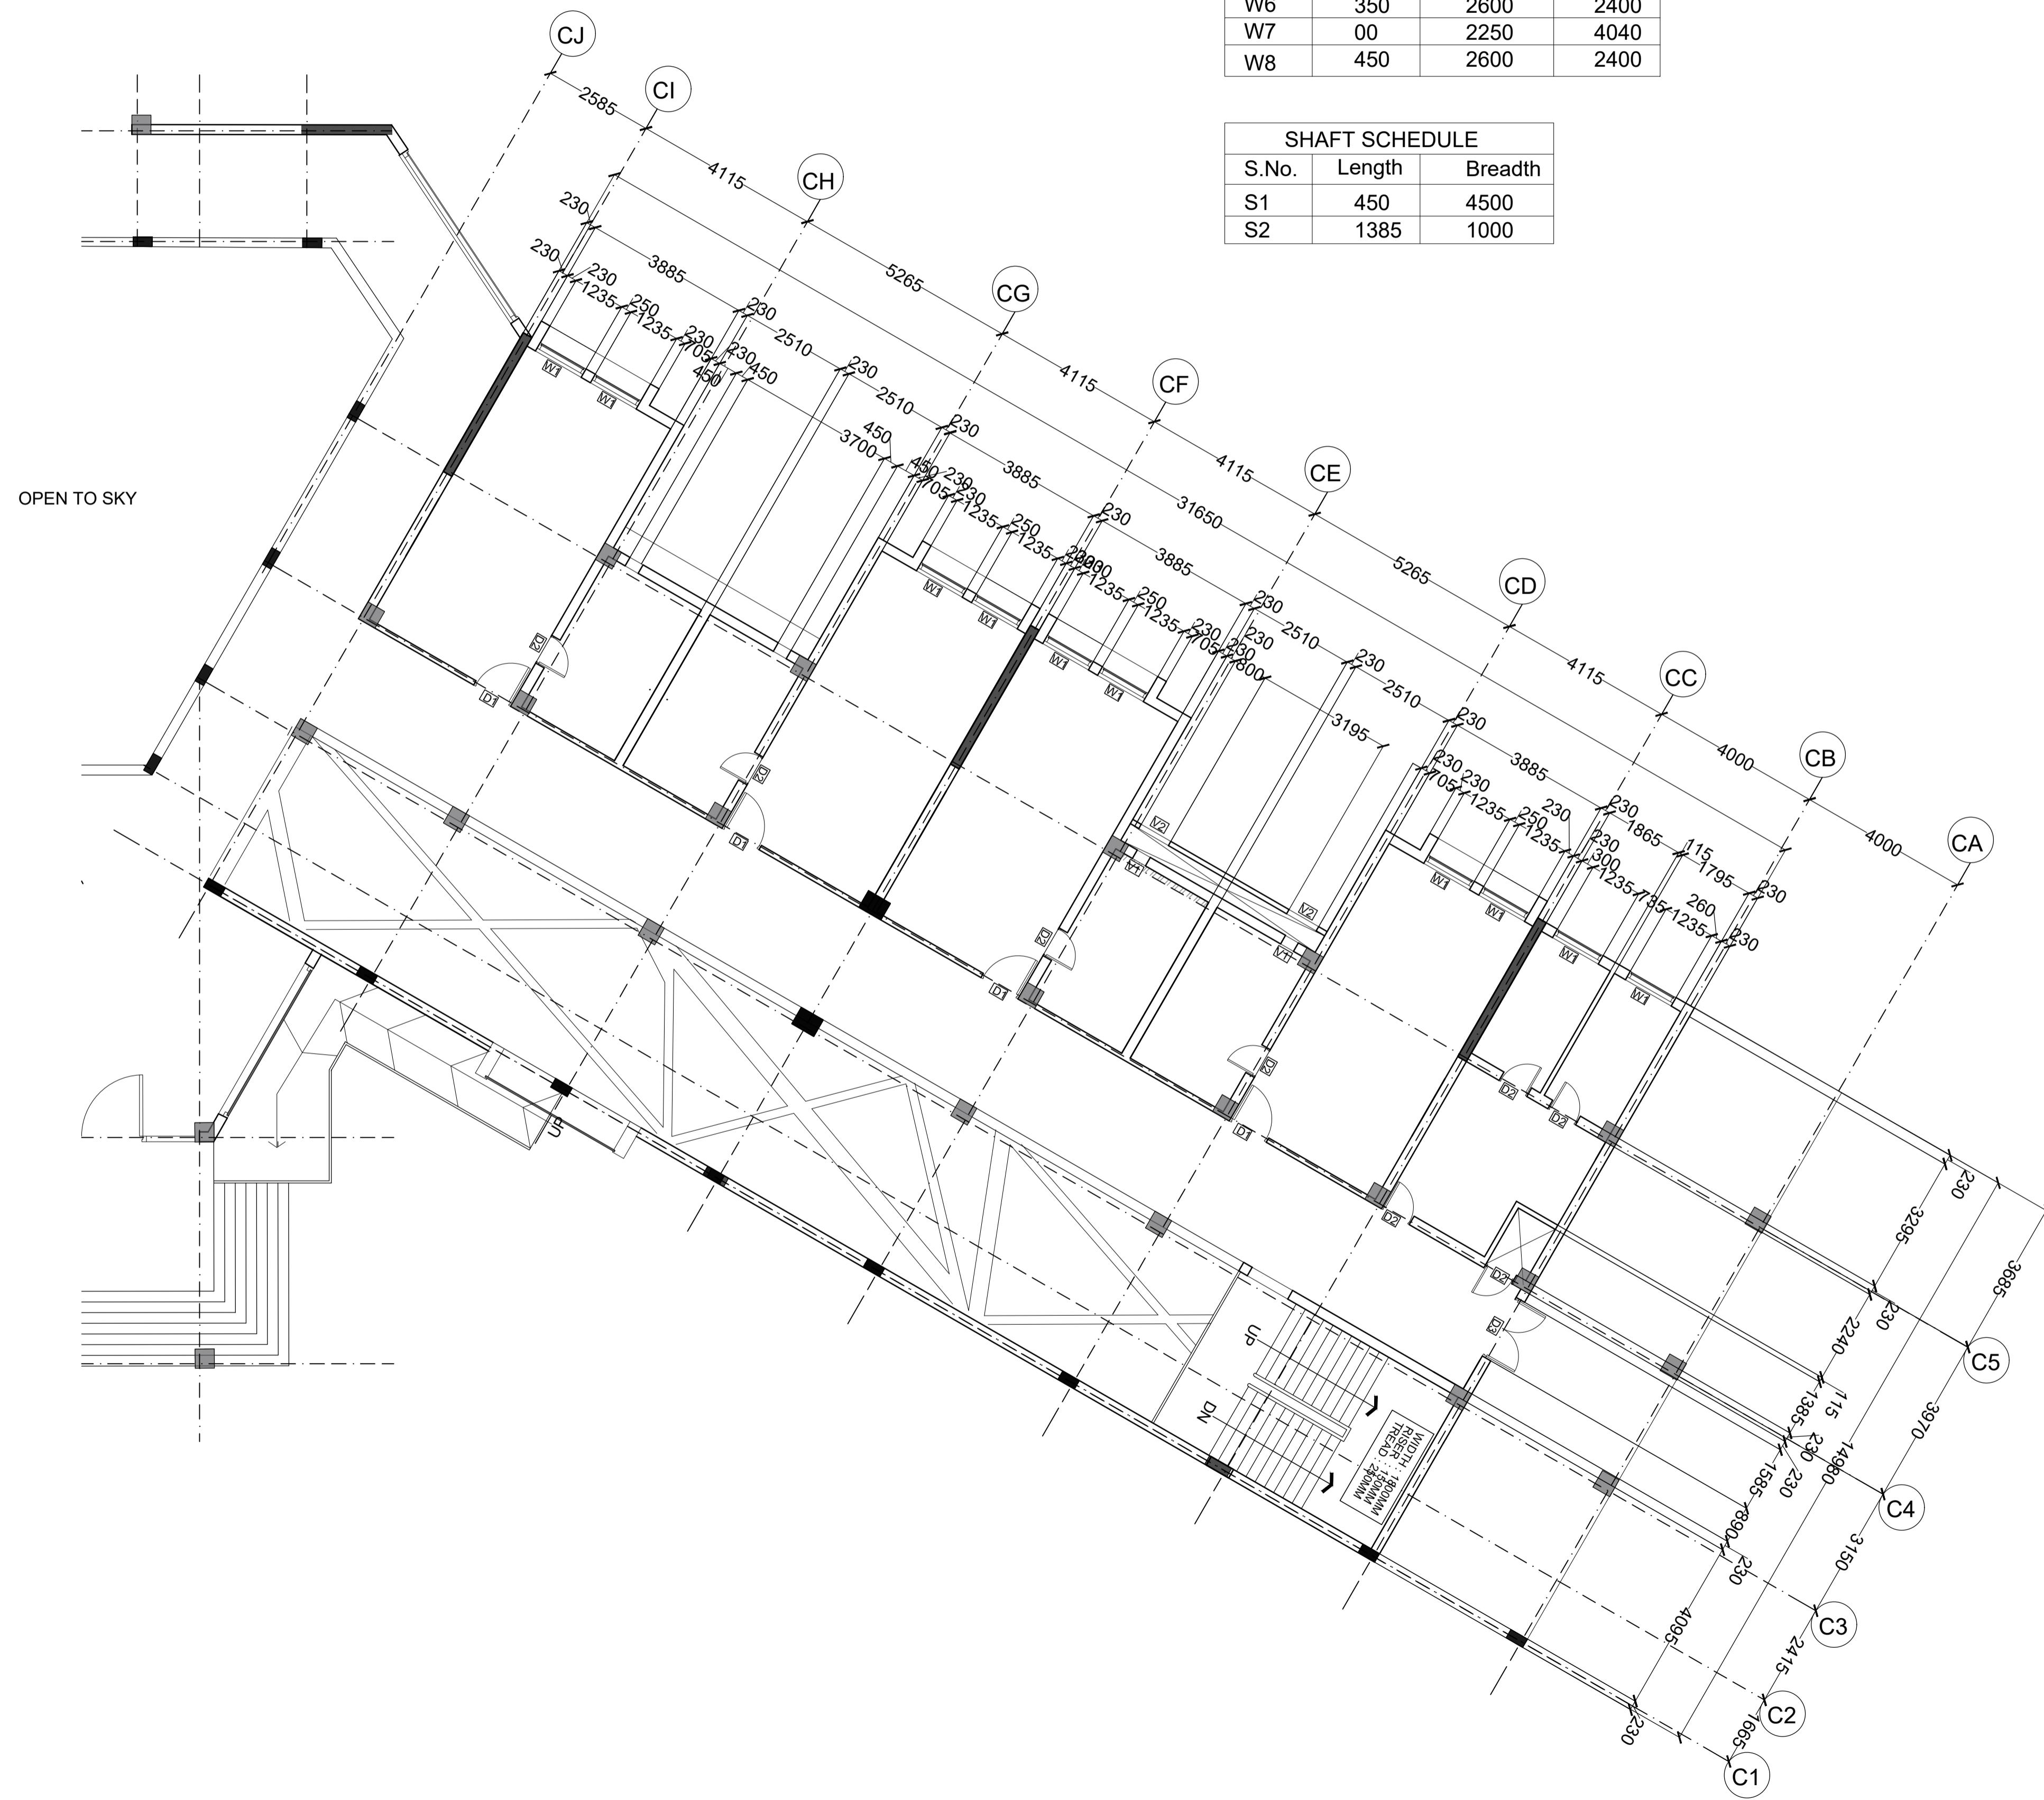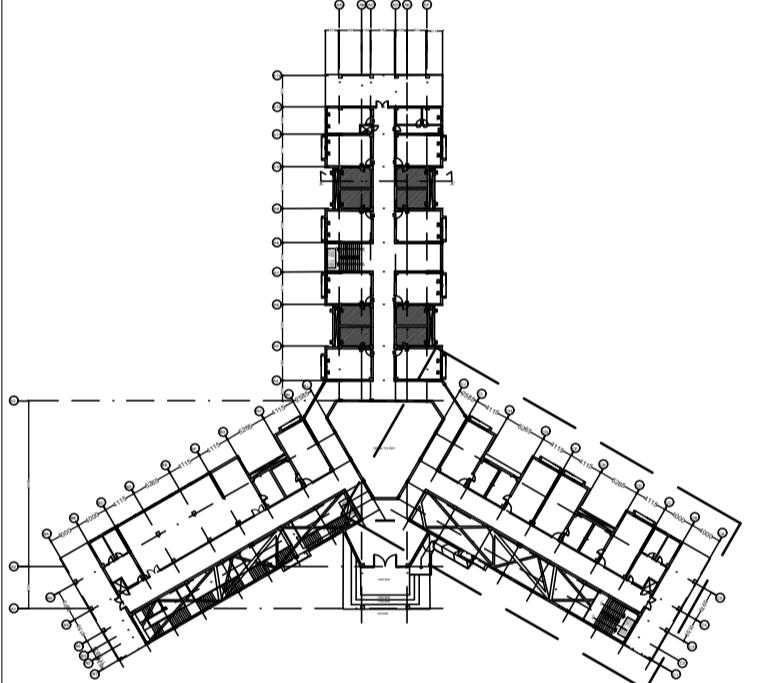



SHEET TITLE
GROUND FLOOR

SHEET NO. : 06C
SCALE : 1:100

PROJECT
HOSTEL WORKING DRW.

DRAWN BY YASH VARDHAN **CHECKED BY**

UID-SOA

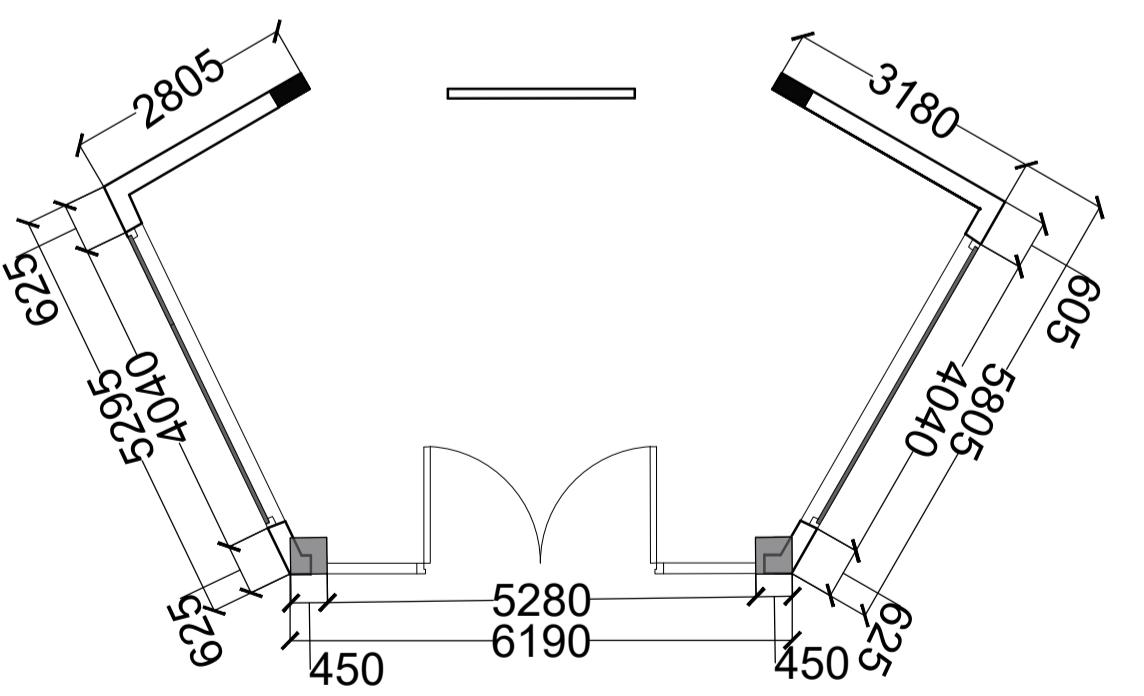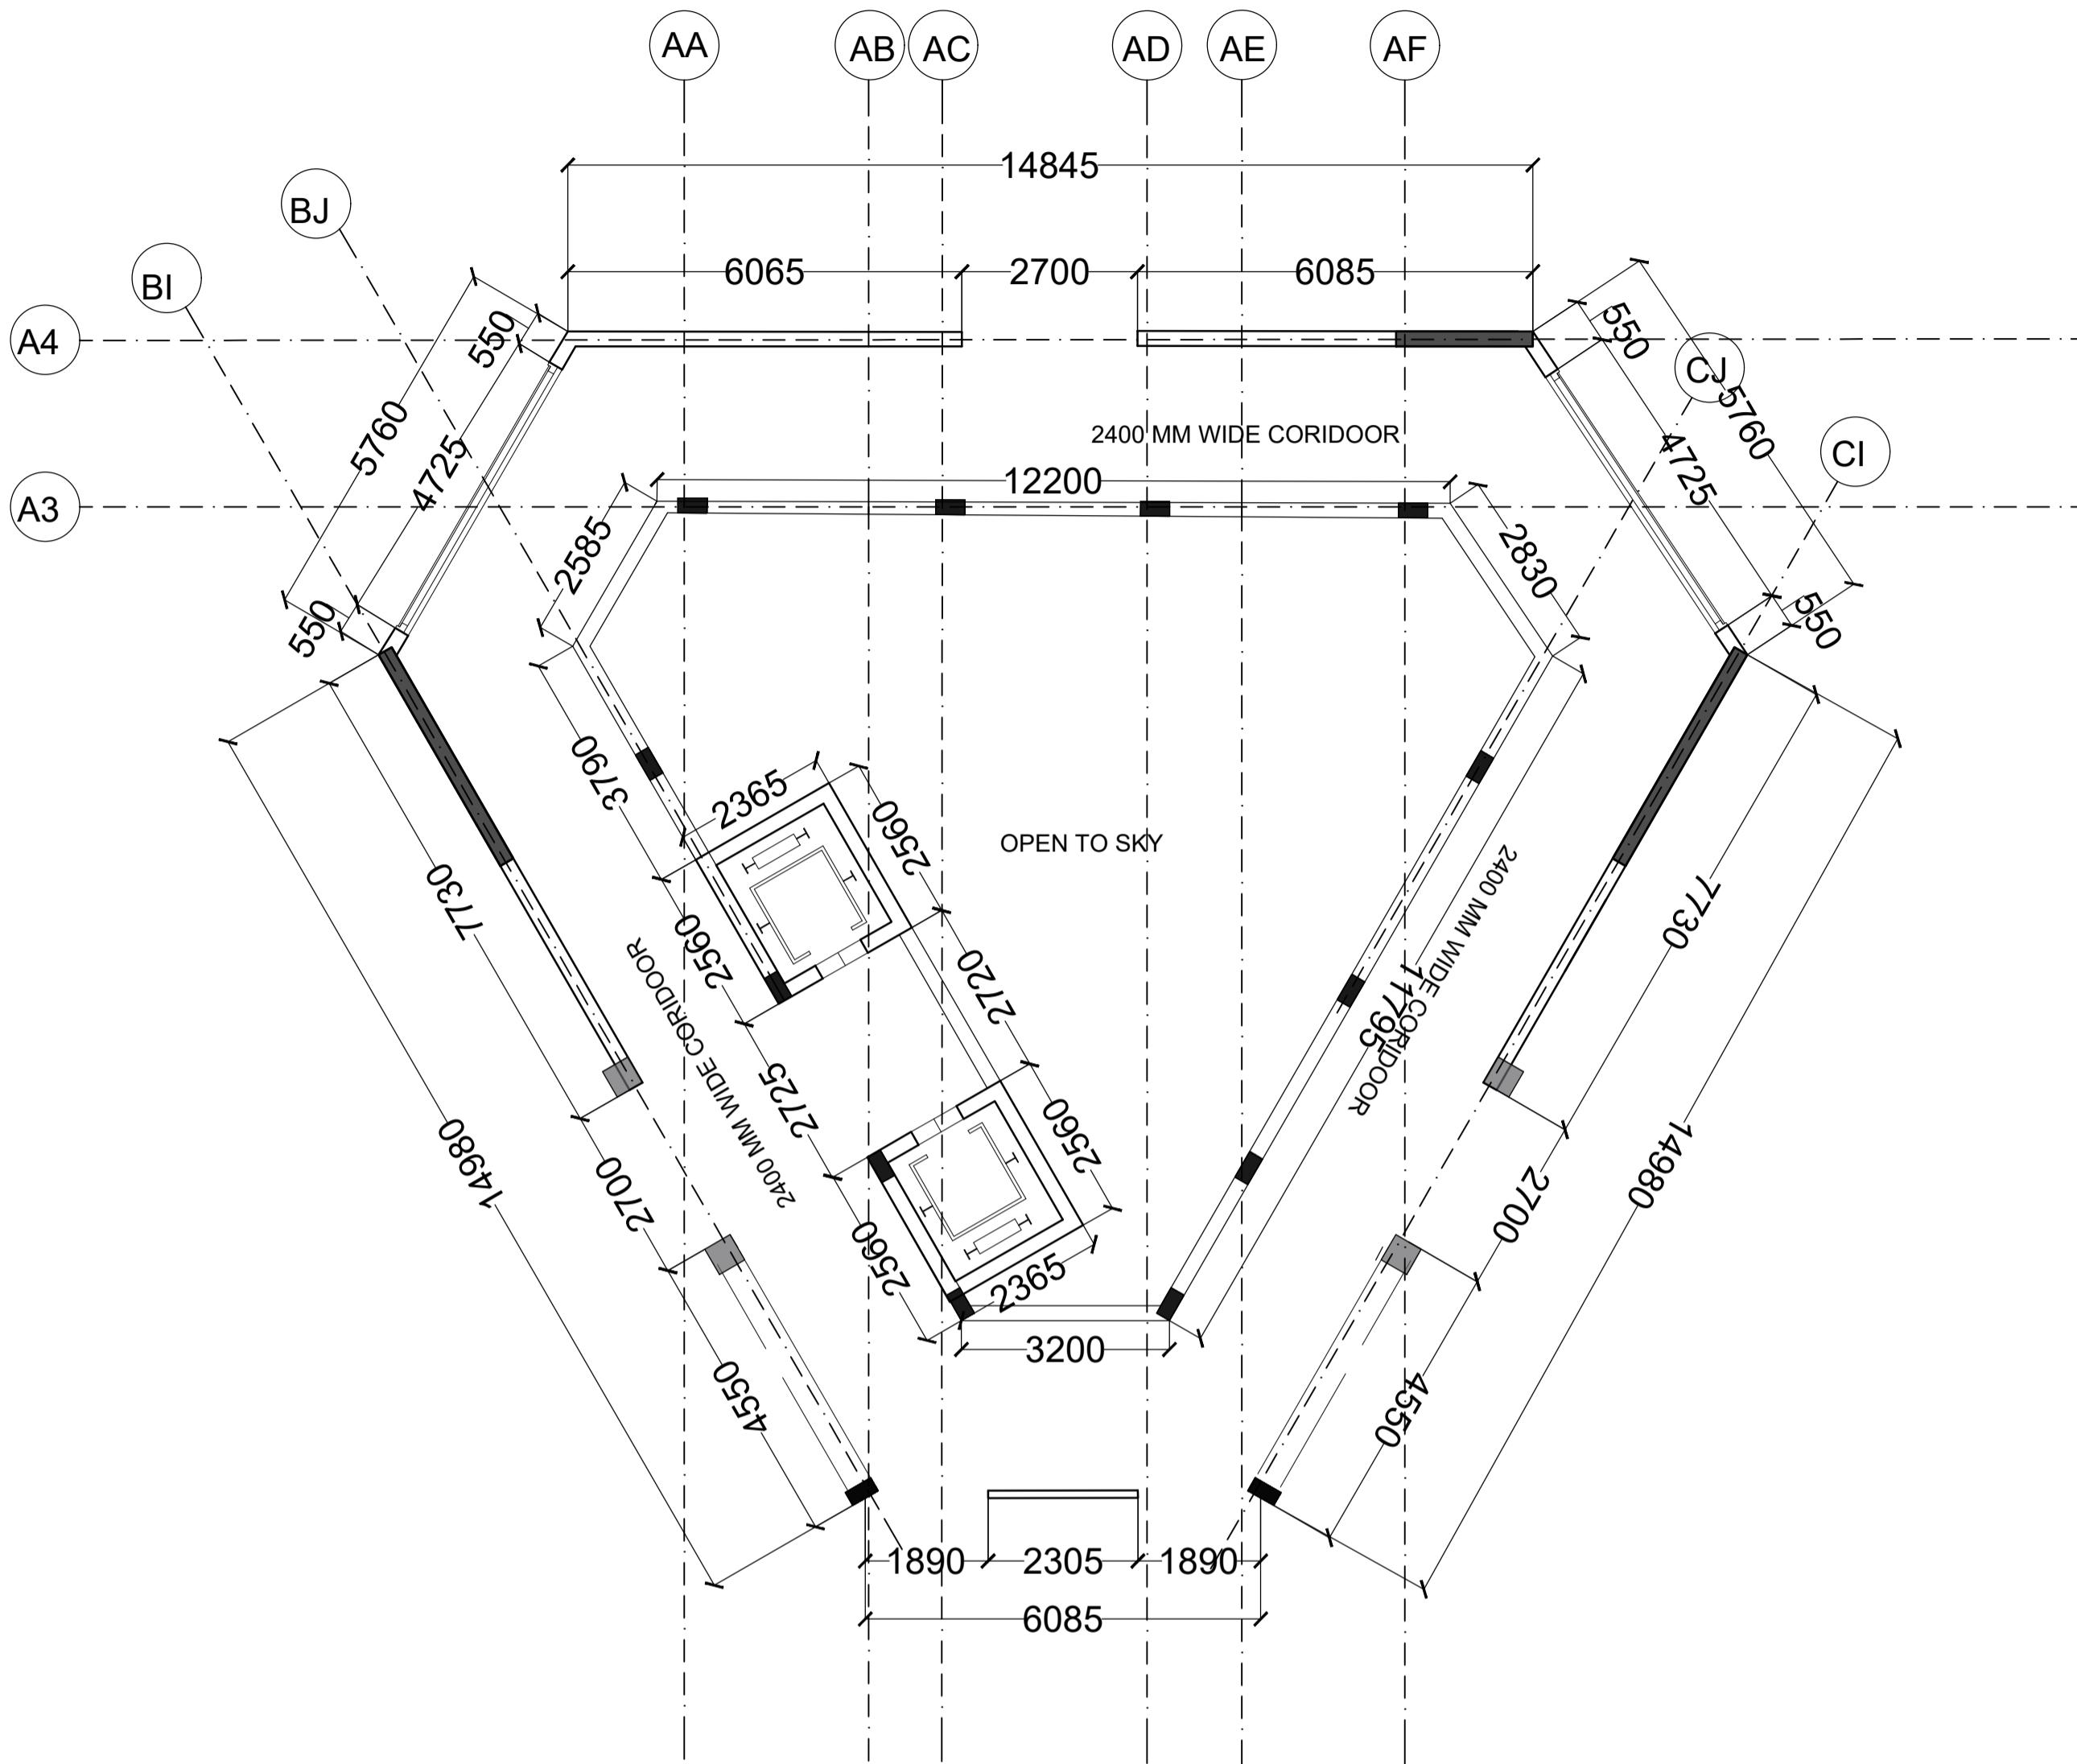


NOTES

ALL DIMENSIONS ARE IN MM
ALL DIMENSIONS TO BE READ NOT MEASURED

LEGENDS

KEY PLAN

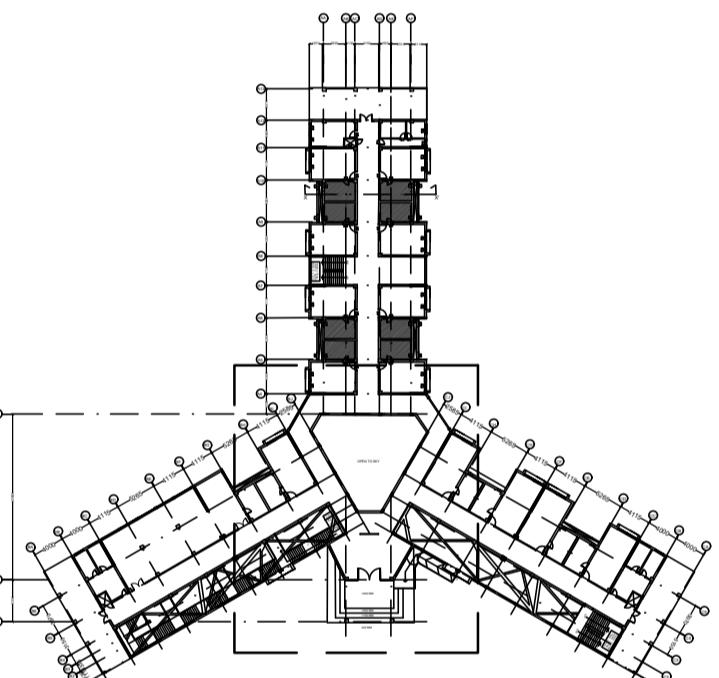

SHEET TITLE

GROUND FLOOR PLAN

SHEET NO. : 06D
SCALE : 1 :100

PROJECT HOSTEL WORKING DRW.

DRAWN BY	CHECKED BY
YASH VARDHAN	

UID-SOA

NOTES

ALL DIMENSIONS ARE IN MM
ALL DIMENSIONS TO BE READ NOT MEASURED

LEGENDS

KEY PLAN

SHEET TITLE


FIRST FLOOR PLAN

SHEET NO. : 07

SCALE : 1 :150

PROJECT HOSTEL WORKING DRW

DRAWN BY	CHECKED BY
YASH VARDHAN	

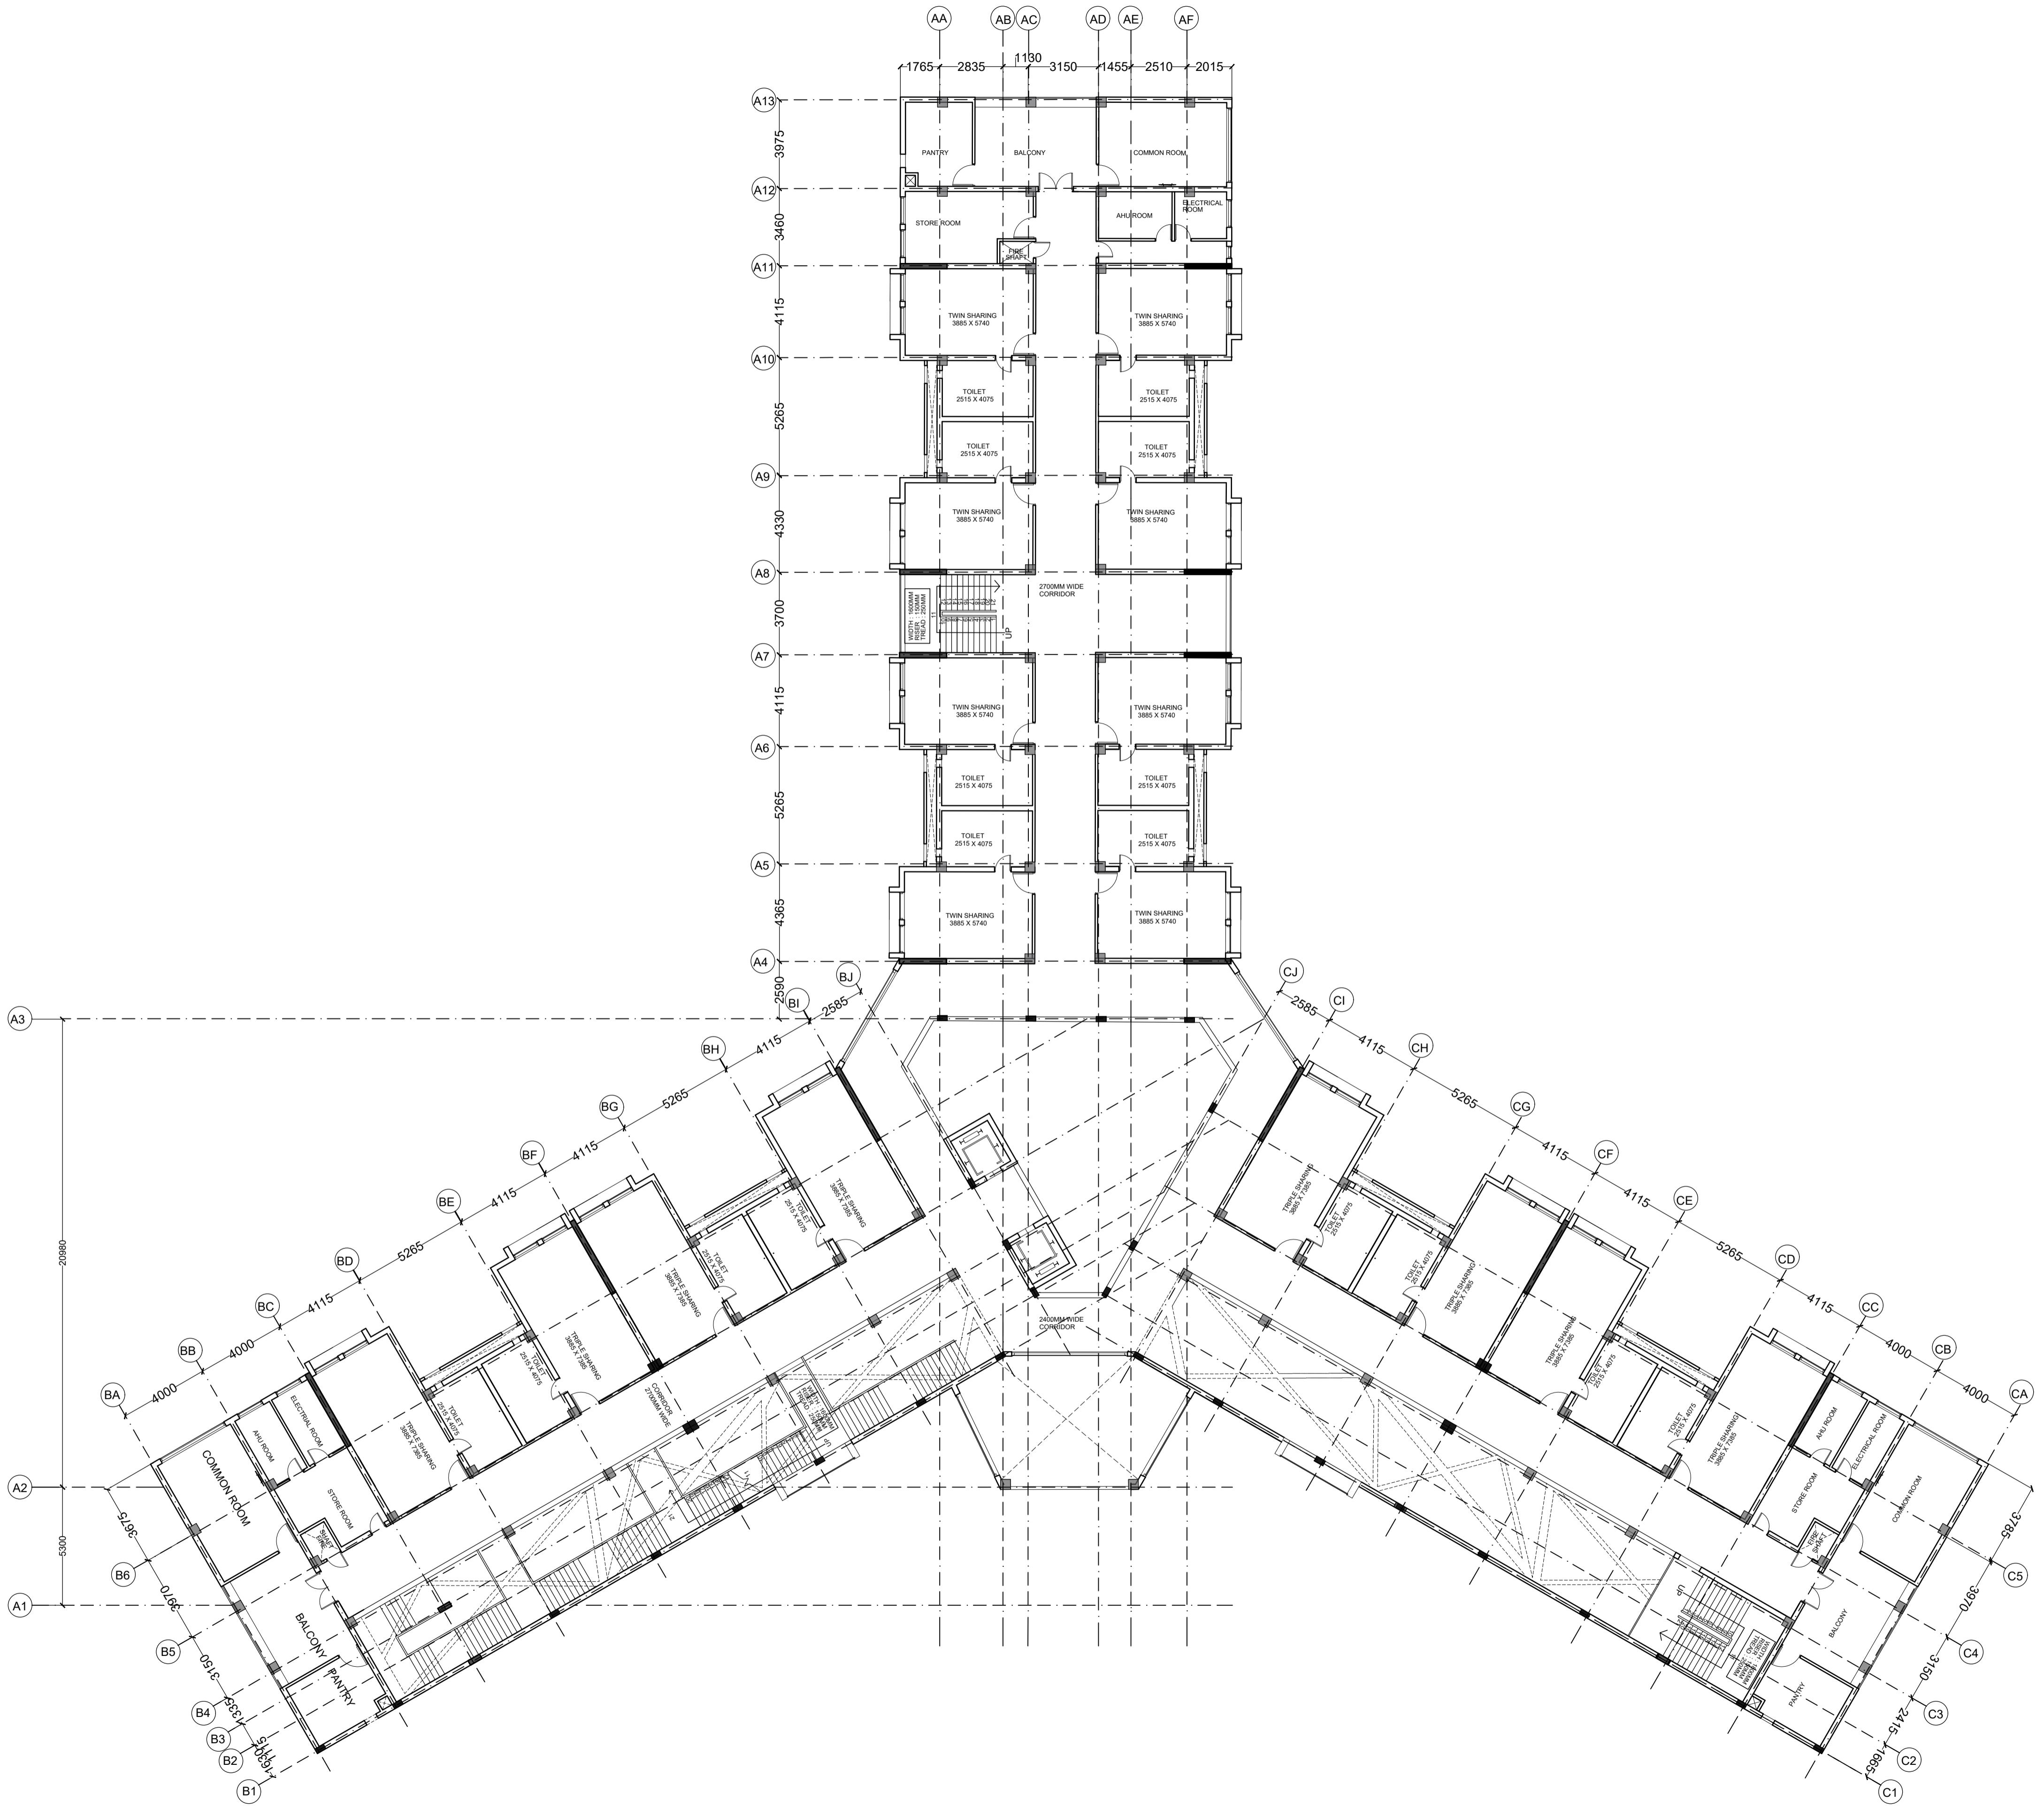

UID-SOA

NOTES

ALL DIMENSIONS ARE IN MM
ALL DIMENSIONS TO BE READ NOT MEASURED

LEGENDS

KEY PLAN

SHEET TITLE
SECOND FLOOR PLAN


SHEET NO.: 08
SCALE : 1:150



PROJECT
HOSTEL WORKING DRW.

DRAWN BY
YASH VARDHAN

CHECKED BY

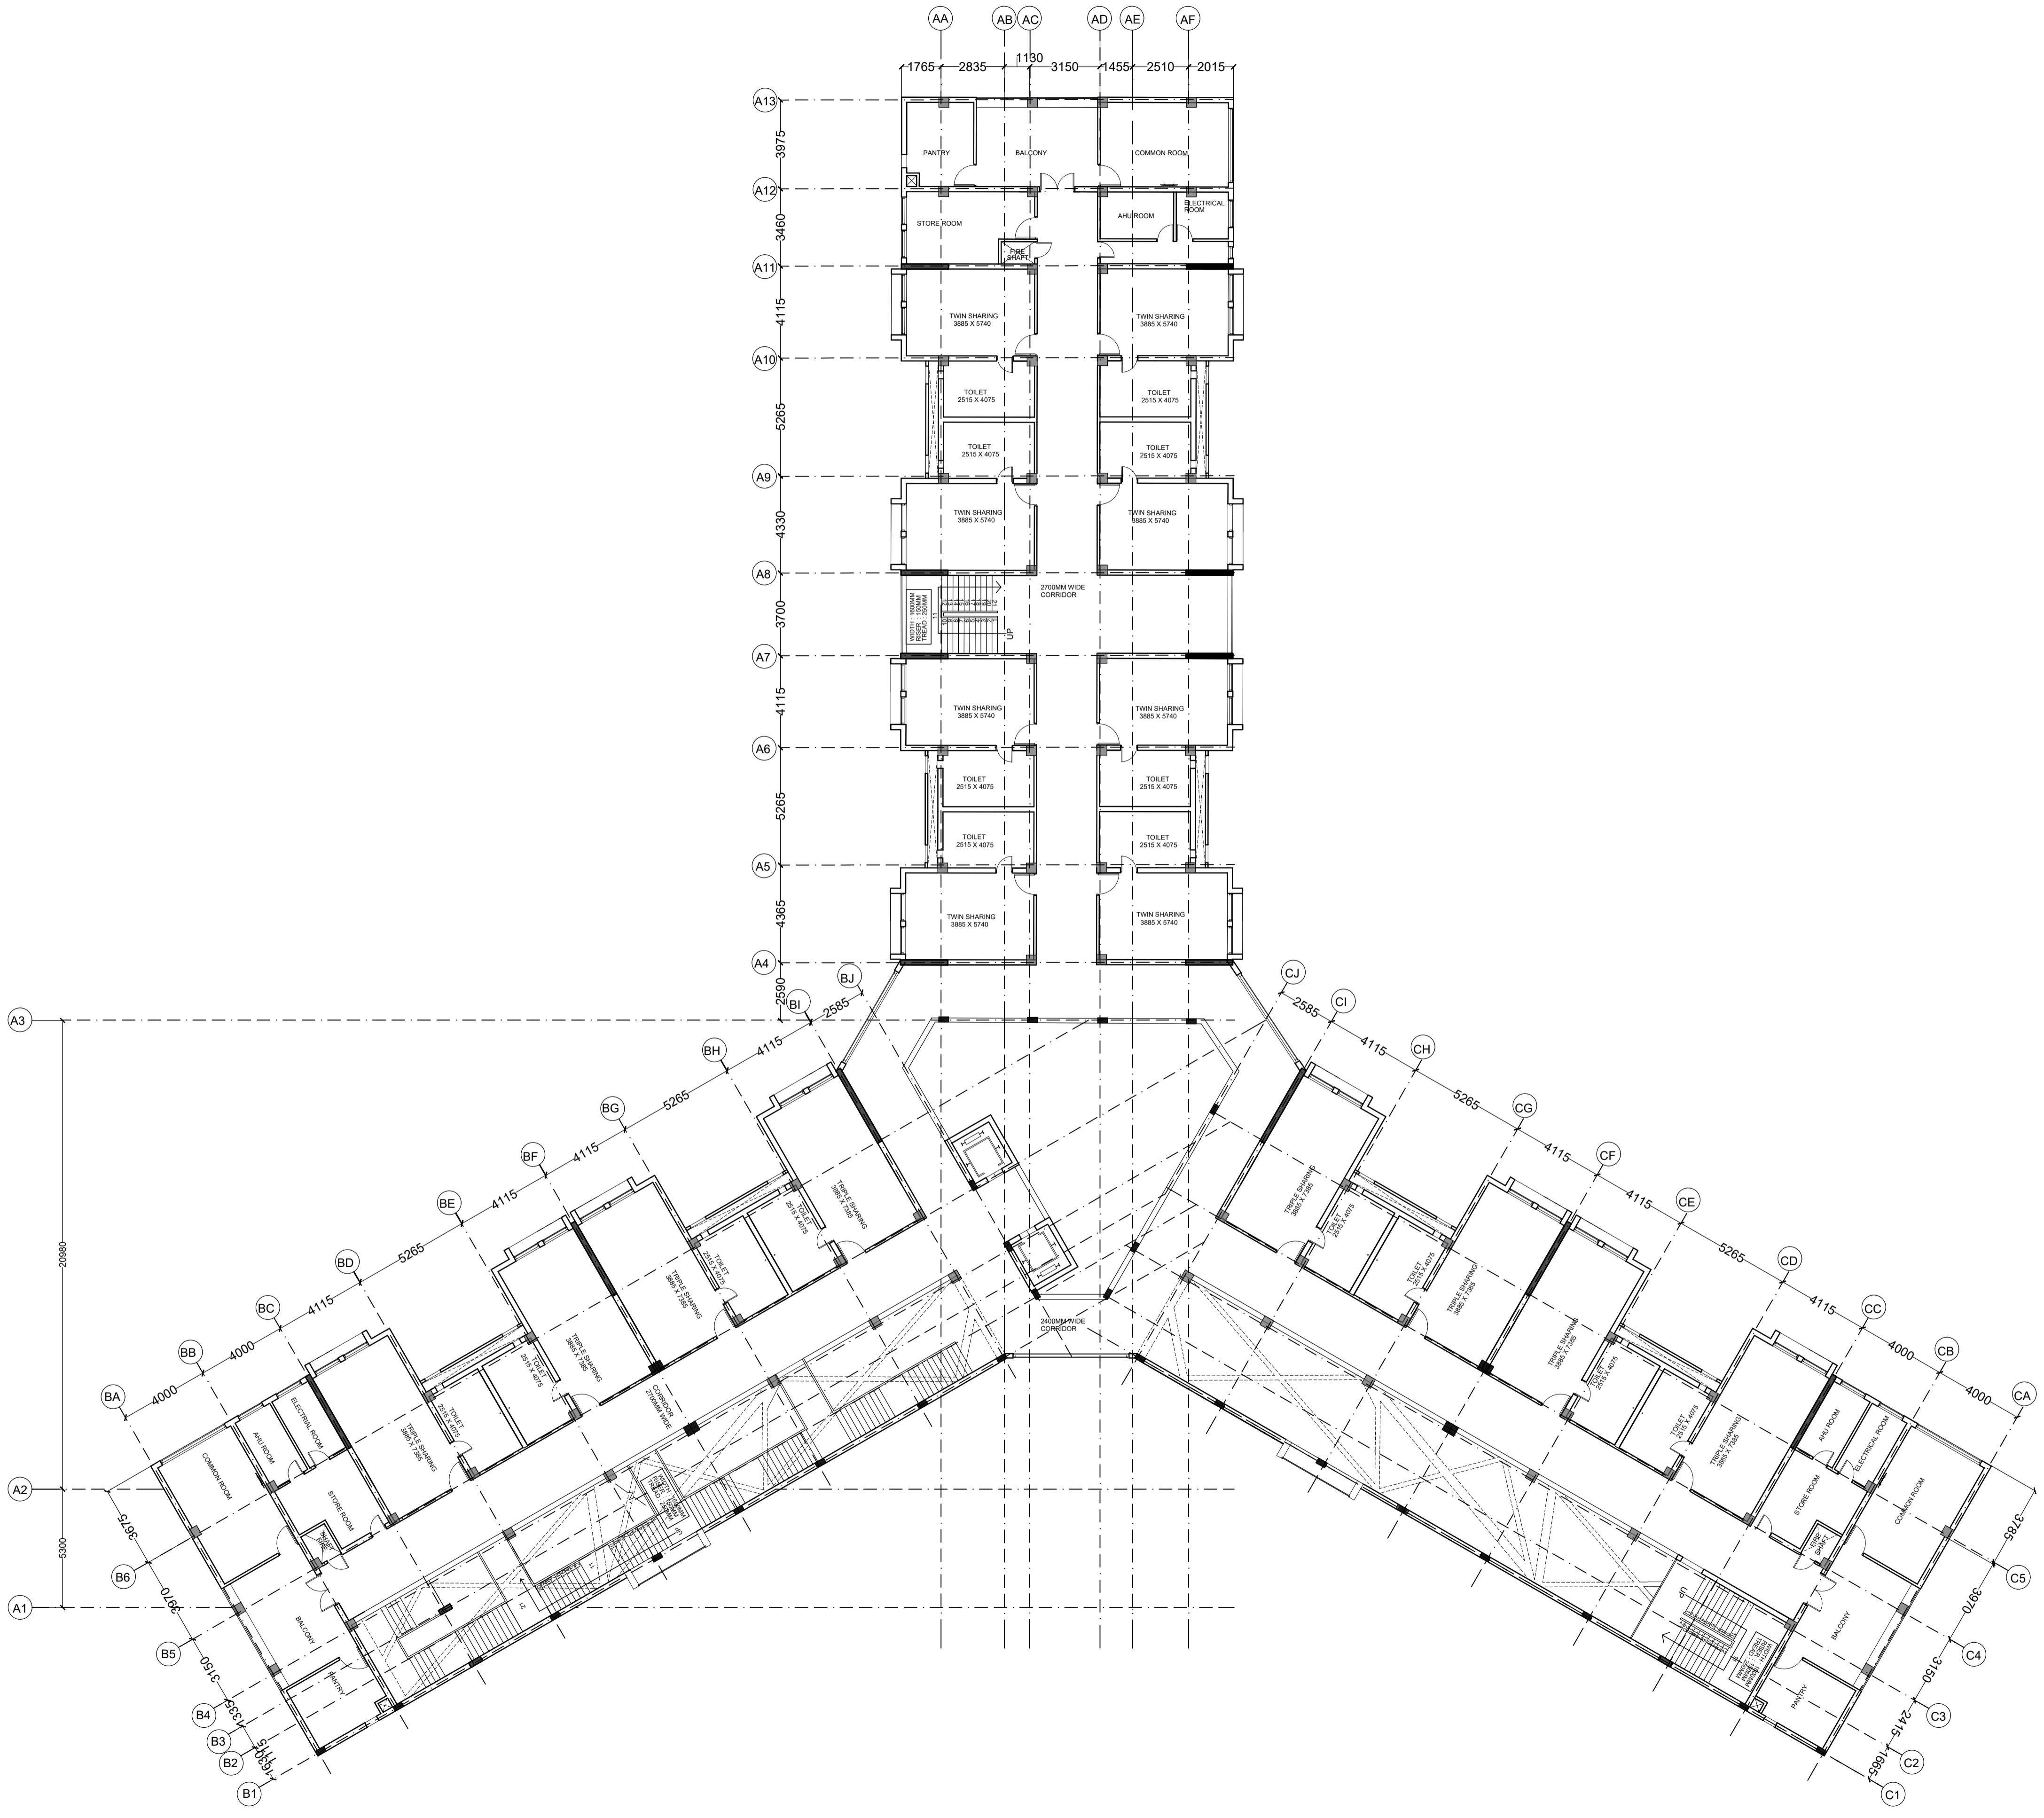

UID-SOA

NOTES

ALL DIMENSIONS ARE IN MM
ALL DIMENSIONS TO BE READ NOT MEASURED

LEGENDS

KEY PLAN


SHEET TITLE

THIRD FLOOR PLAN

SHEET NO. : 09
SCALE : 1 :150

PROJECT HOSTEL WORKING DRW.

DRAWN BY	CHECKED BY
YASH VARDHAN	

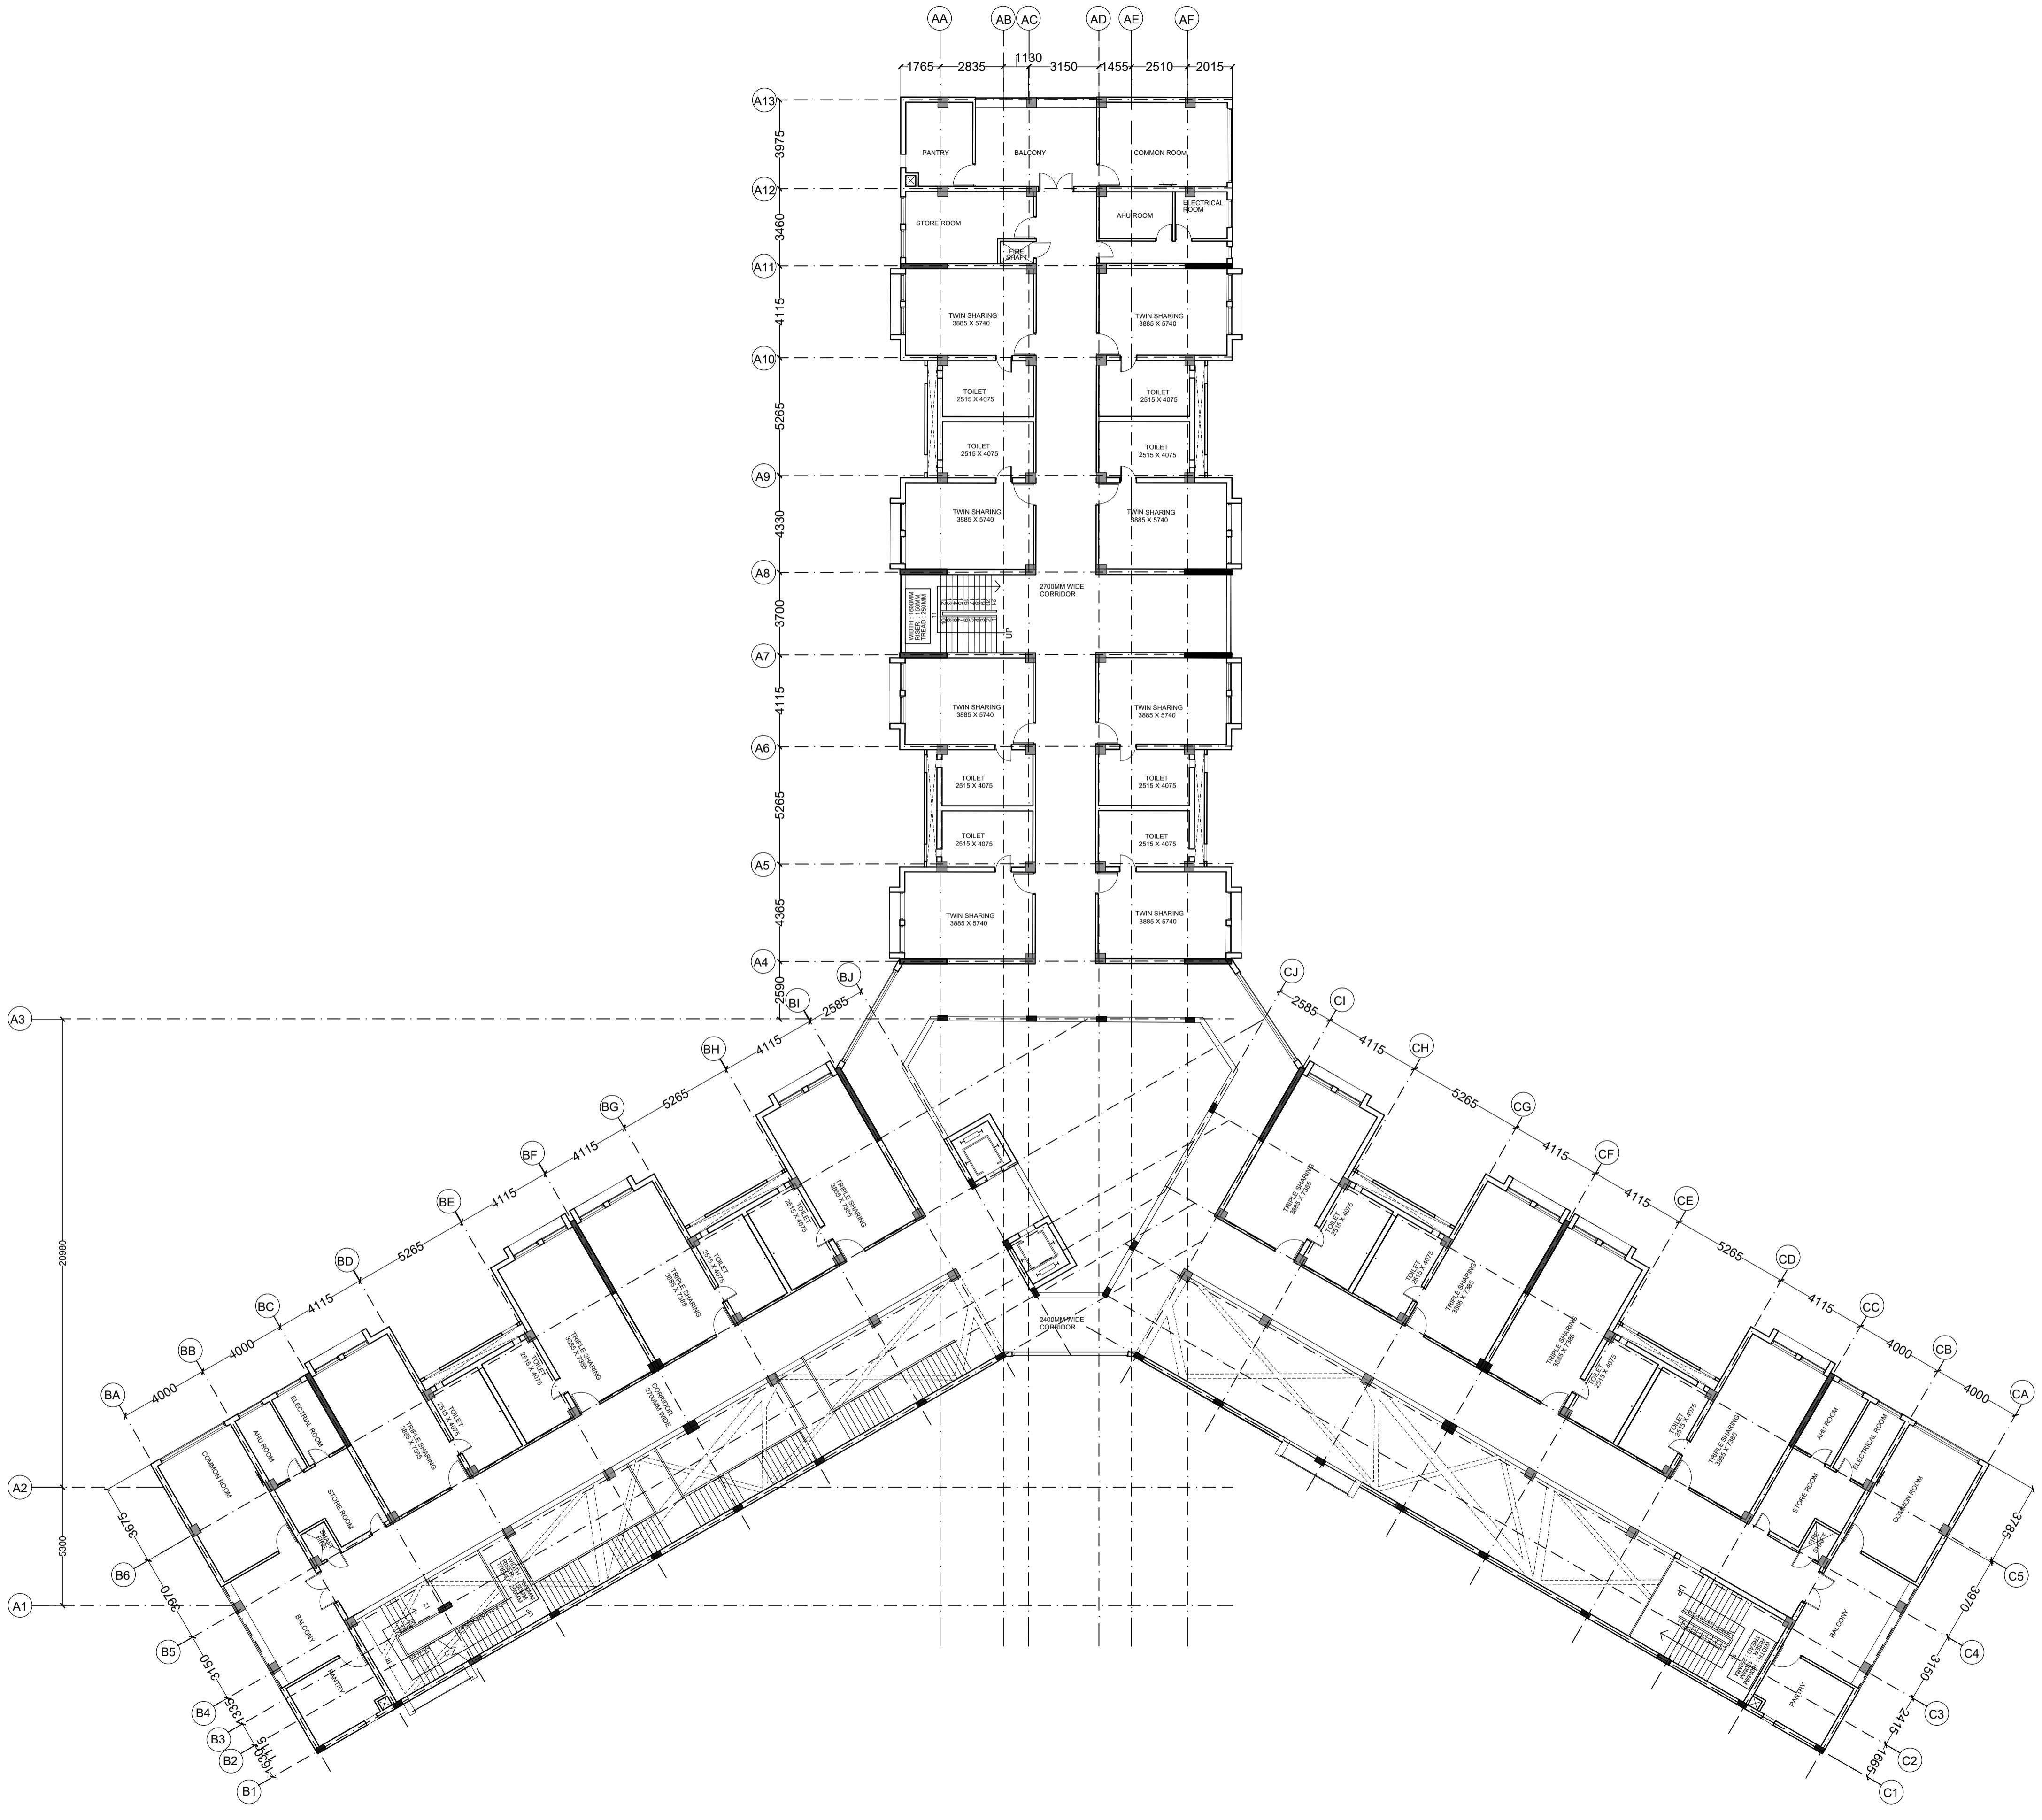

UID-SOA

NOTES

ALL DIMENSIONS ARE IN MM
ALL DIMENSIONS TO BE READ NOT MEASURED

LEGENDS

KEY PLAN


SHEET TITLE

FOURTH FLOOR PLAN

SHEET NO. : 10
SCALE : 1 : 150

PROJECT HOSTEL WORKING DRW.

DRAWN BY	CHECKED BY
YASH VARDHAN	

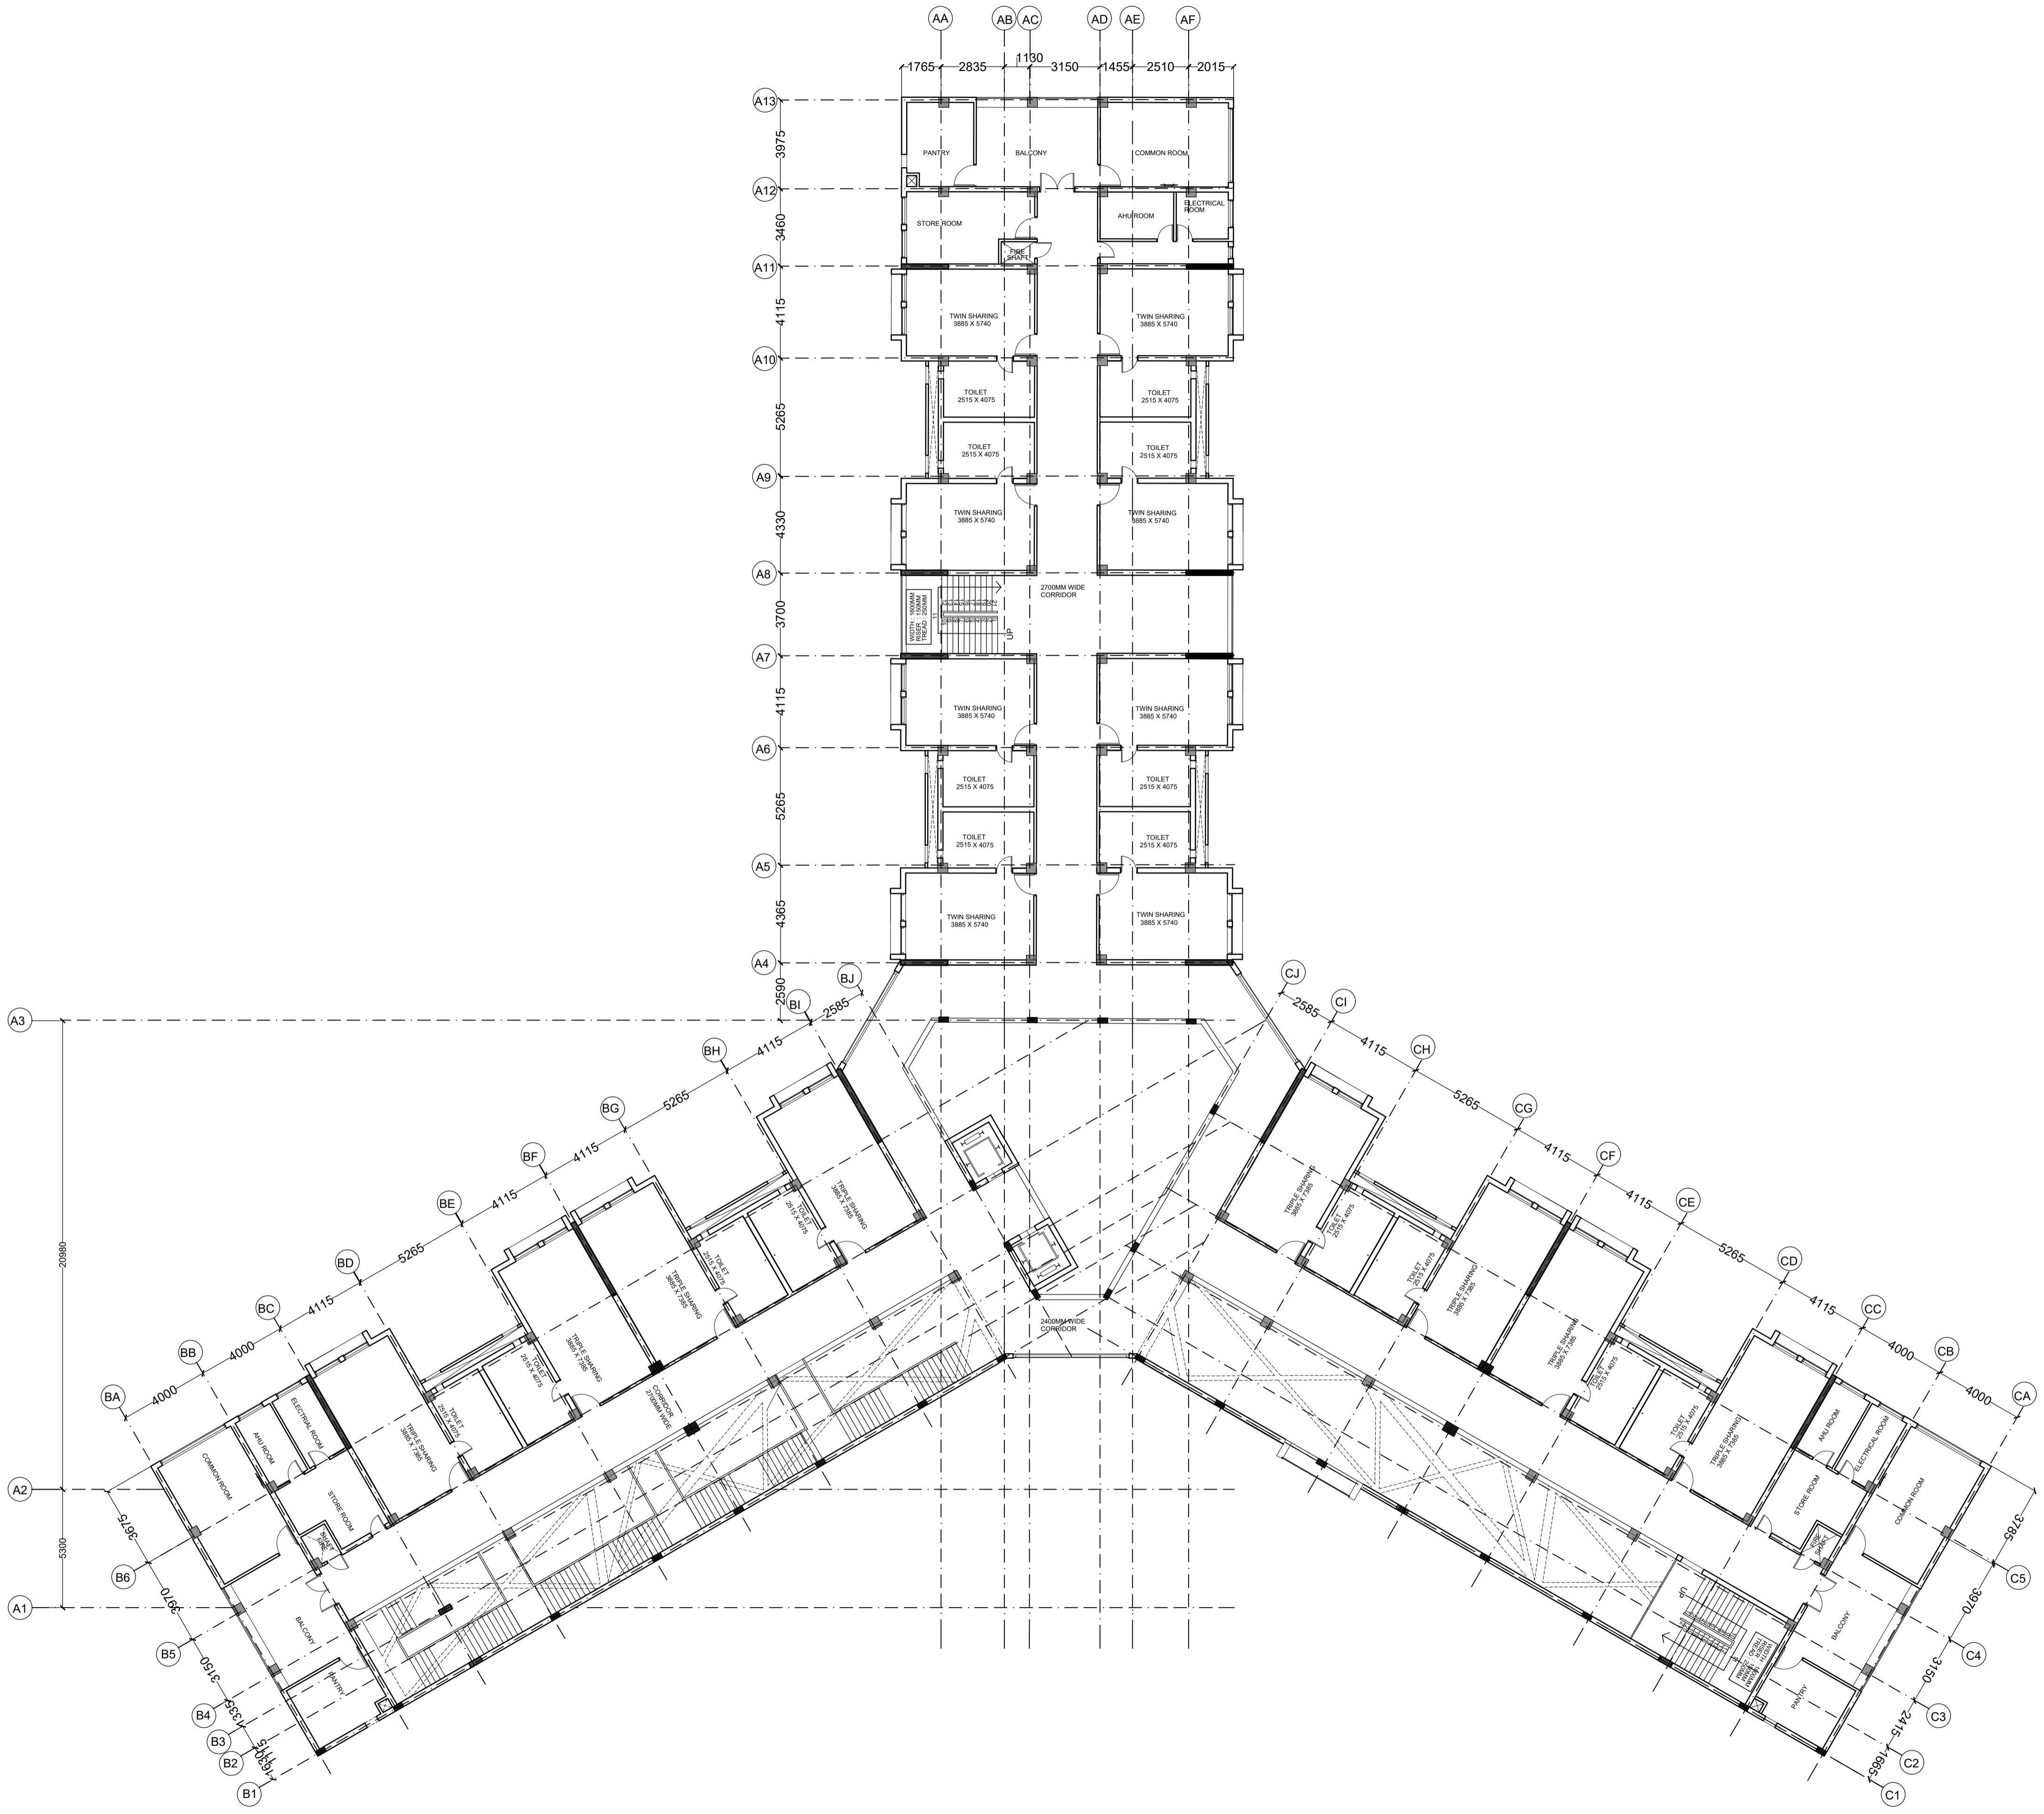

UID-SOA

NOTES

ALL DIMENSIONS ARE IN MM
ALL DIMENSIONS TO BE READ NOT MEASURED

LEGENDS

KEY PLAN

SHEET TITLE


TERRACE FLOOR PLAN

SHEET NO. : 11

SCALE : 1 :150

PROJECT HOSTEL WORKING DRW


DRAWN BY	CHECKED BY
YASH VARDHAN	

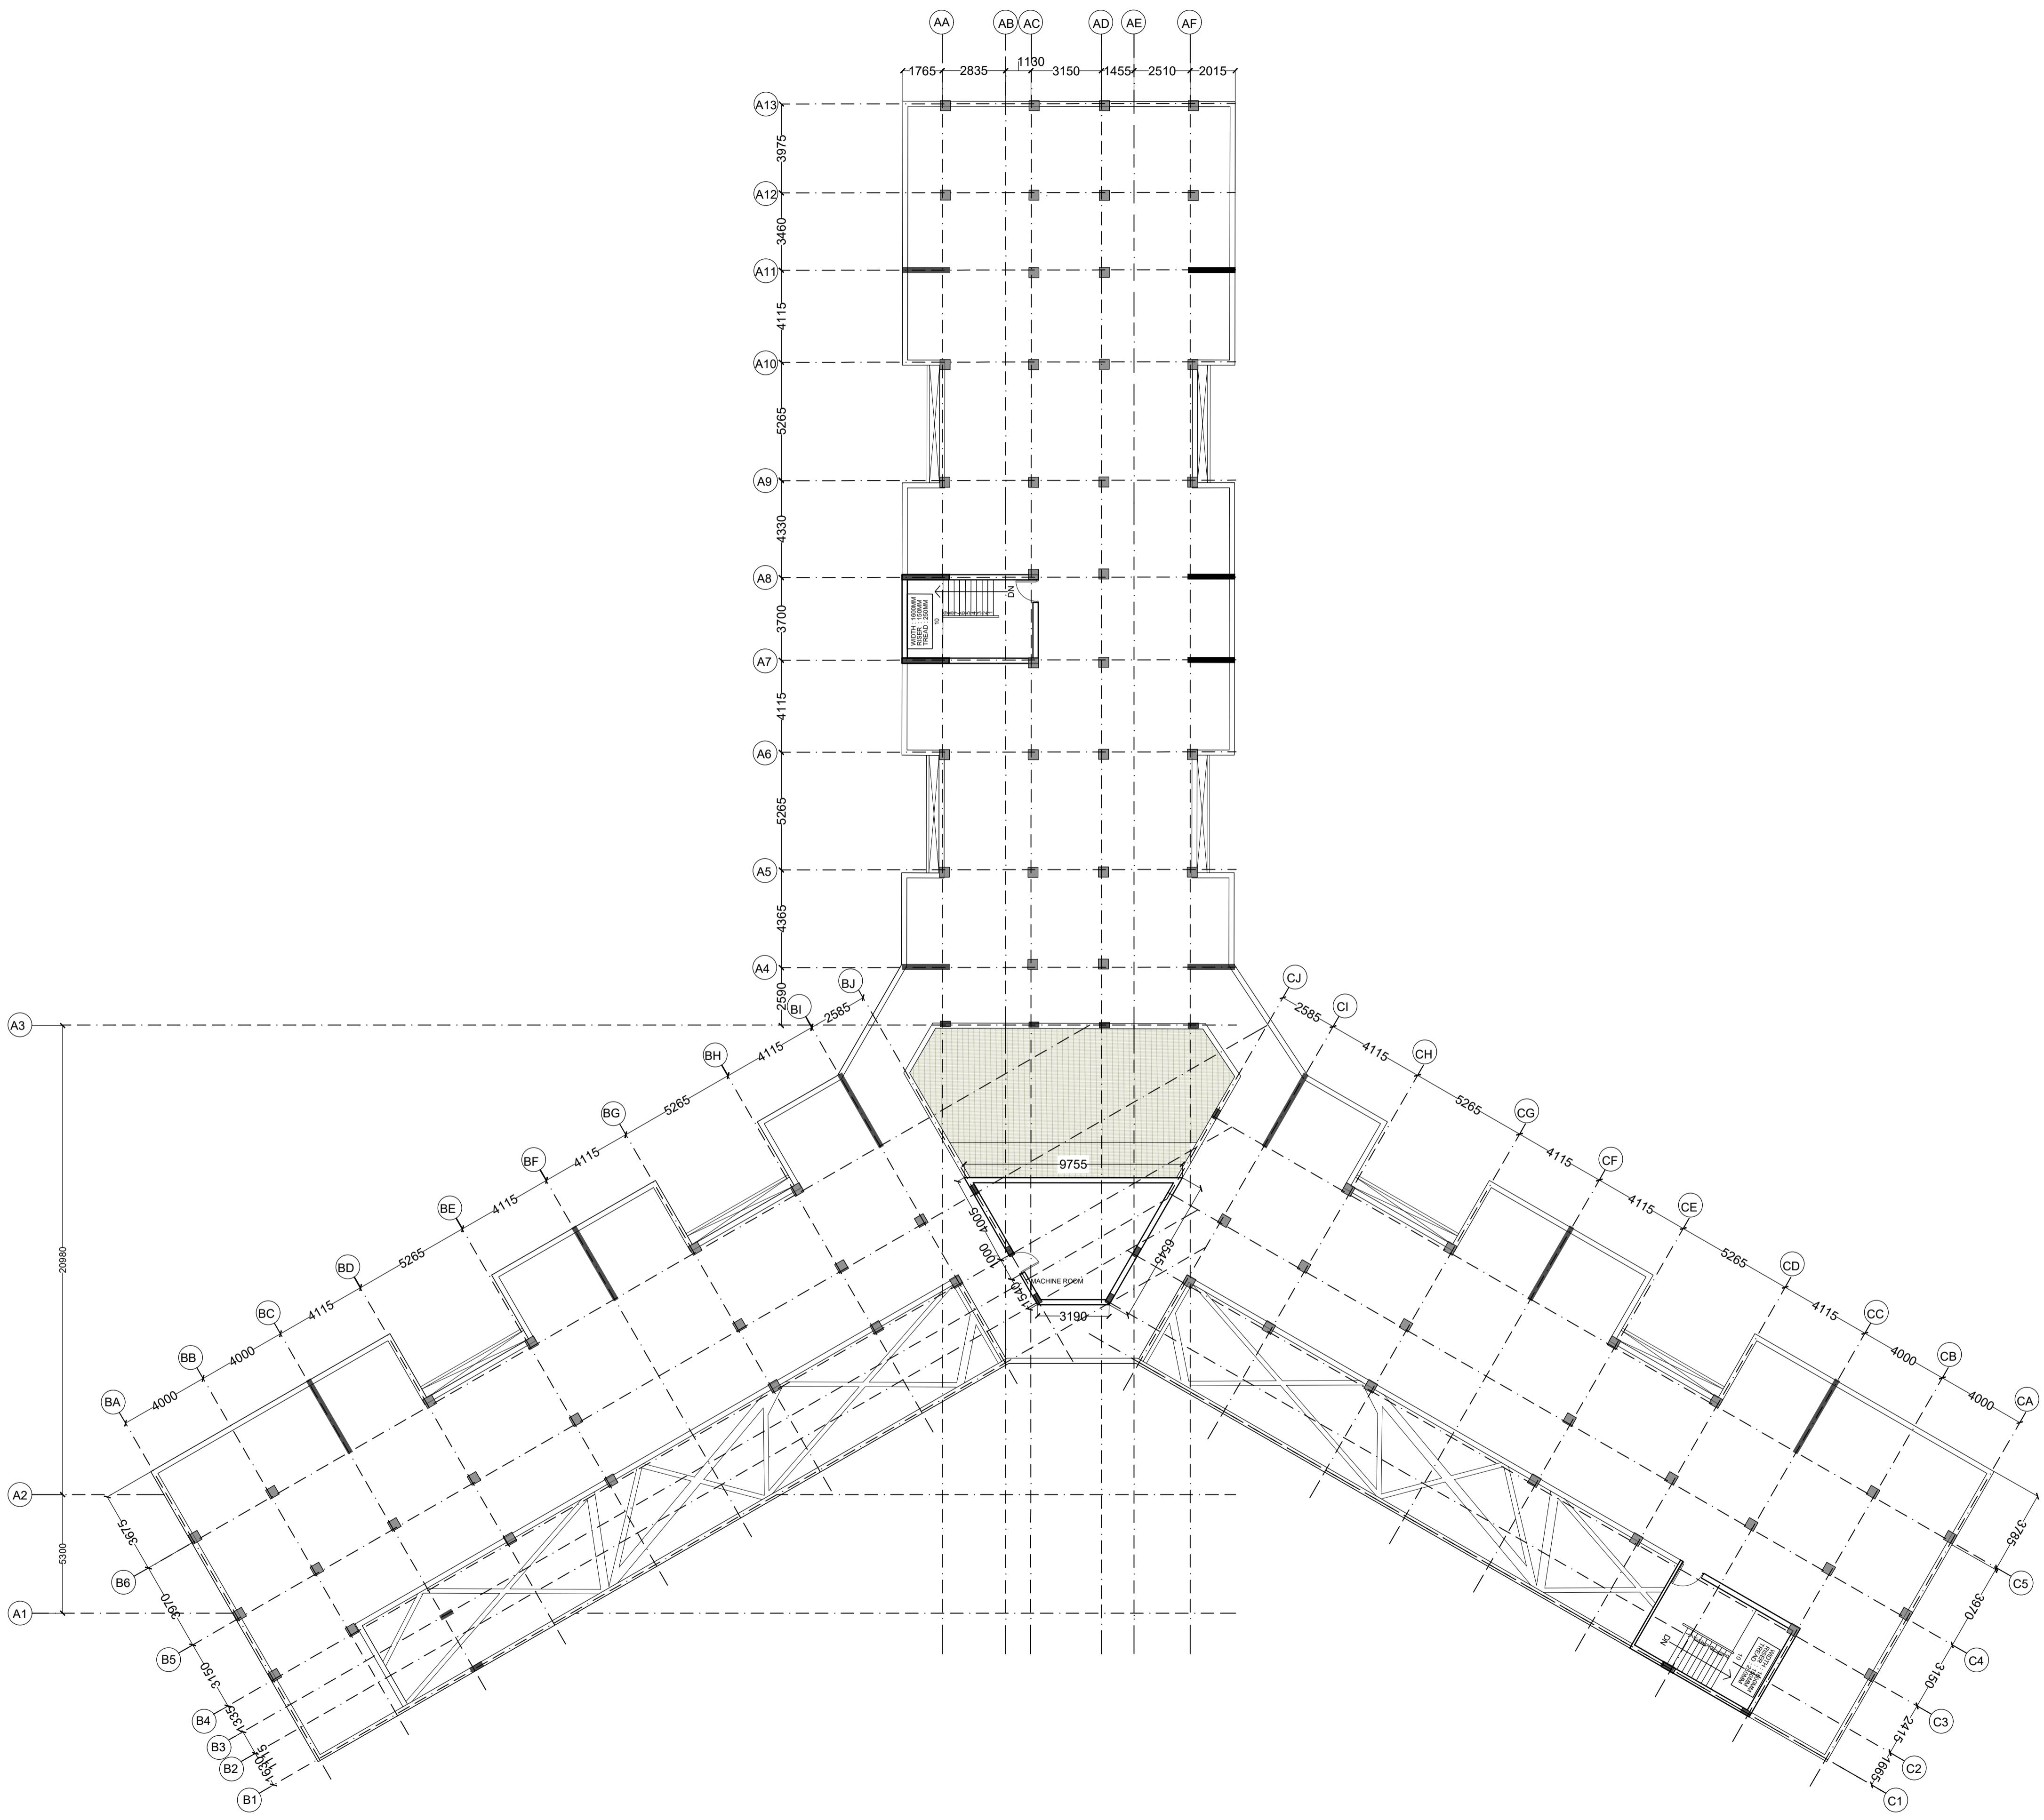




UID-SOA

NOTES

ALL DIMENSIONS ARE IN MM
ALL DIMENSIONS TO BE READ NOT MEASURED

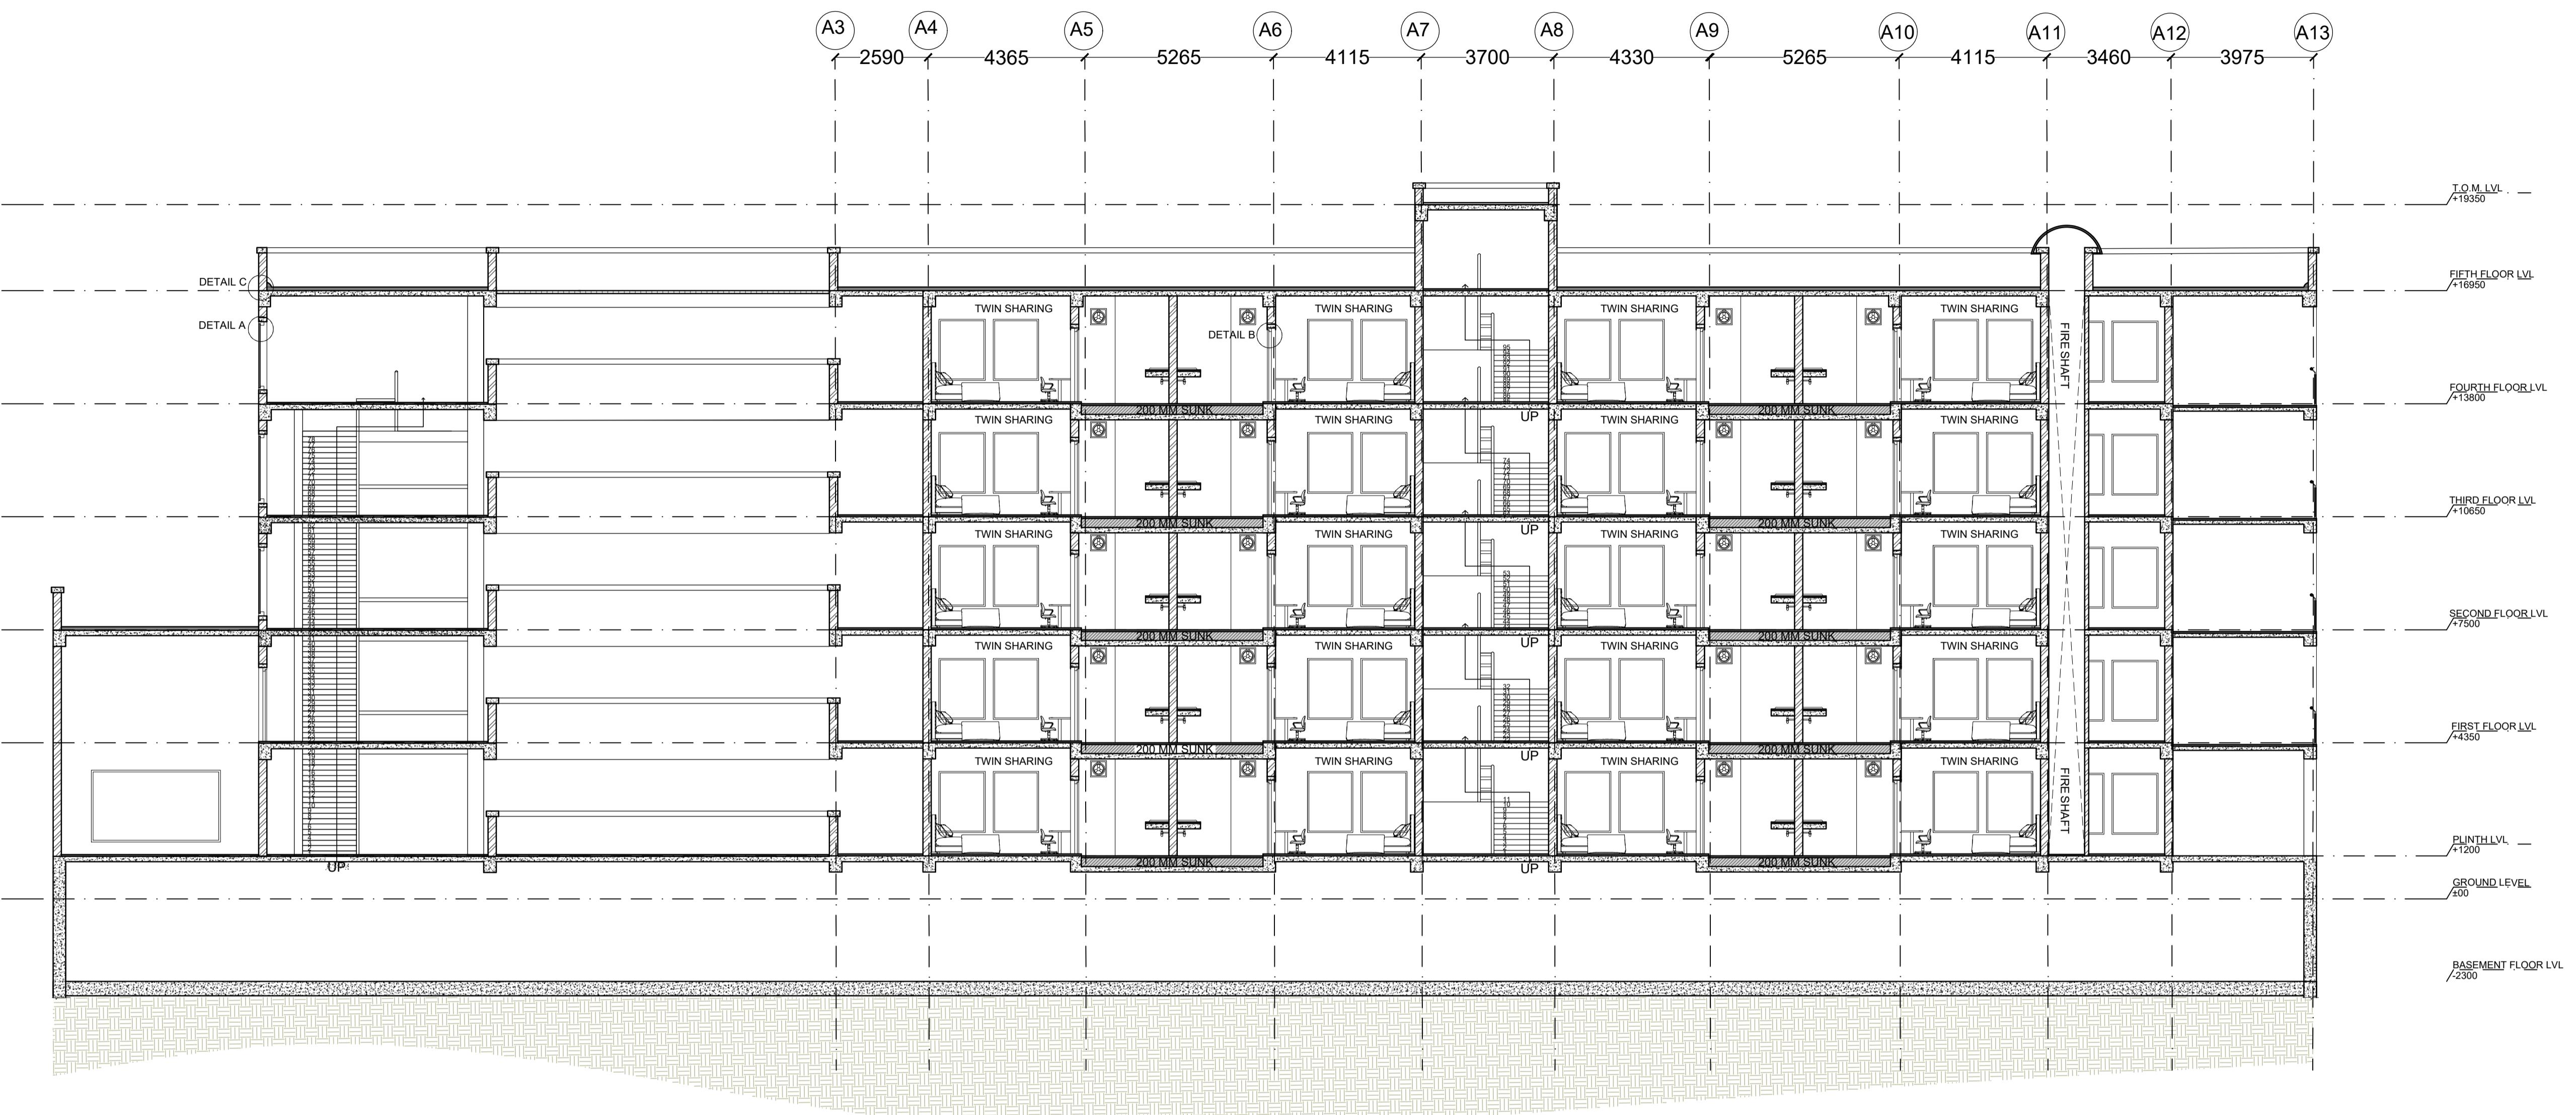

SECTION XX'

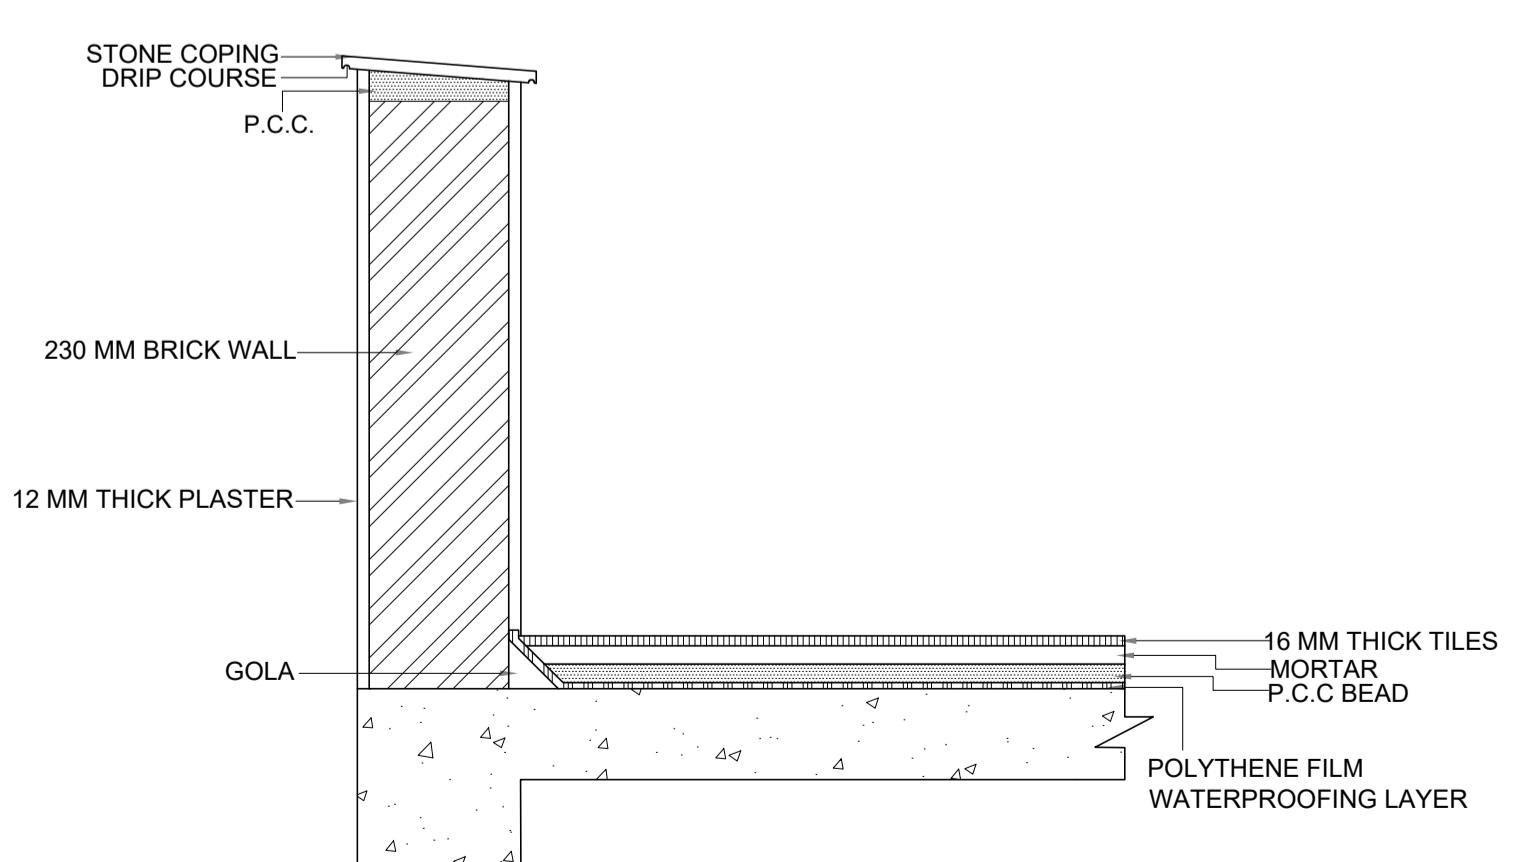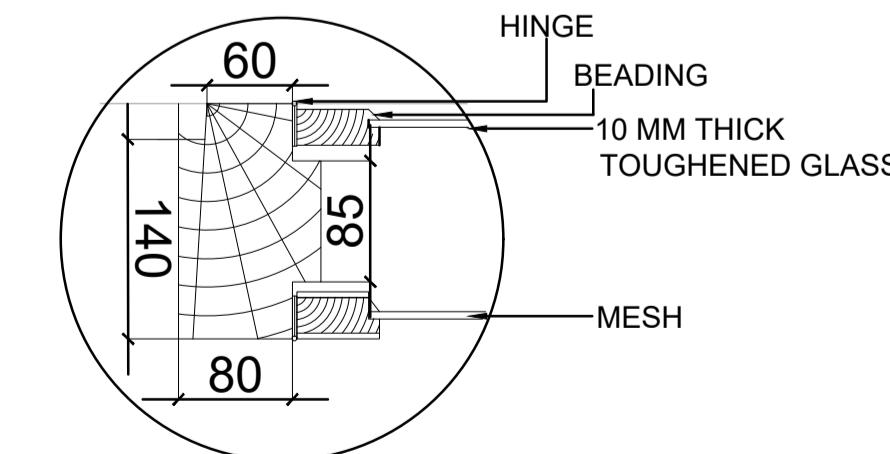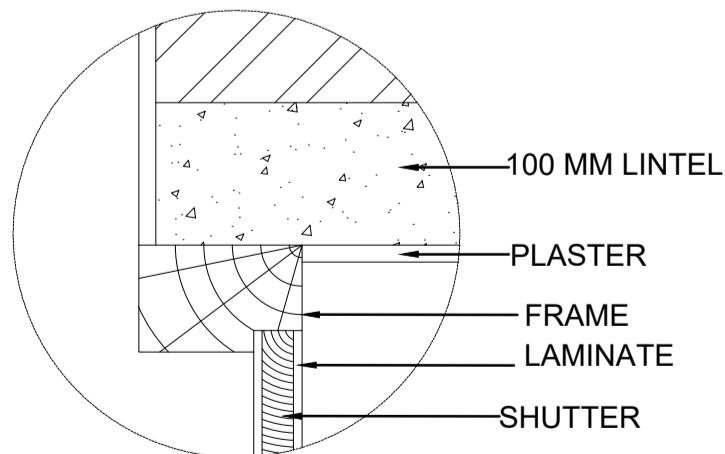


SHEET TITLE
SECTION XX'

SHEET NO. : 12
SCALE : 1 :100

PROJECT
HOSTEL WORKING DRW.


DRAWN BY YASH VARDHAN	CHECKED BY
---------------------------------	-------------------

KEY PLAN

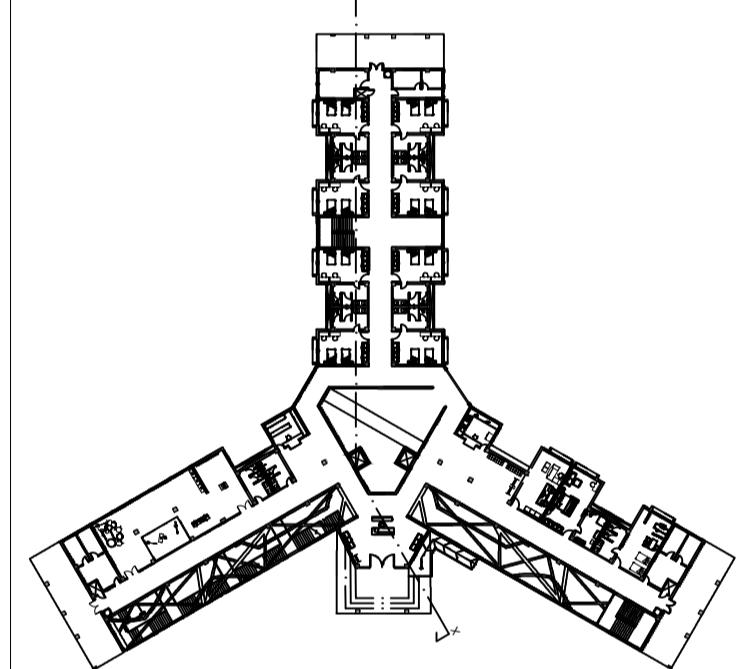


NOTES

ALL DIMENSIONS ARE IN MM
ALL DIMENSIONS TO BE READ NOT MEASURED

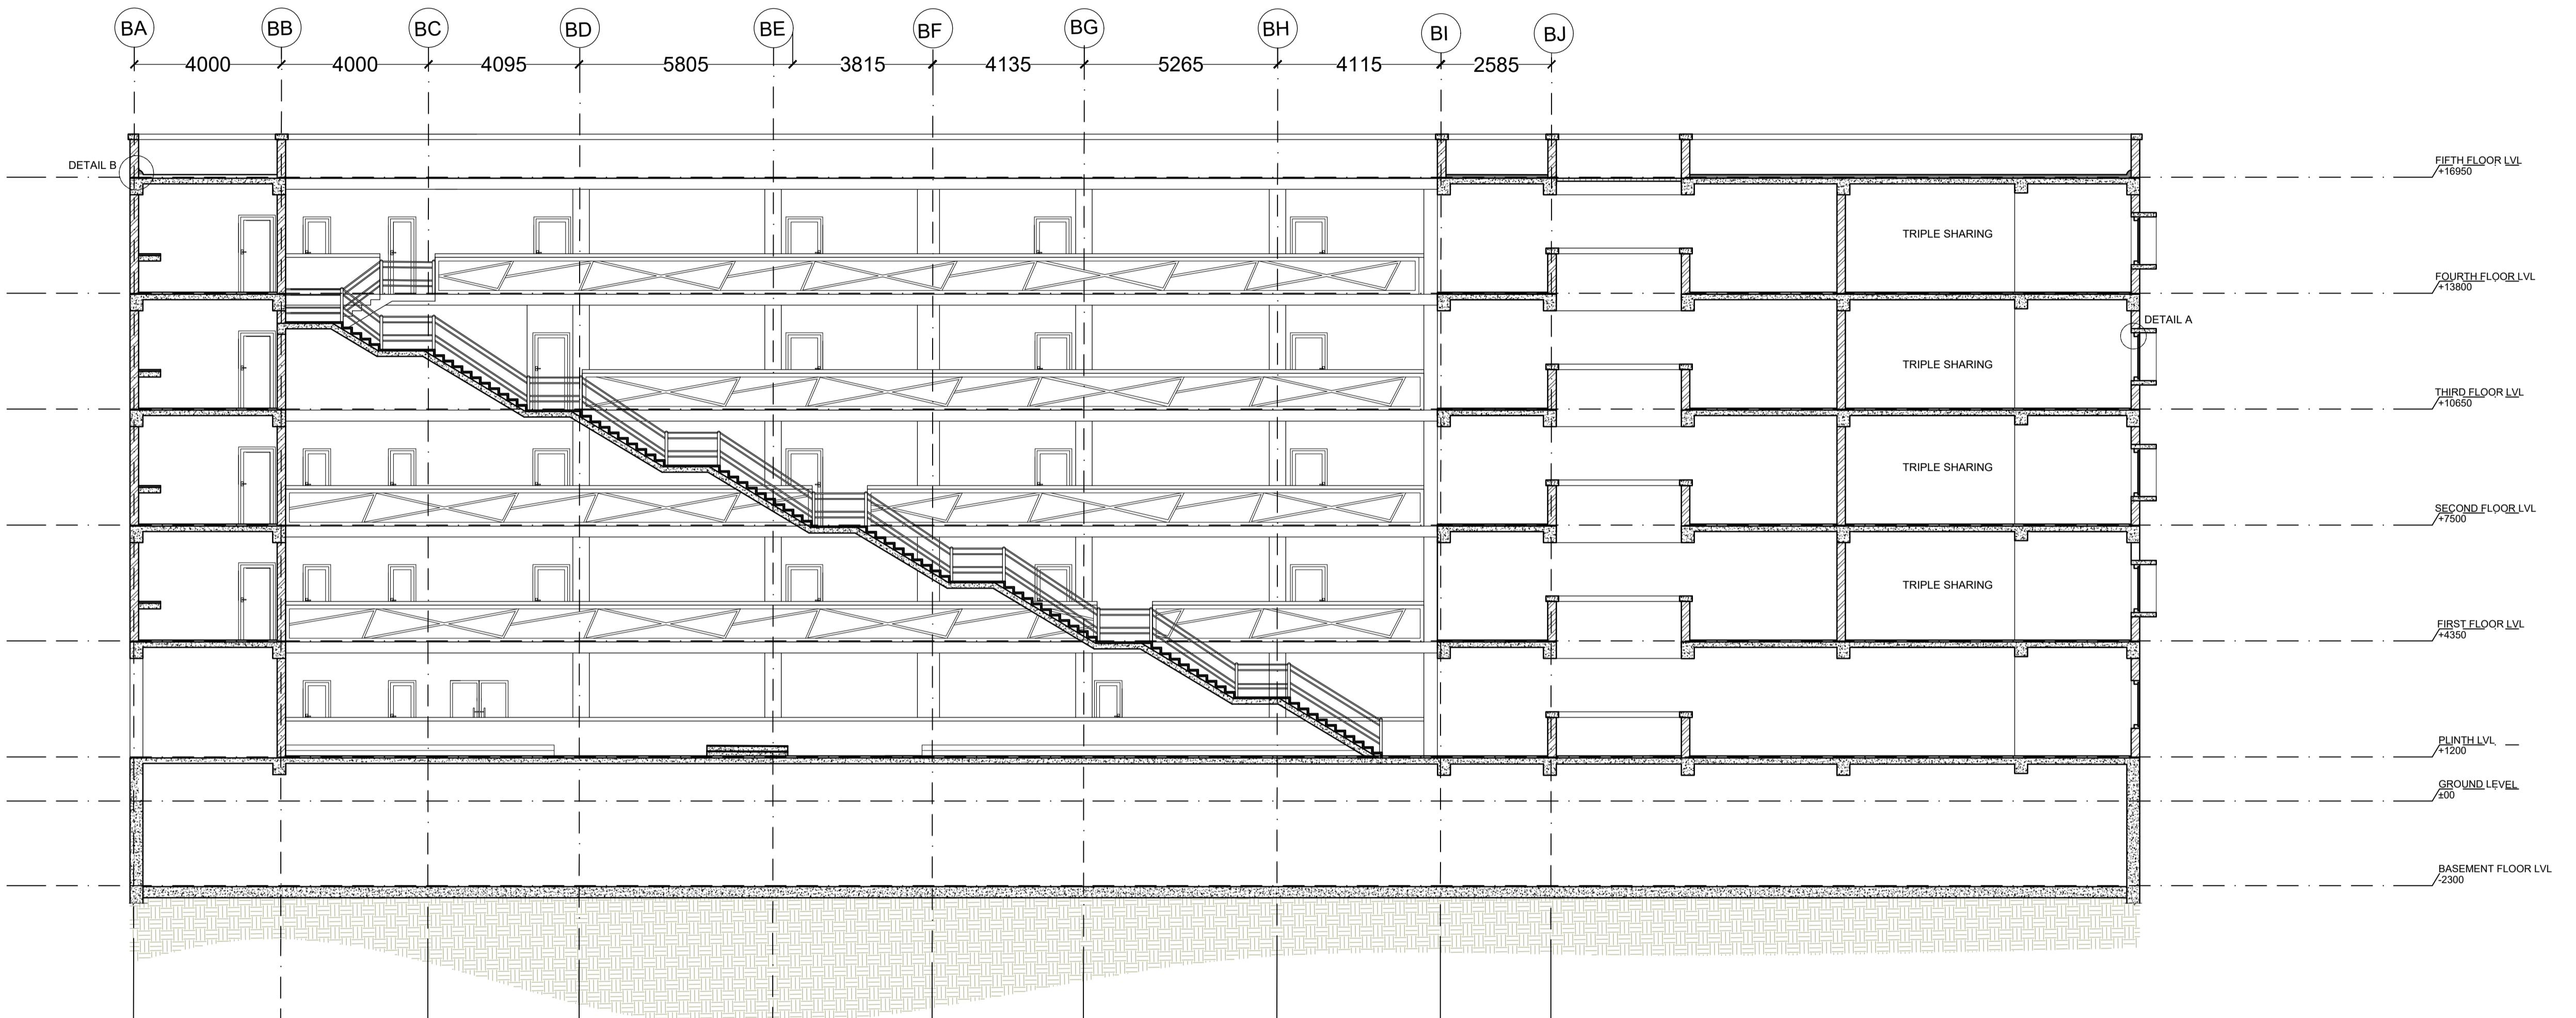

SECTION YY'

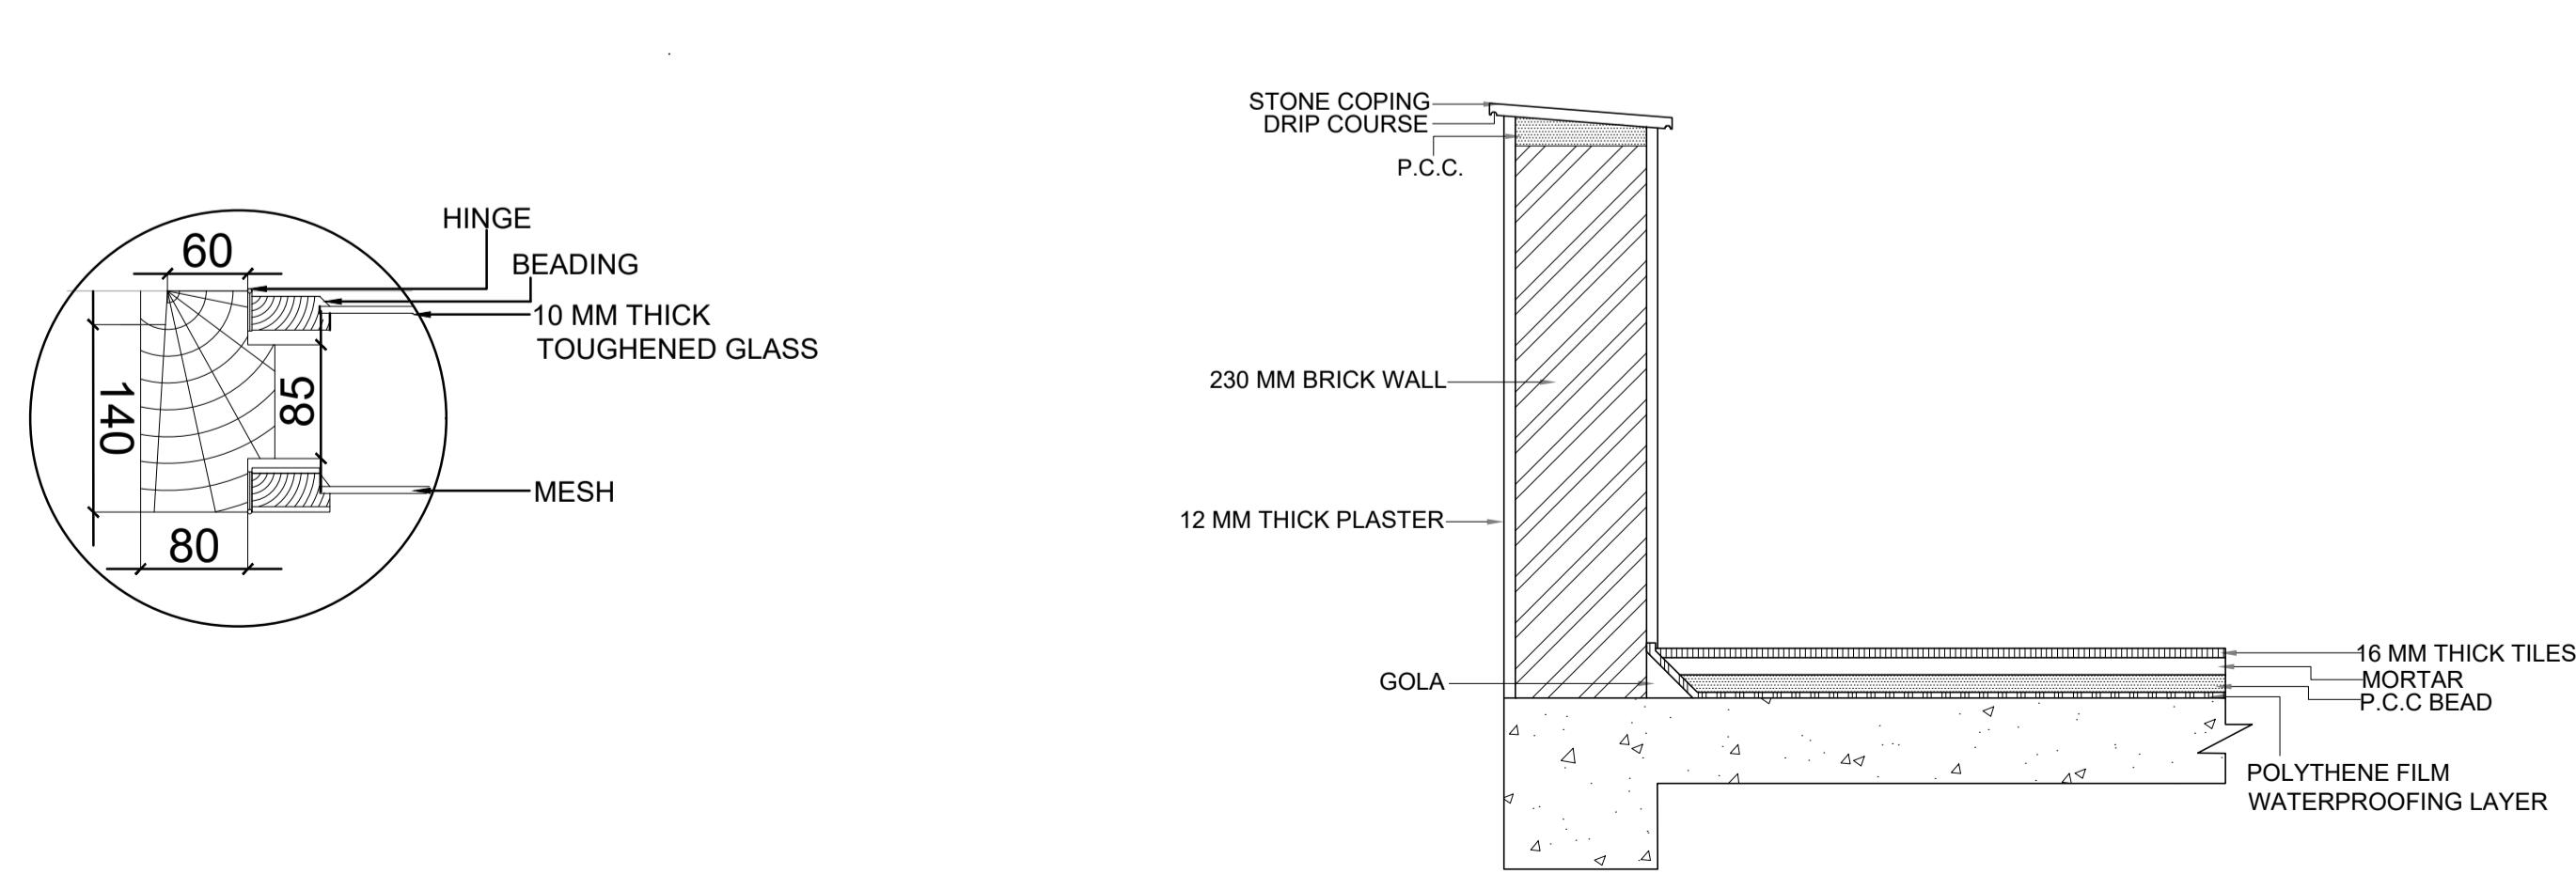

SHEET TITLE
SECTION YY'


SHEET NO.: 13
SCALE : 1:100

PROJECT
HOSTEL WORKING DRW.

DRAWN BY YASH VARDHAN	CHECKED BY
--------------------------	------------

LEGENDS


KEY PLAN

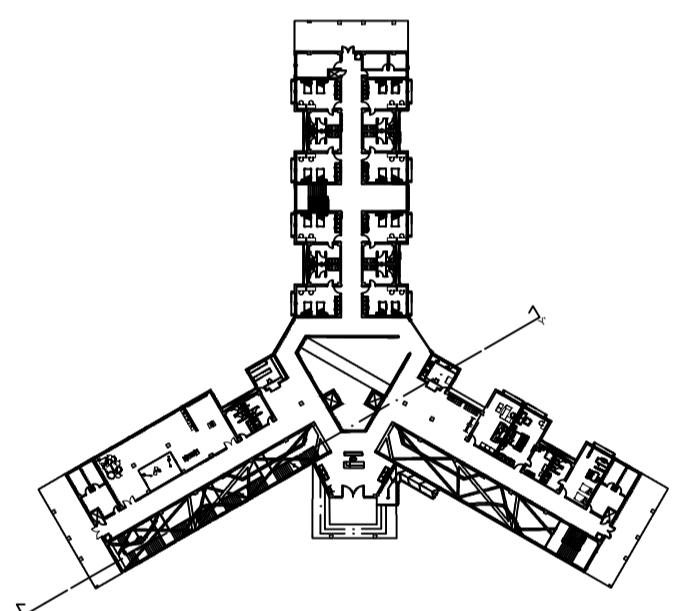

UID-SOA

NOTES

ALL DIMENSIONS ARE IN MM
ALL DIMENSIONS TO BE READ NOT MEASURED

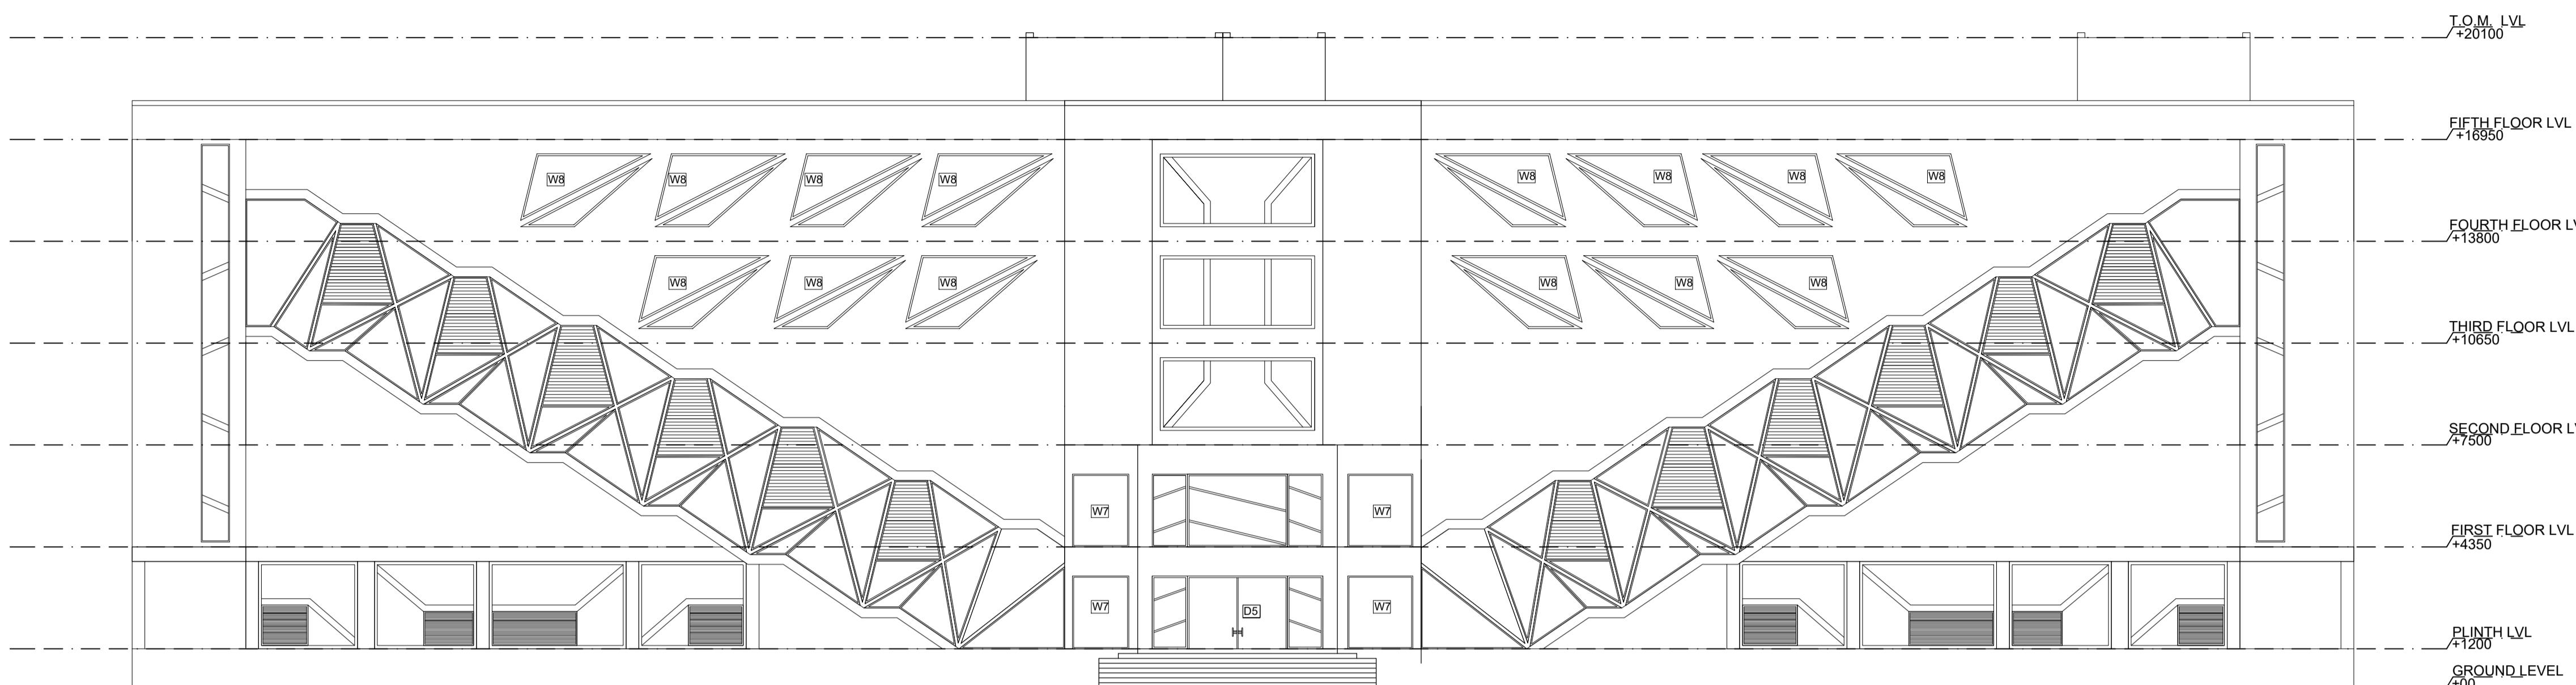


WINDOW SCHEDULE			
S.No.	Sill	Lintel	Width
1.	600	2300	1235
2.	600	2600	550
3.	600	2300	3000
4.	600	2300	1800
5.	600	2300	1400
6.	350	2600	2400
7.	00	2250	4040
8.	450	2600	2400

LEGENDS

DOOR SCHEDULE			
S.No.	Sill	Lintel	Width
1.	0	2250	1000
2.	0	2250	850
3.	0	2250	1800
4.	0	2250	1800
5.	0	2250	3200

KEY PLAN

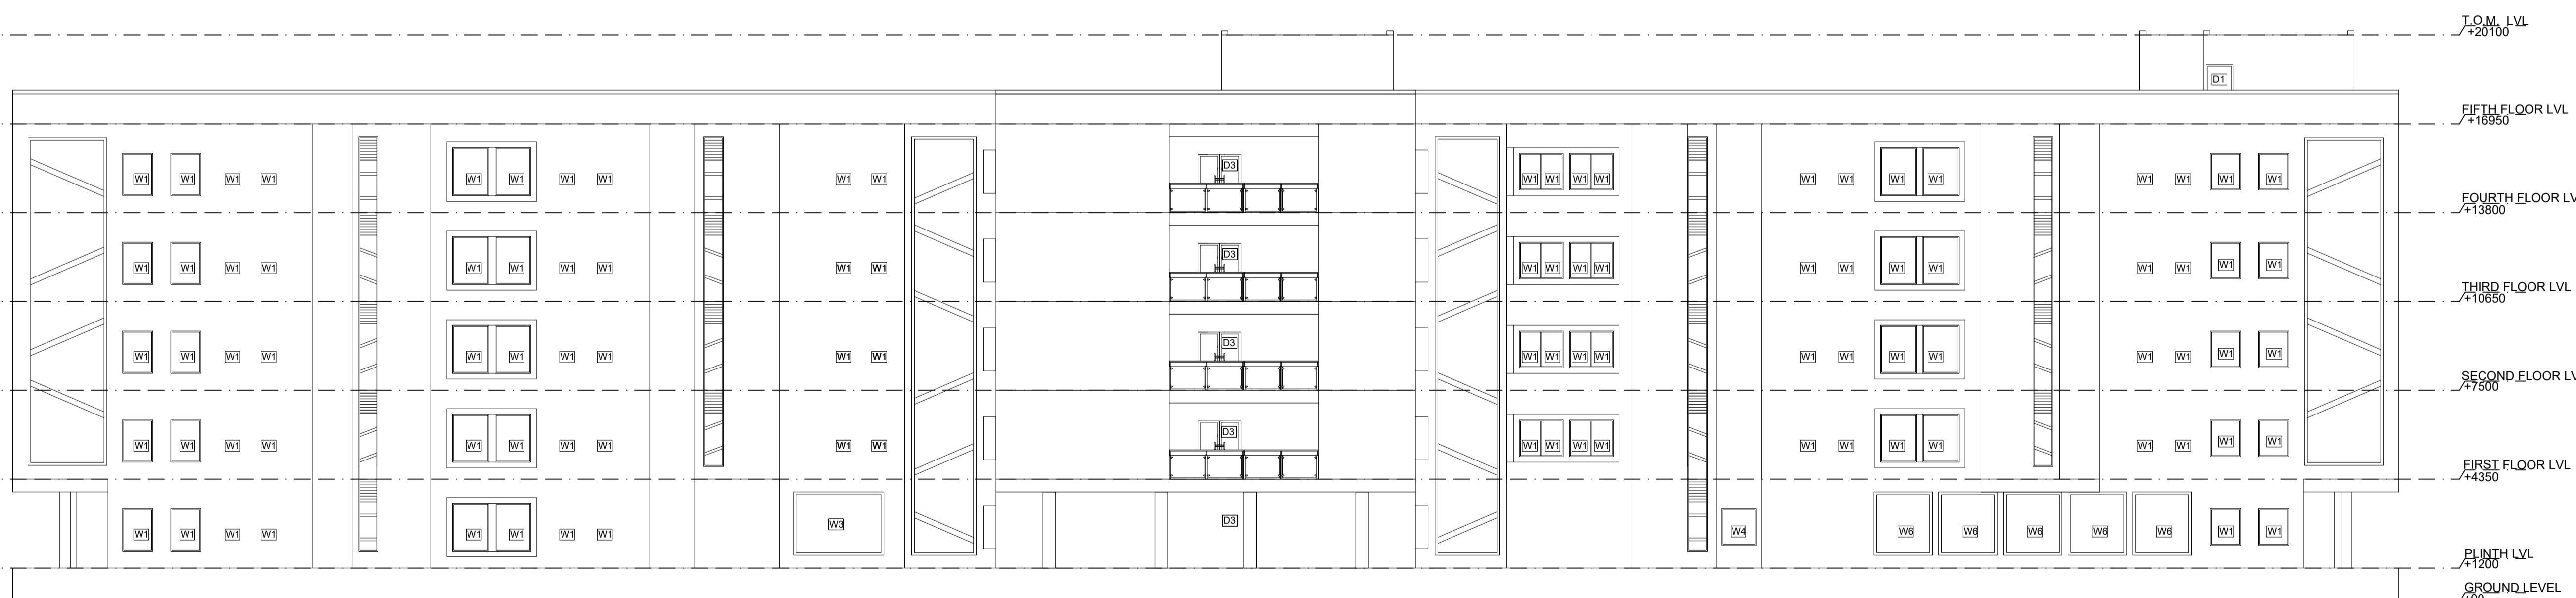

REAR ELEVATION

SHEET TITLE

ELEVATIONS

SHEET NO. : 14
SCALE : 1 : 125



PROJECT
HOSTEL WORKING DRW.

DRAWN BY YASH VARDHAN | CHECKED BY

UID-SOA

NOTES



ALL DIMENSIONS ARE IN MM
ALL DIMENSIONS TO BE READ NOT MEASURED

WINDOW SCHEDULE			
S.No.	Sill	Lintel	Width
1.	600	2300	1235
2.	600	2600	550
3.	600	2300	3000
4.	600	2300	1800
5.	600	2300	1400
6.	350	2600	2400
7.	00	2250	4040
8.	450	2600	2400

LEGENDS

DOOR SCHEDULE			
S.No.	Sill	Lintel	Width
1.	0	2250	1000
2.	0	2250	850
3.	0	2250	1800
4.	0	2250	1800
5.	0	2250	3200

KEY PLAN

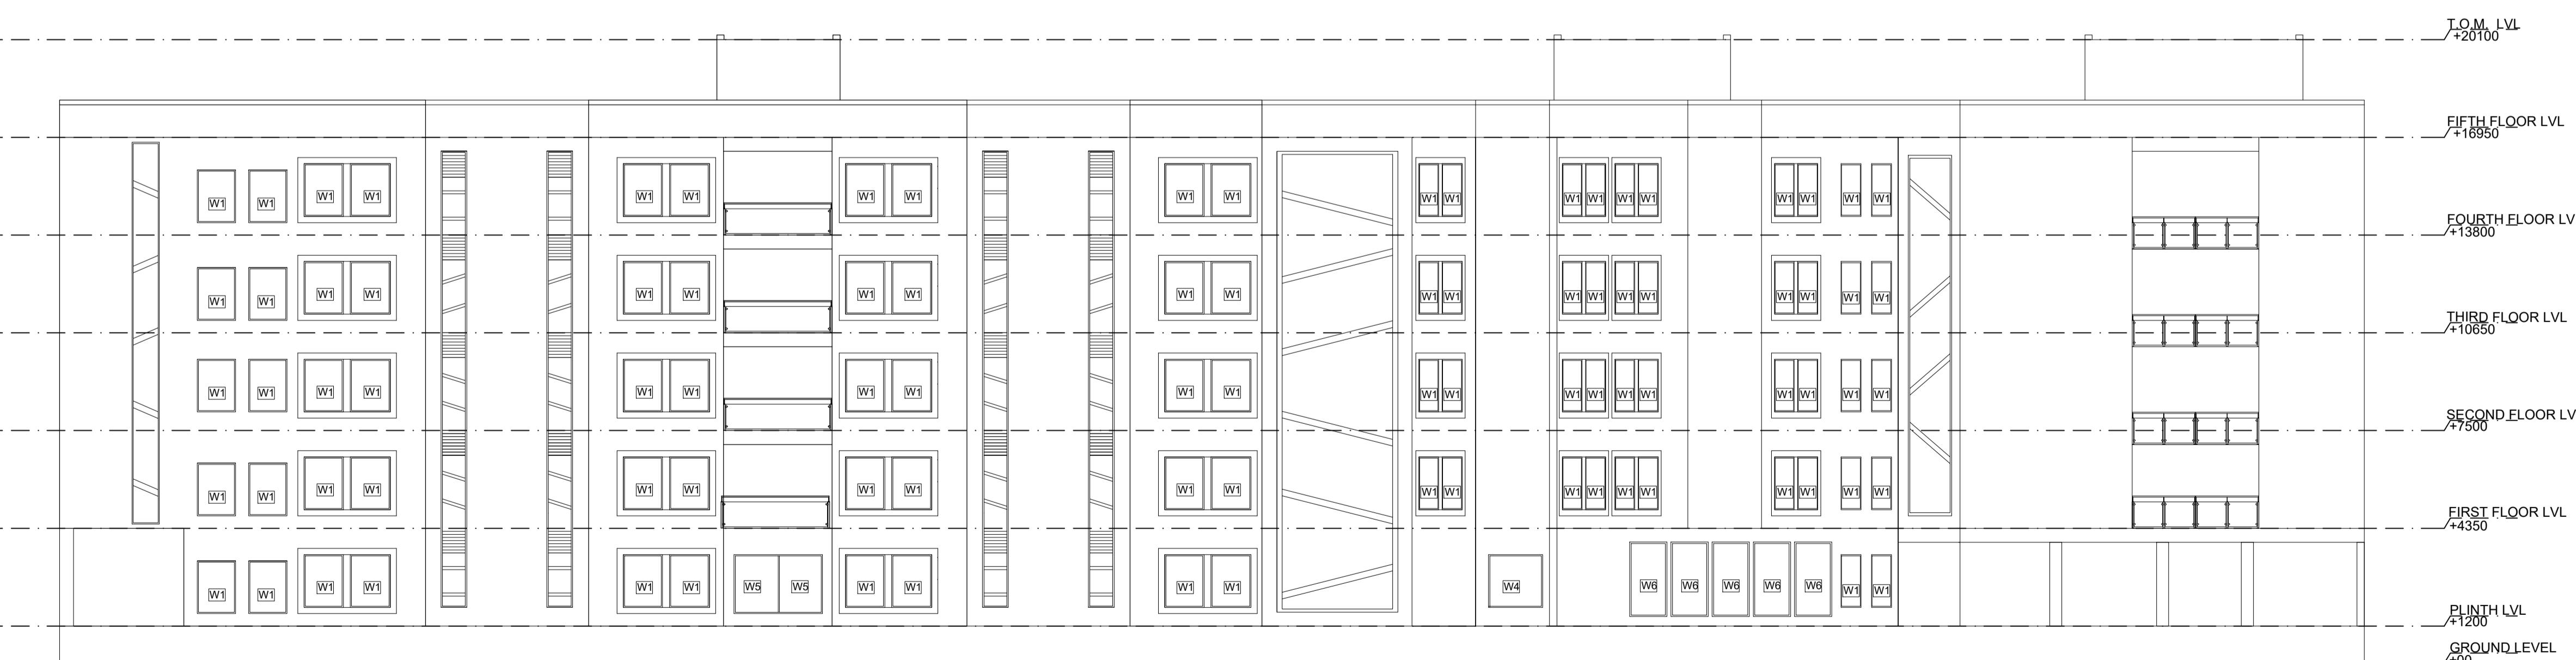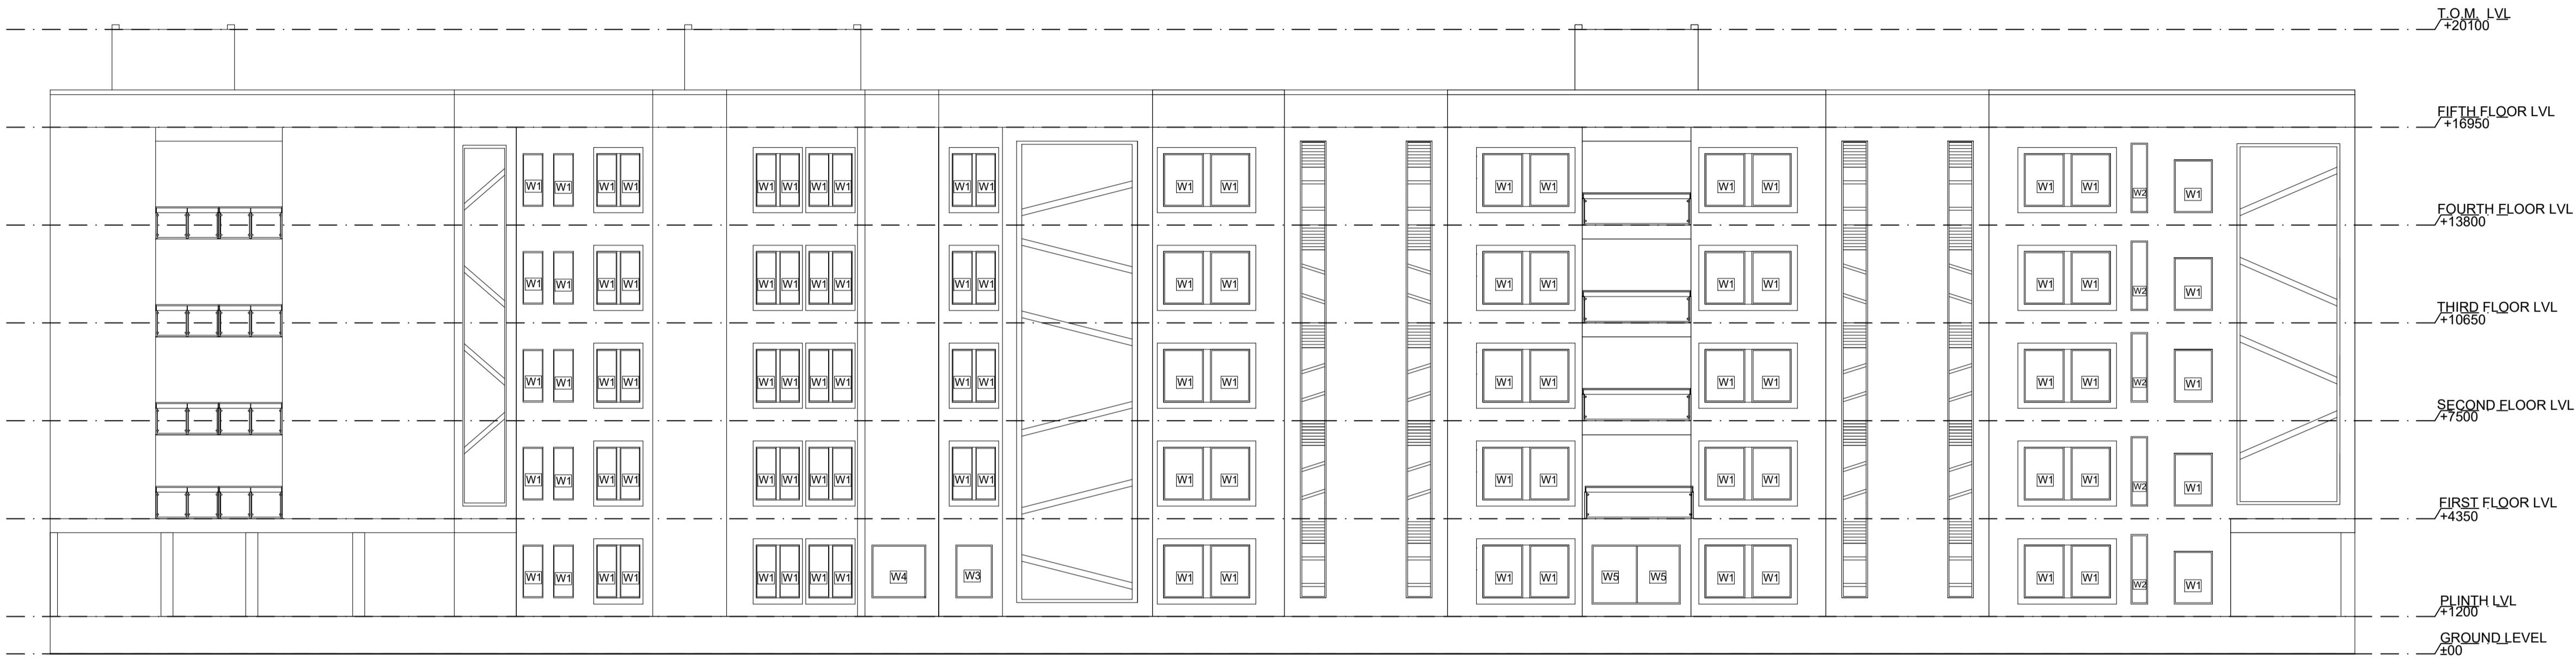

SHEET TITLE

ELEVATIONS

SHEET NO. : 15
SCALE : 1:150



PROJECT
HOSTEL WORKING DRW.

DRAWN BY
YASH VARDHAN

CHECKED BY

UID-SOA


NOTES

ALL DIMENSIONS ARE IN MM
ALL DIMENSIONS TO BE READ NOT MEASURED


LEGENDS

230 MM THICK BRICK WALL
TILES AND PLASTER
CERAMIC TILES
(300X300X10)


KEY PLAN

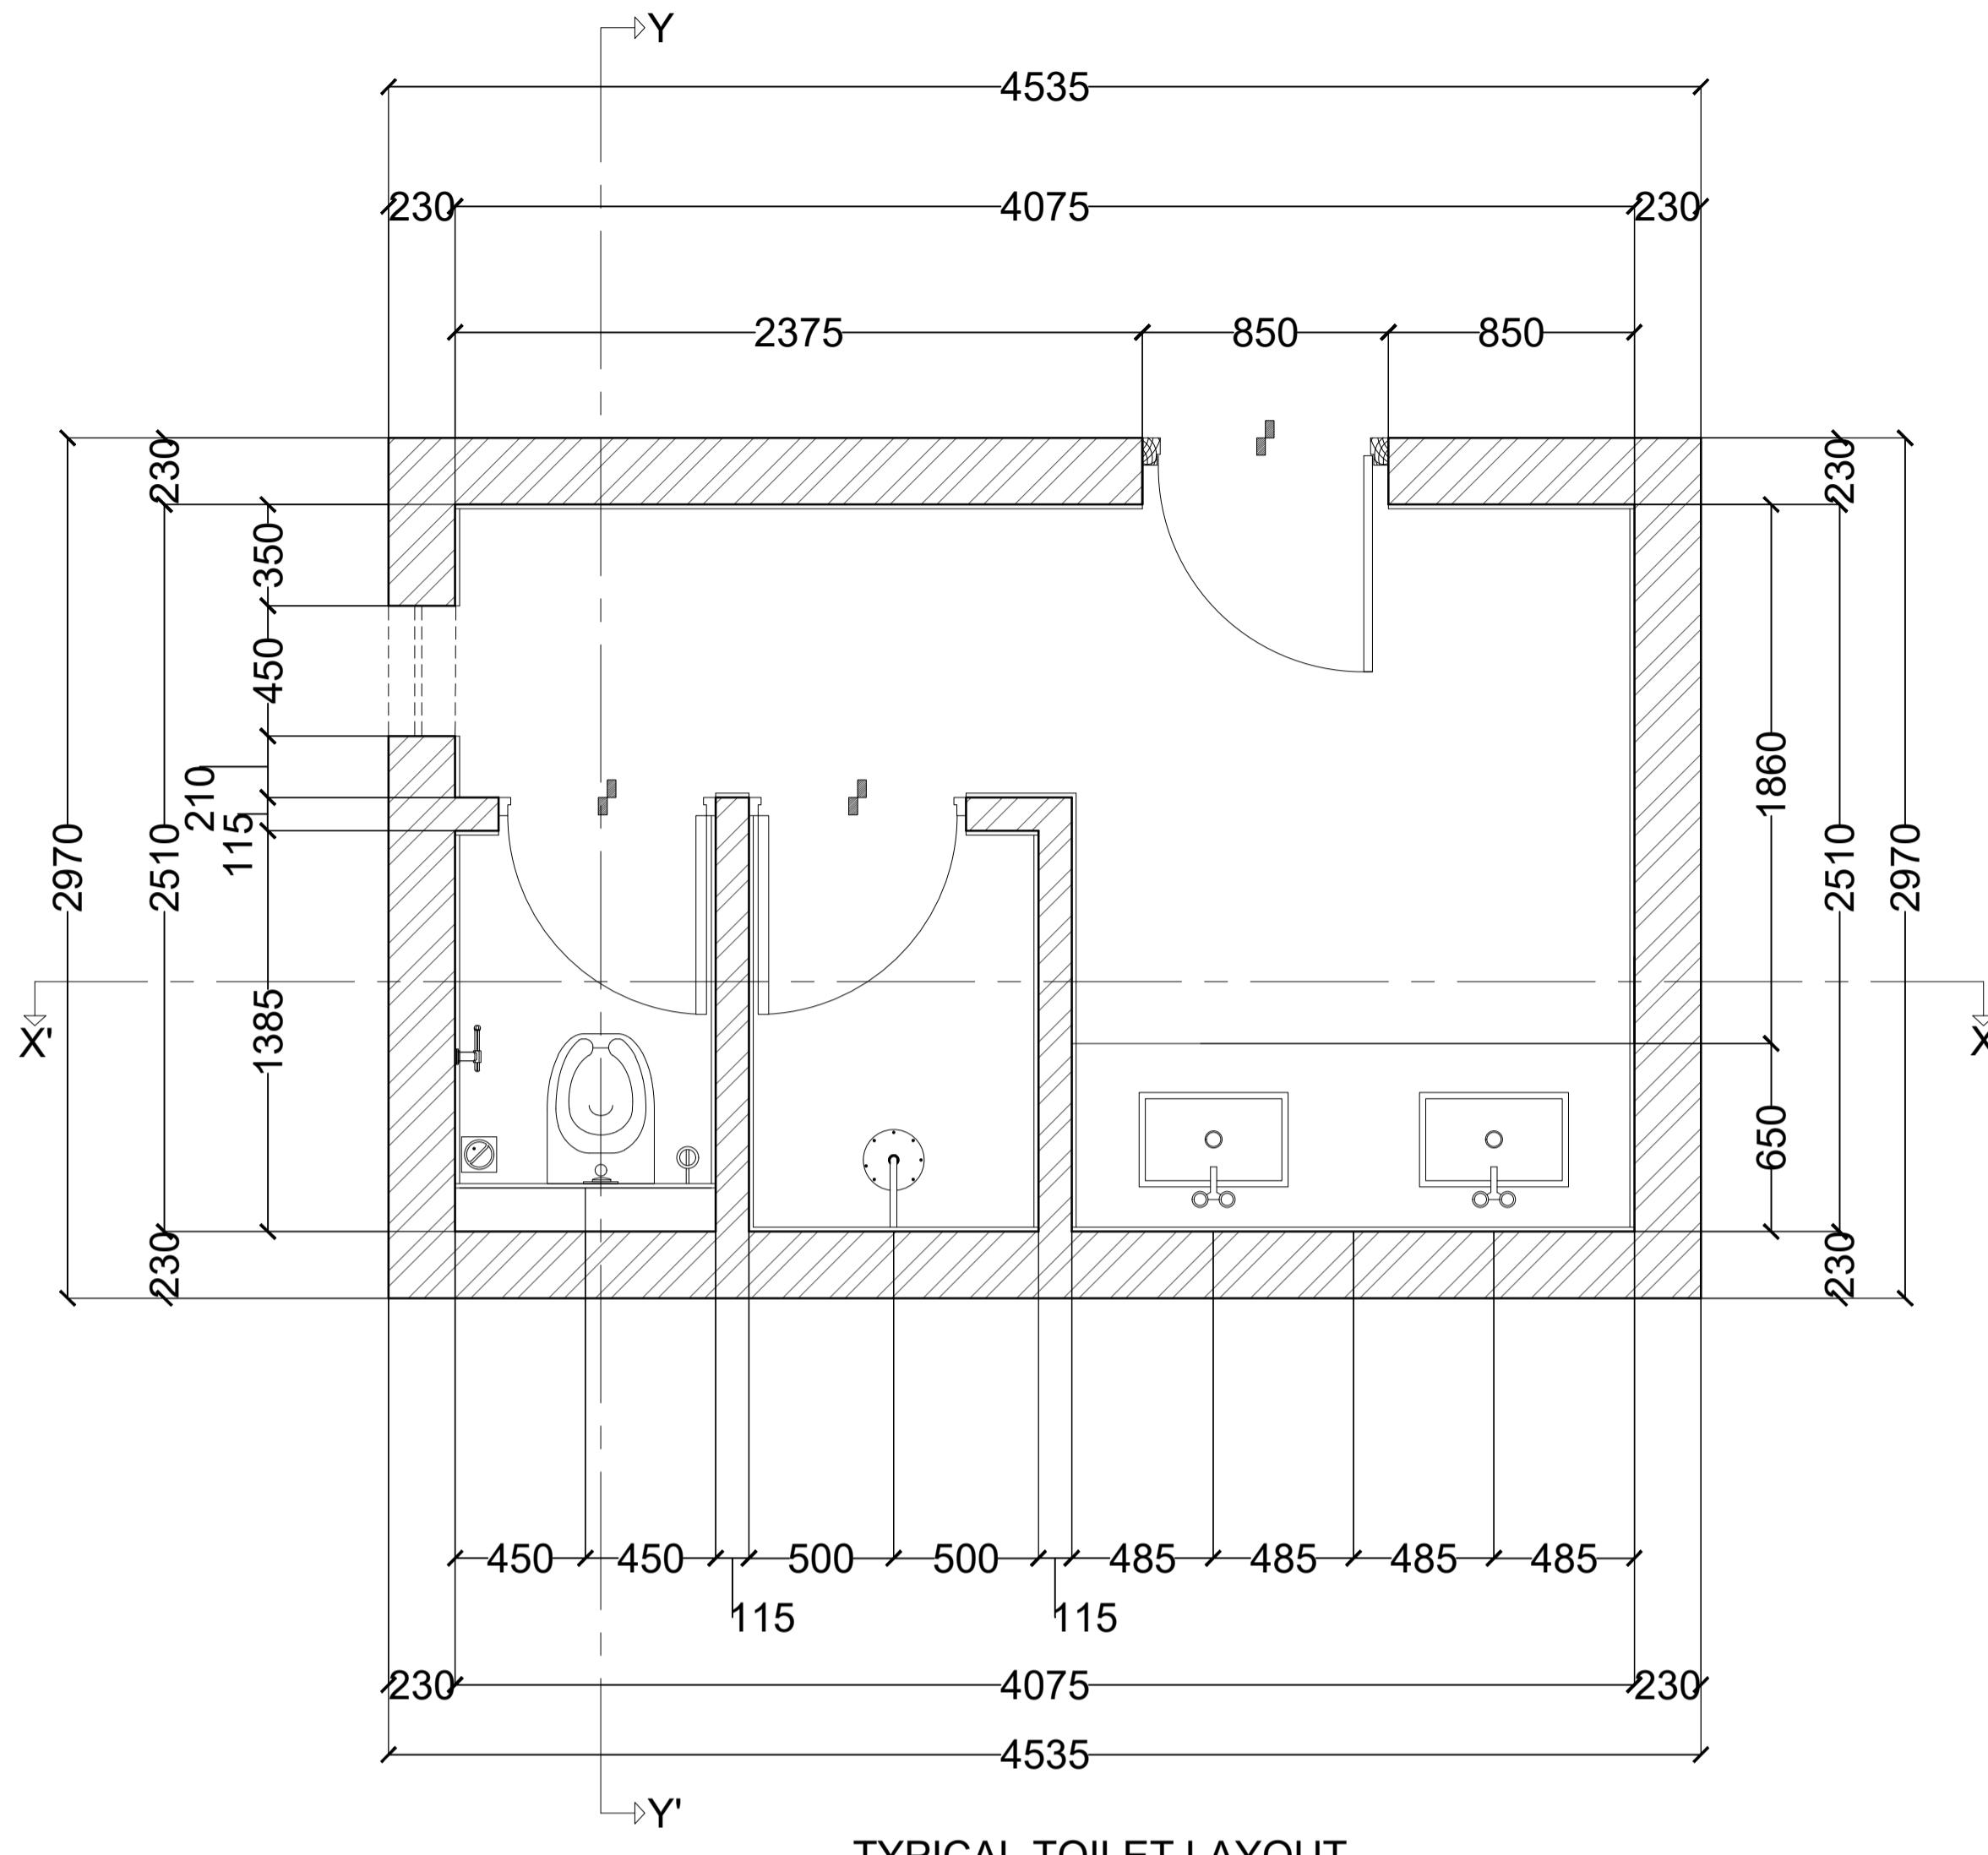


TYPICAL TOILET LAYOUT

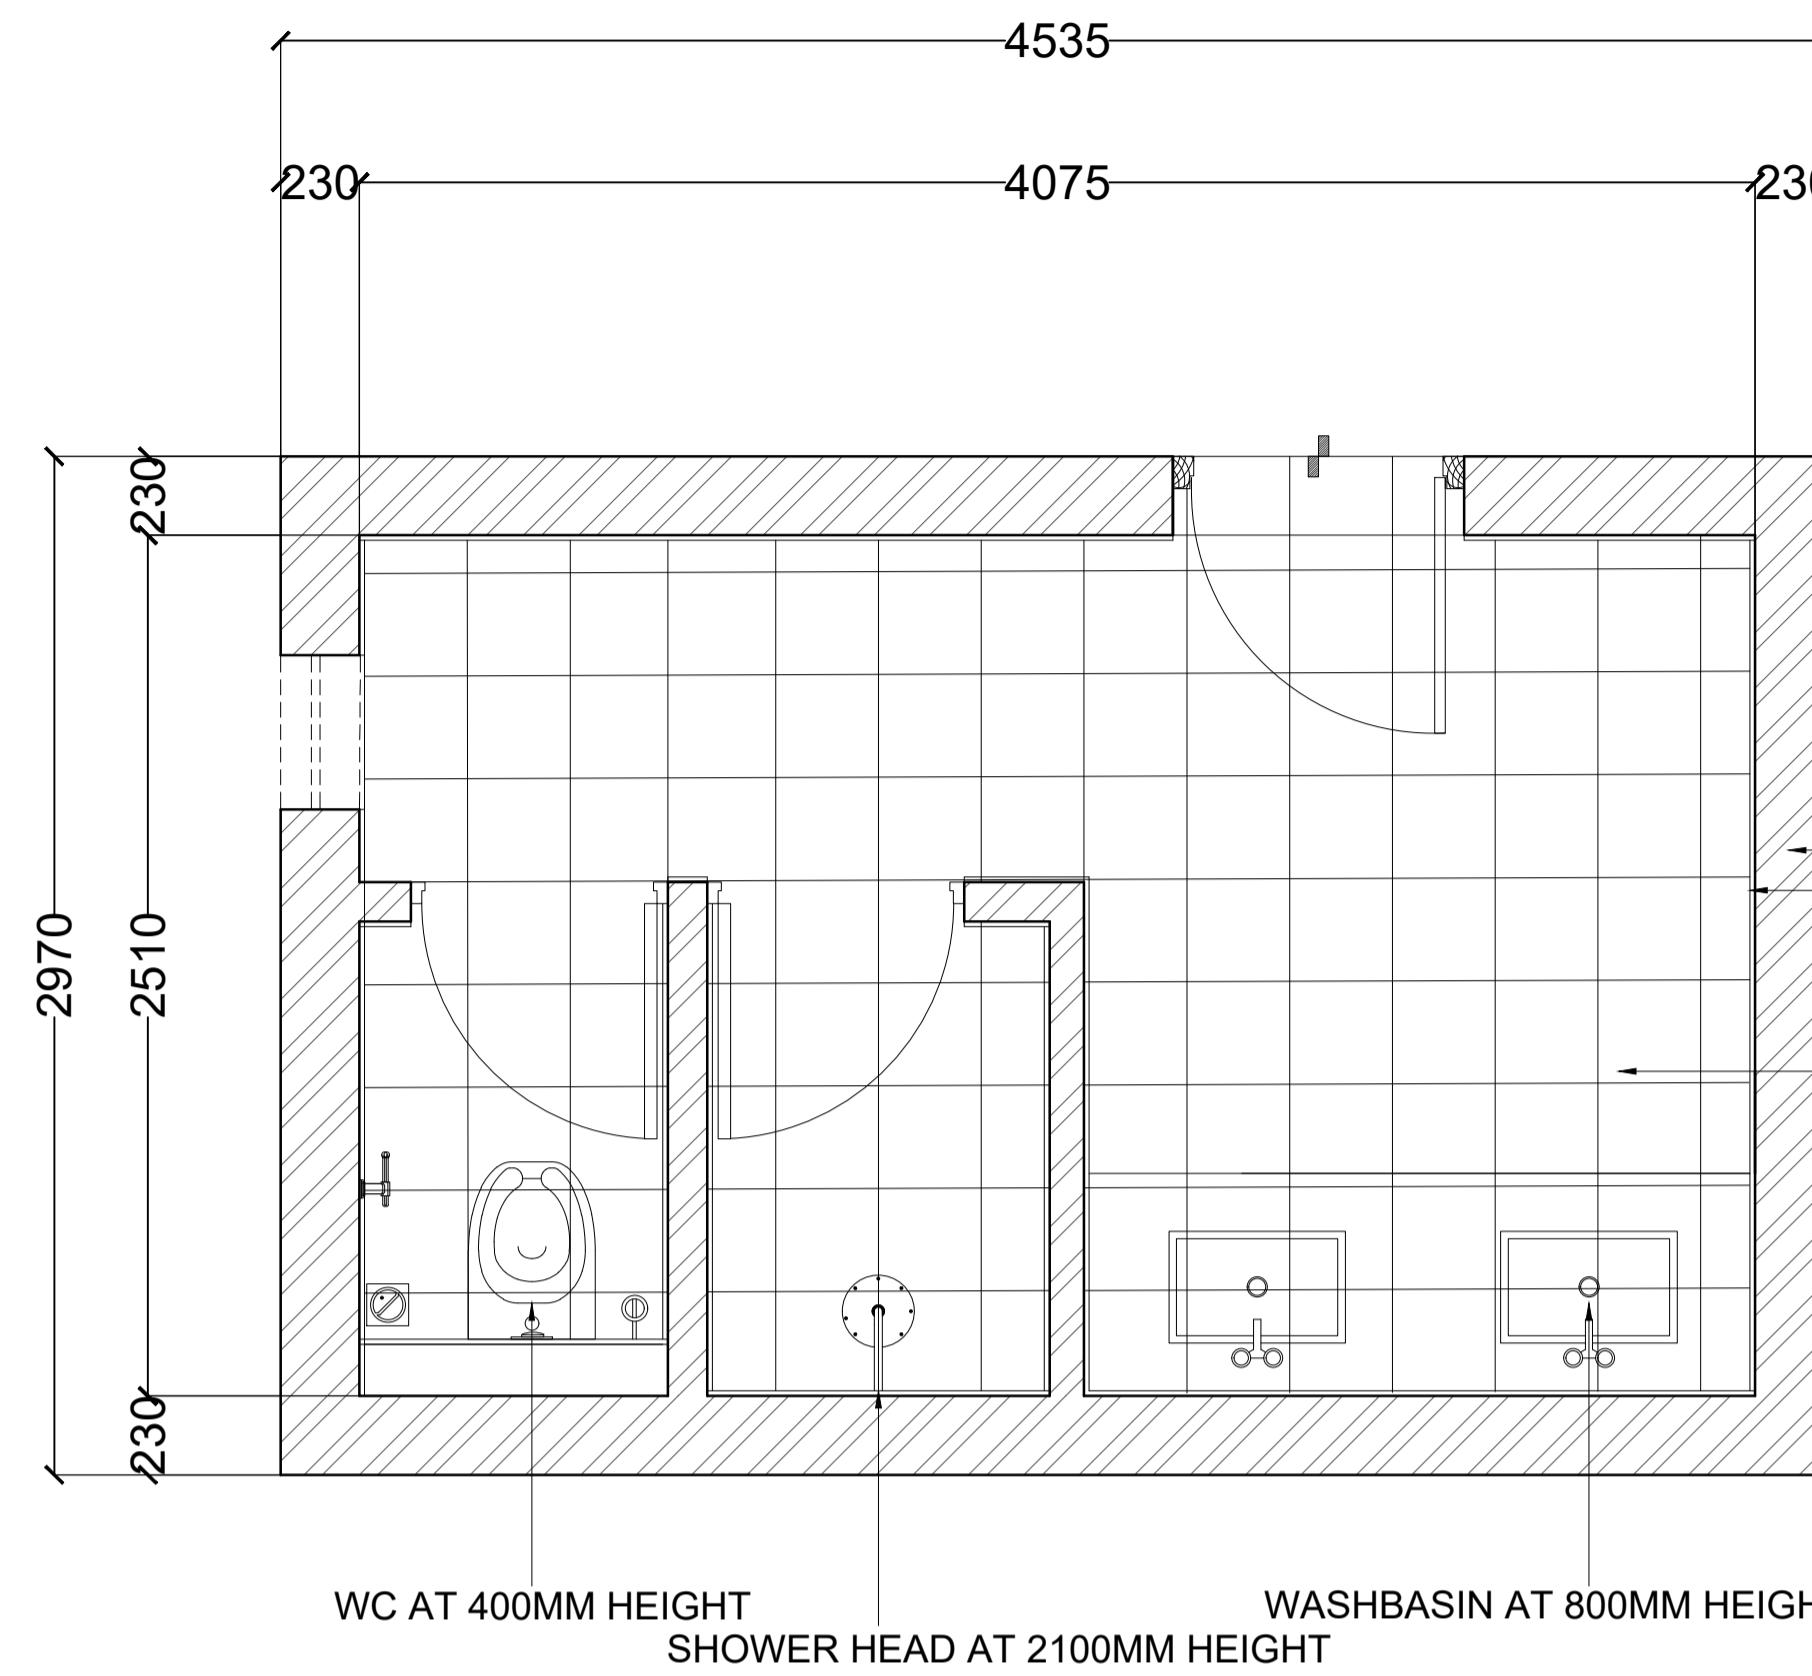

FLOORING LAYOUT

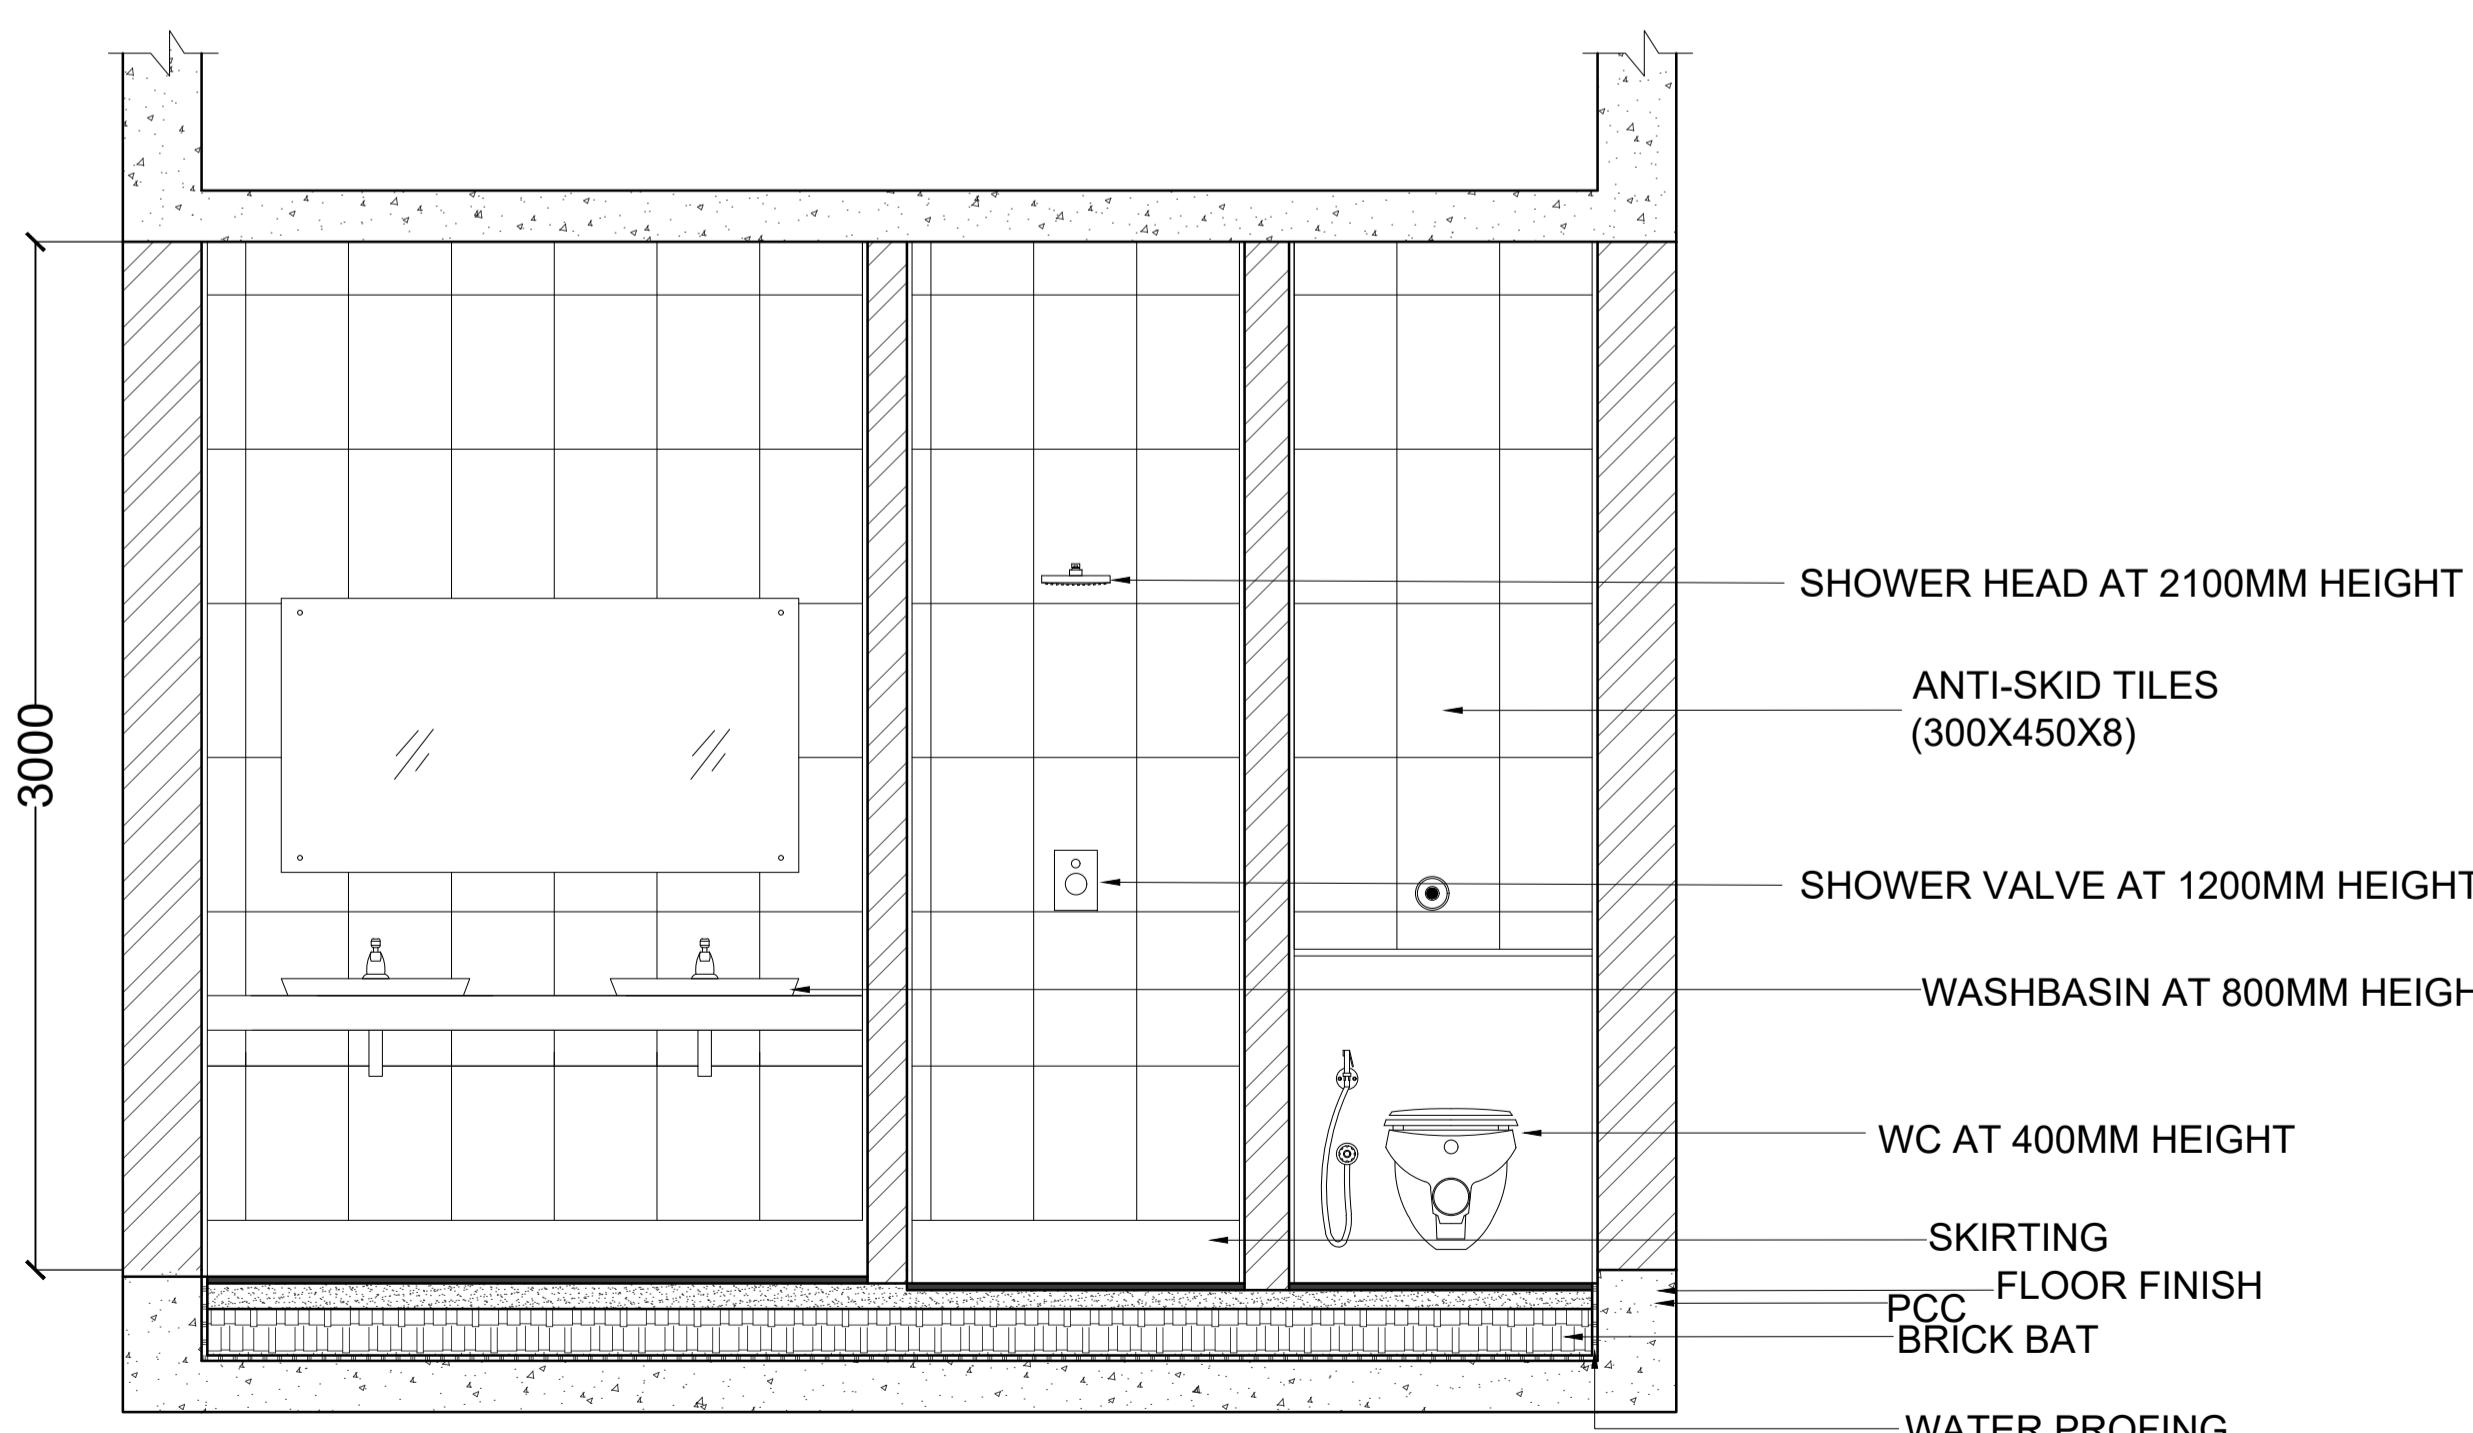

SECTION XX'

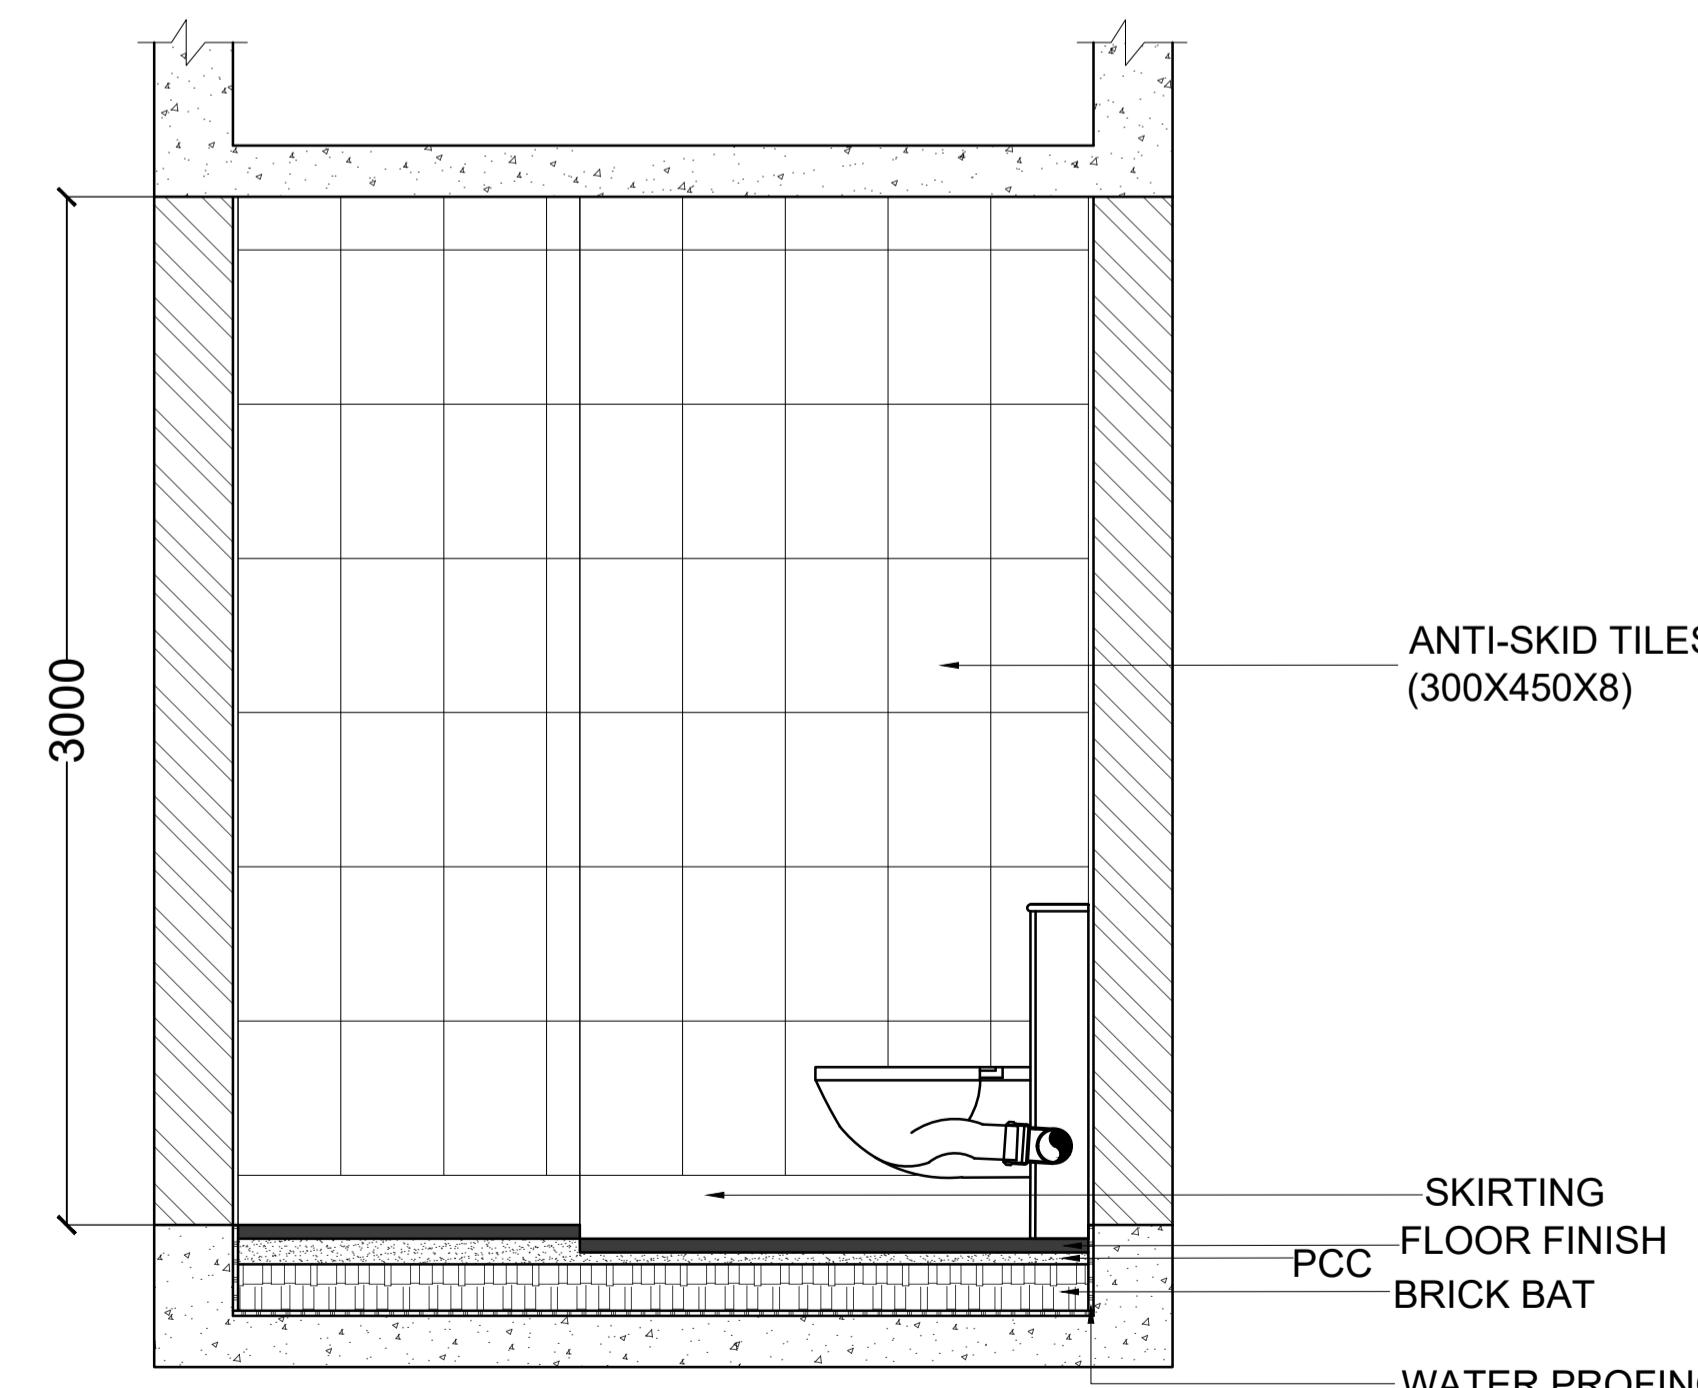

SECTION YY'

SHEET TITLE
TOILET DETAIL

SHEET NO.: 16
SCALE : 1:20



PROJECT
HOSTEL WORKING DRW.
DRAWN BY
YASH VARDHAN

CHECKED BY

UID-SOA

UID-SOA

NOTES

ALL DIMENSIONS ARE IN MM

ALL DIMENSIONS TO BE READ NOT MEASURED

LEGENDS

KEY PLAN

SHEET TITLE

RESIDENCE KITCHEN DETAIL

SHEET NO. : 17

SCALE : 1 :20

A compass rose icon with a vertical line pointing upwards labeled 'N'.

PROJECT

HOSTEL WORKING DRW.

DRAWN BY

YASH VARDHAN

CHECKED BY




UID-SOA

NOTES

ALL DIMENSIONS ARE IN MM
ALL DIMENSIONS TO BE READ NOT MEASURED

LEGENDS

KEY PLAN

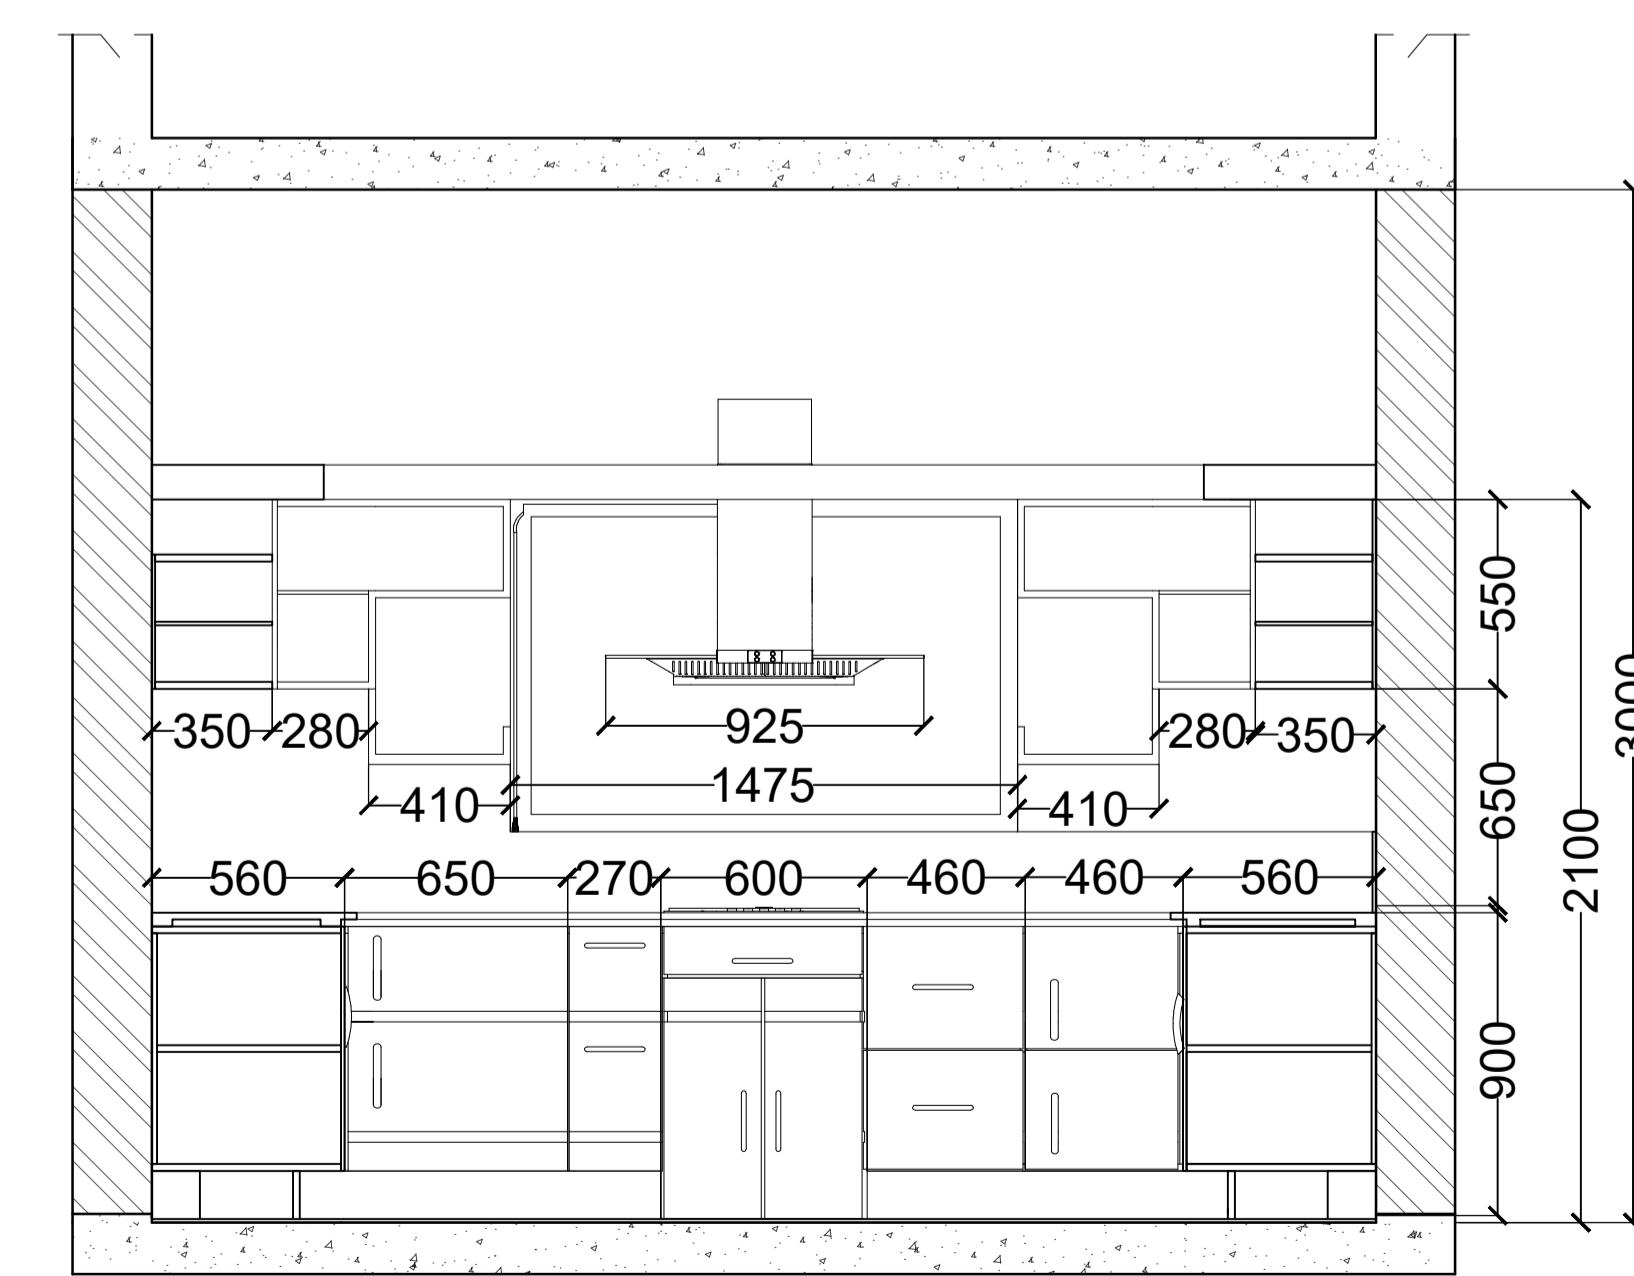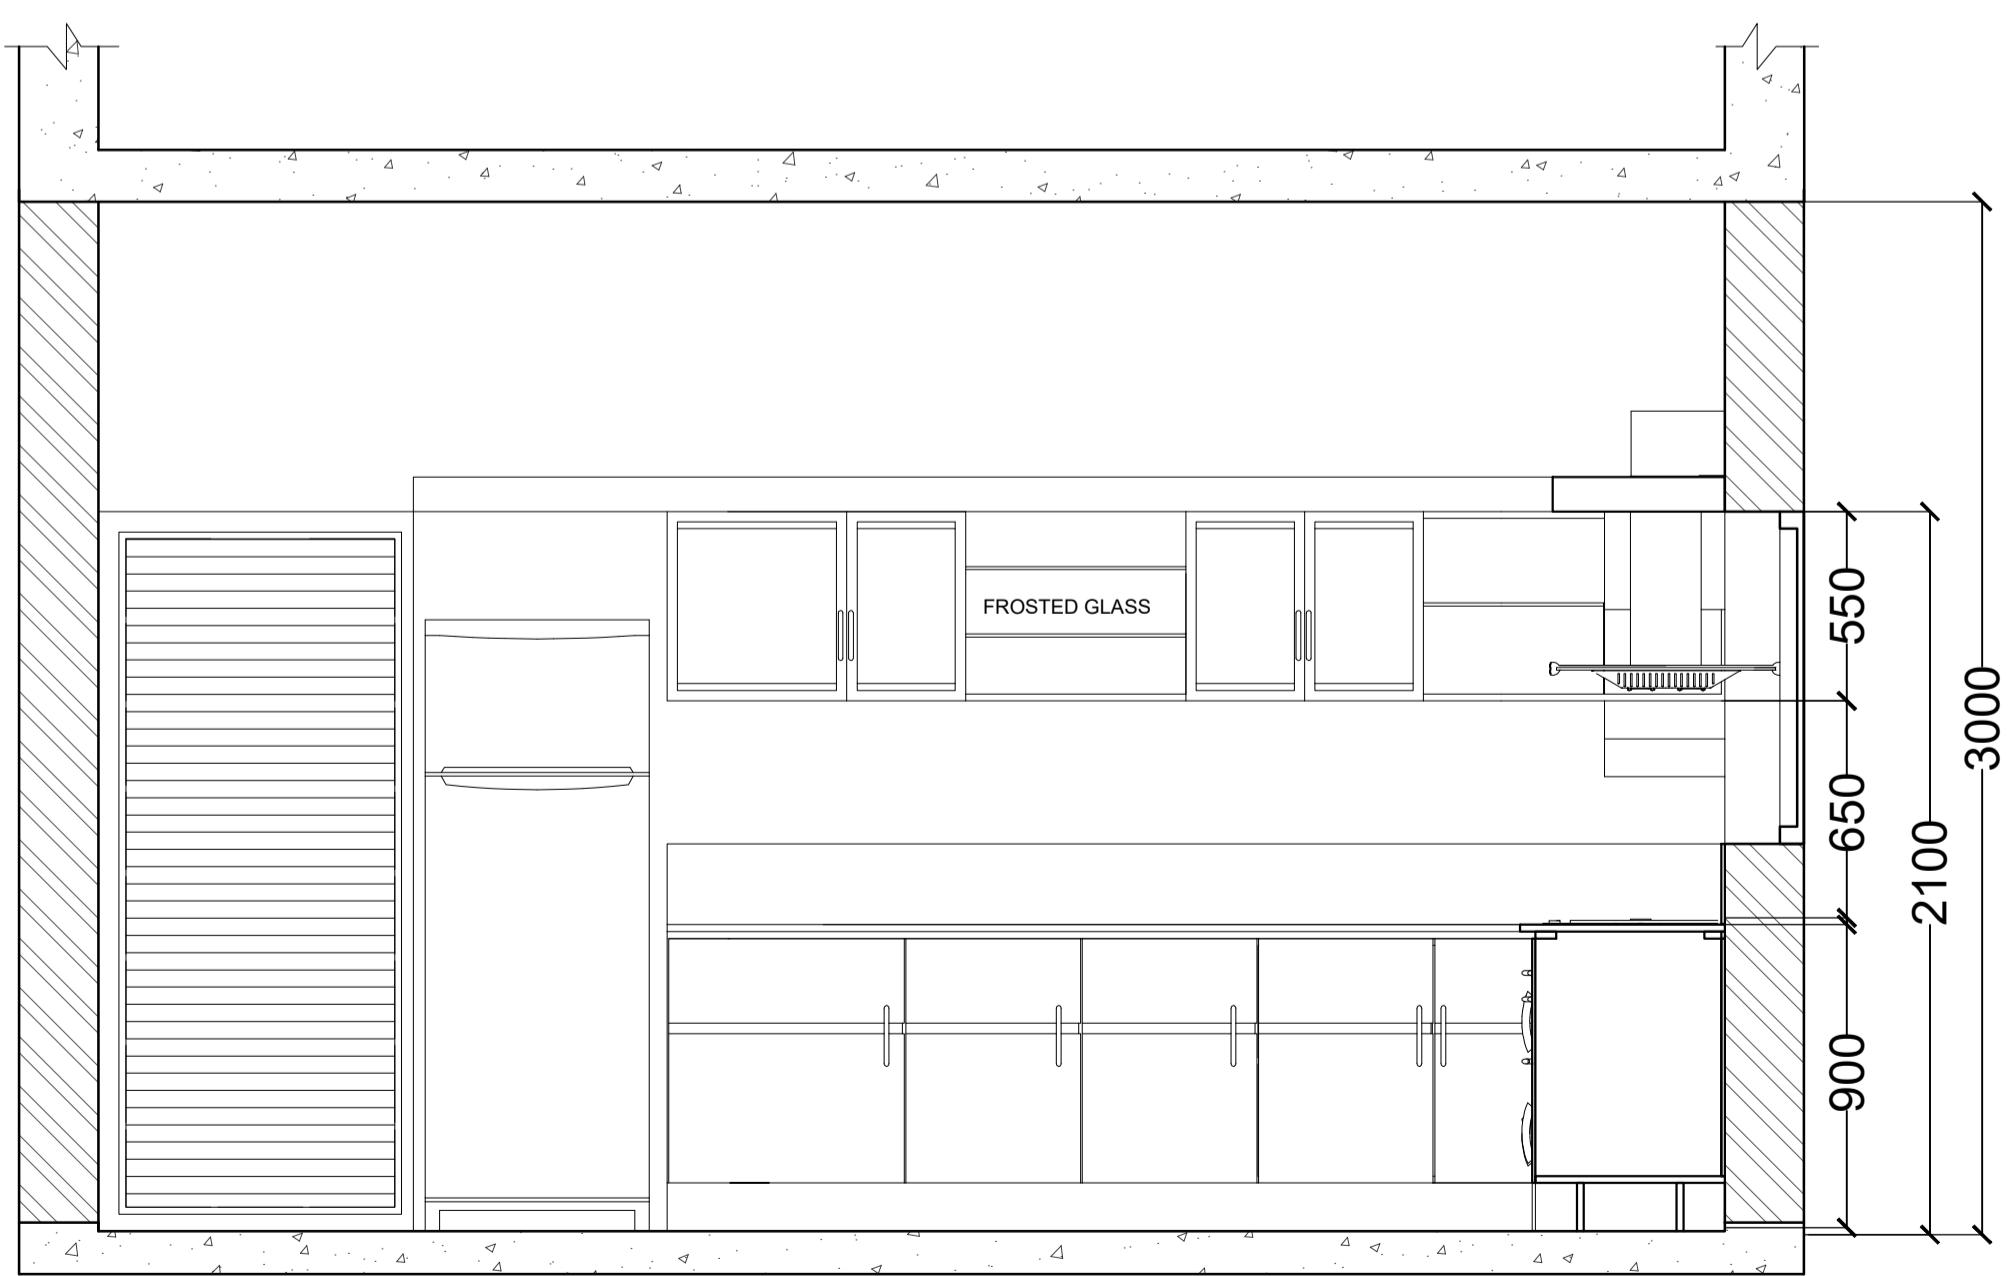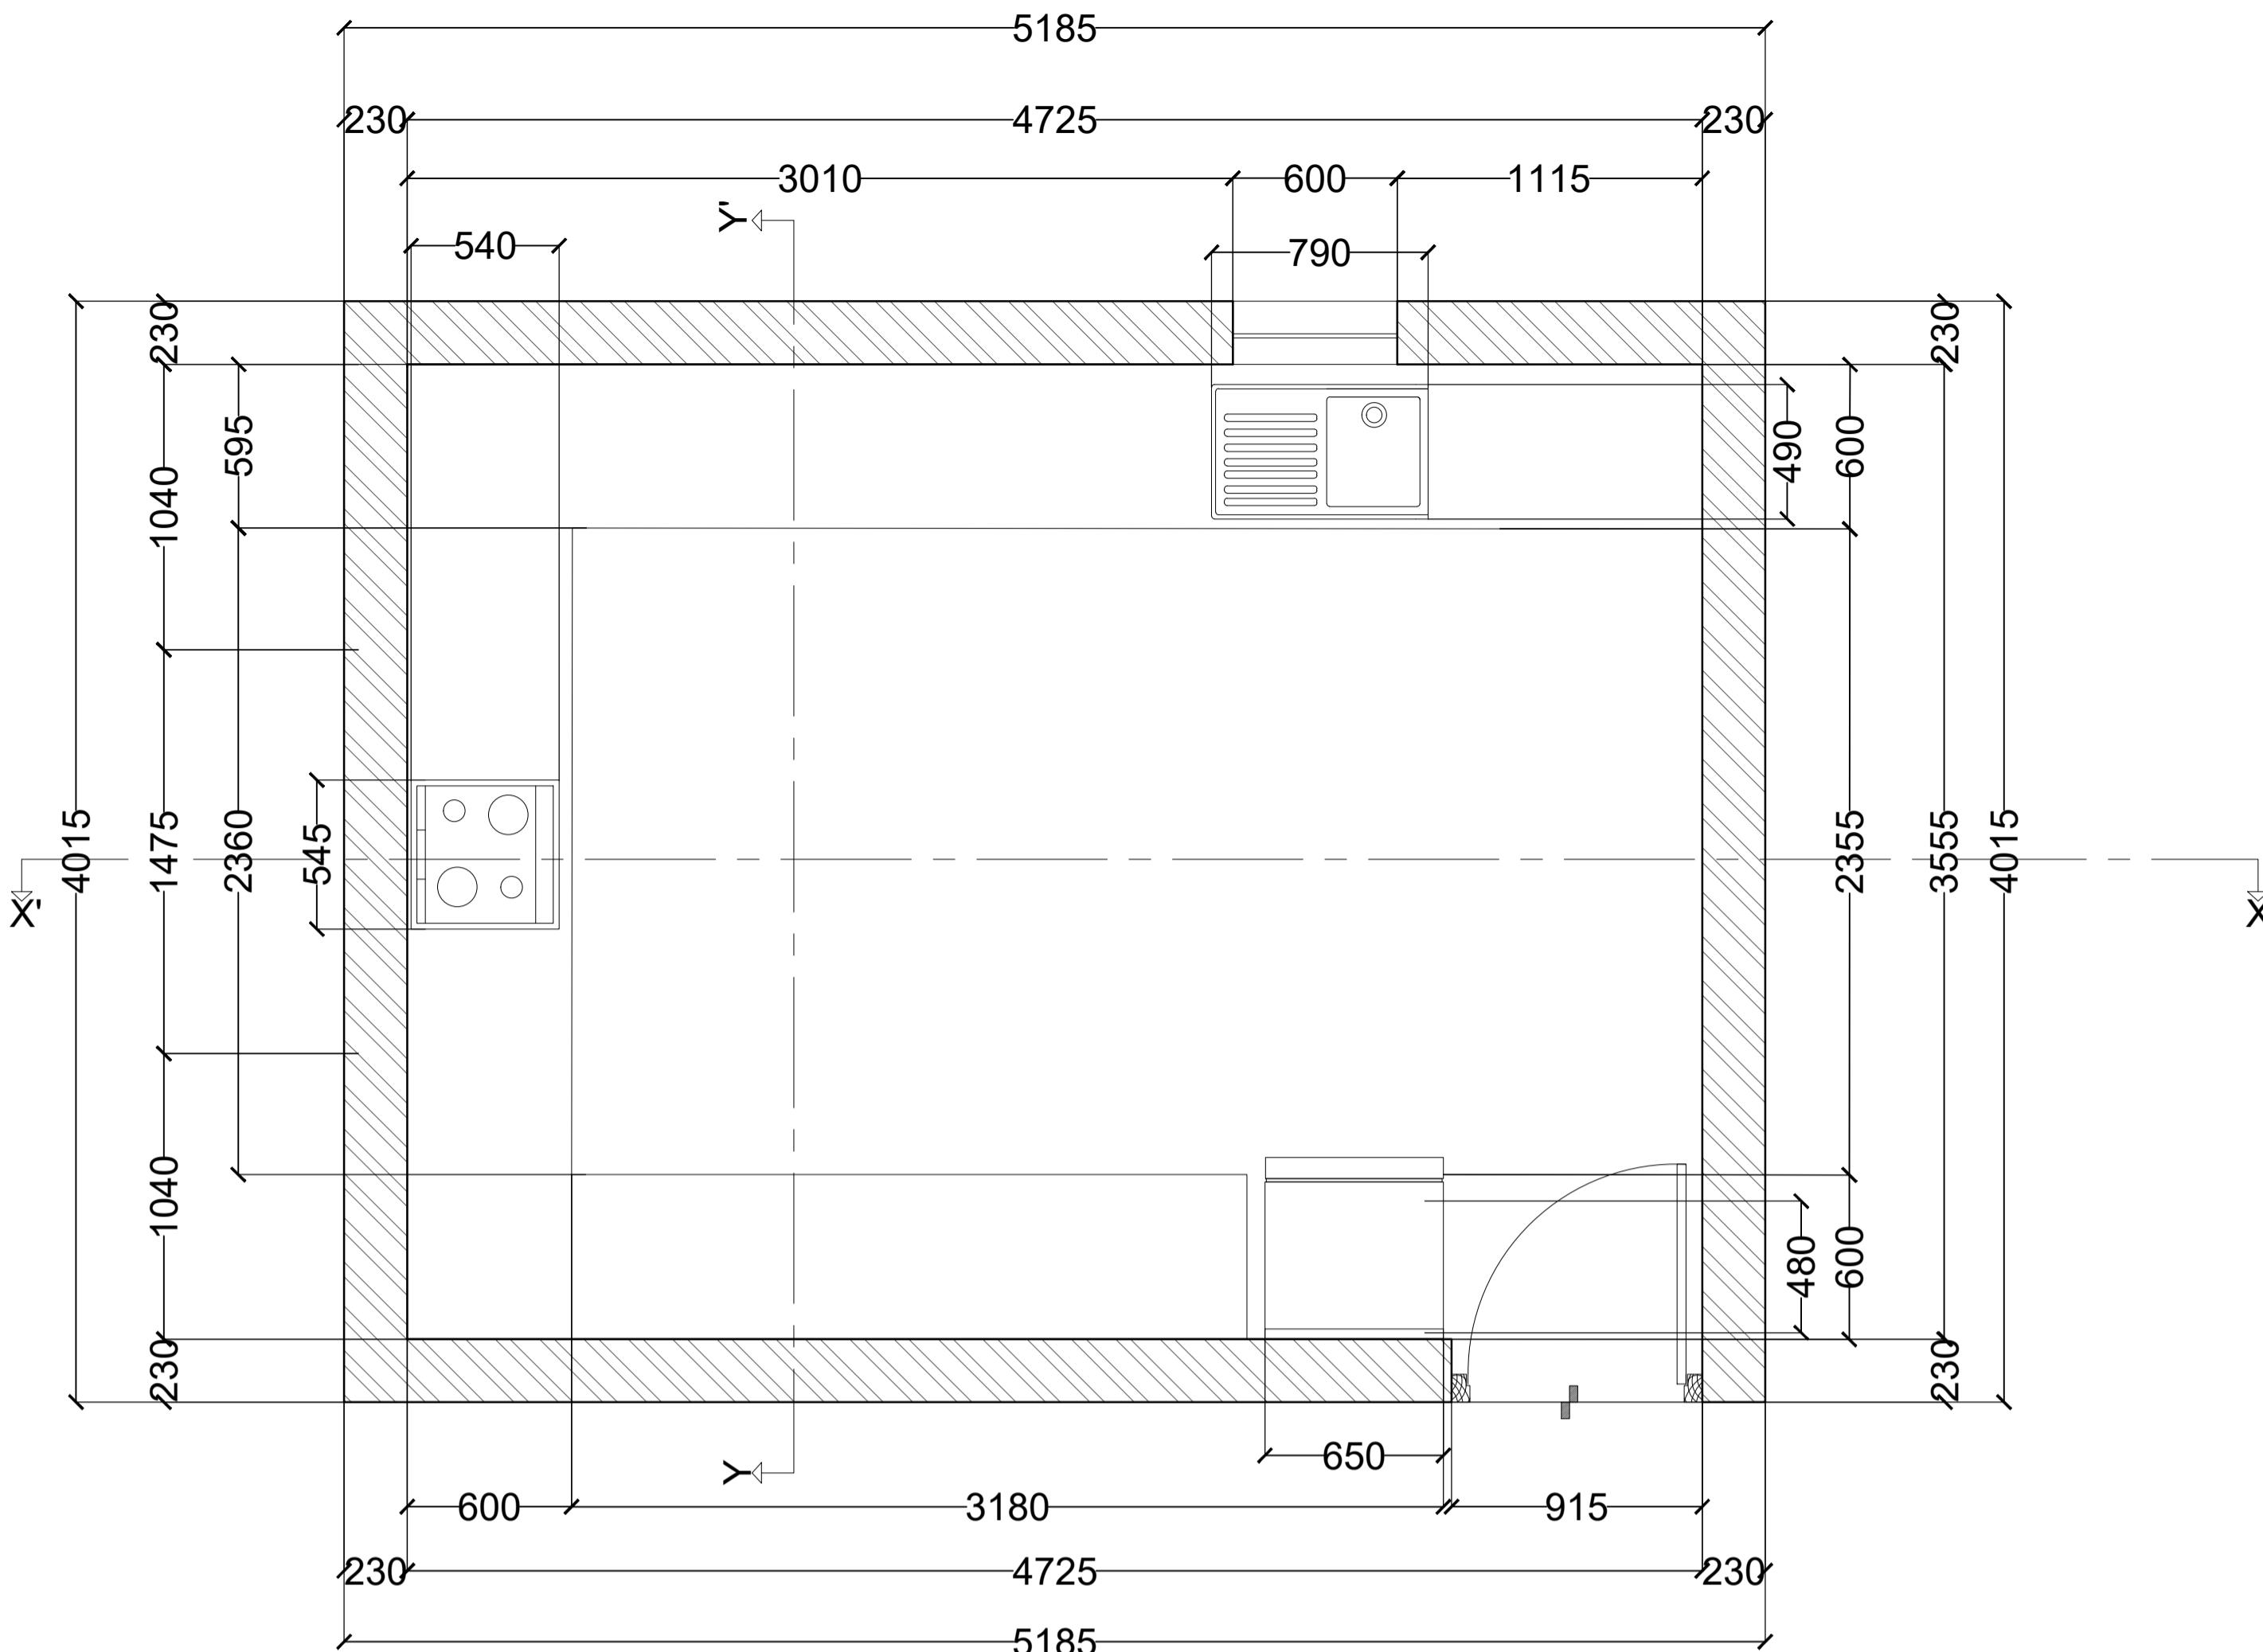

SHEET TITLE
RESIDENCE KITCHEN DETAIL

SHEET NO.: 17A
SCALE : 1 : 20



PROJECT
HOSTEL WORKING DRW.

DRAWN BY YASH VARDHAN	CHECKED BY
--------------------------	------------

UID-SOA


NOTES

ALL DIMENSIONS ARE IN MM
ALL DIMENSIONS TO BE READ NOT MEASURED


LEGENDS

- L


KEY PLAN

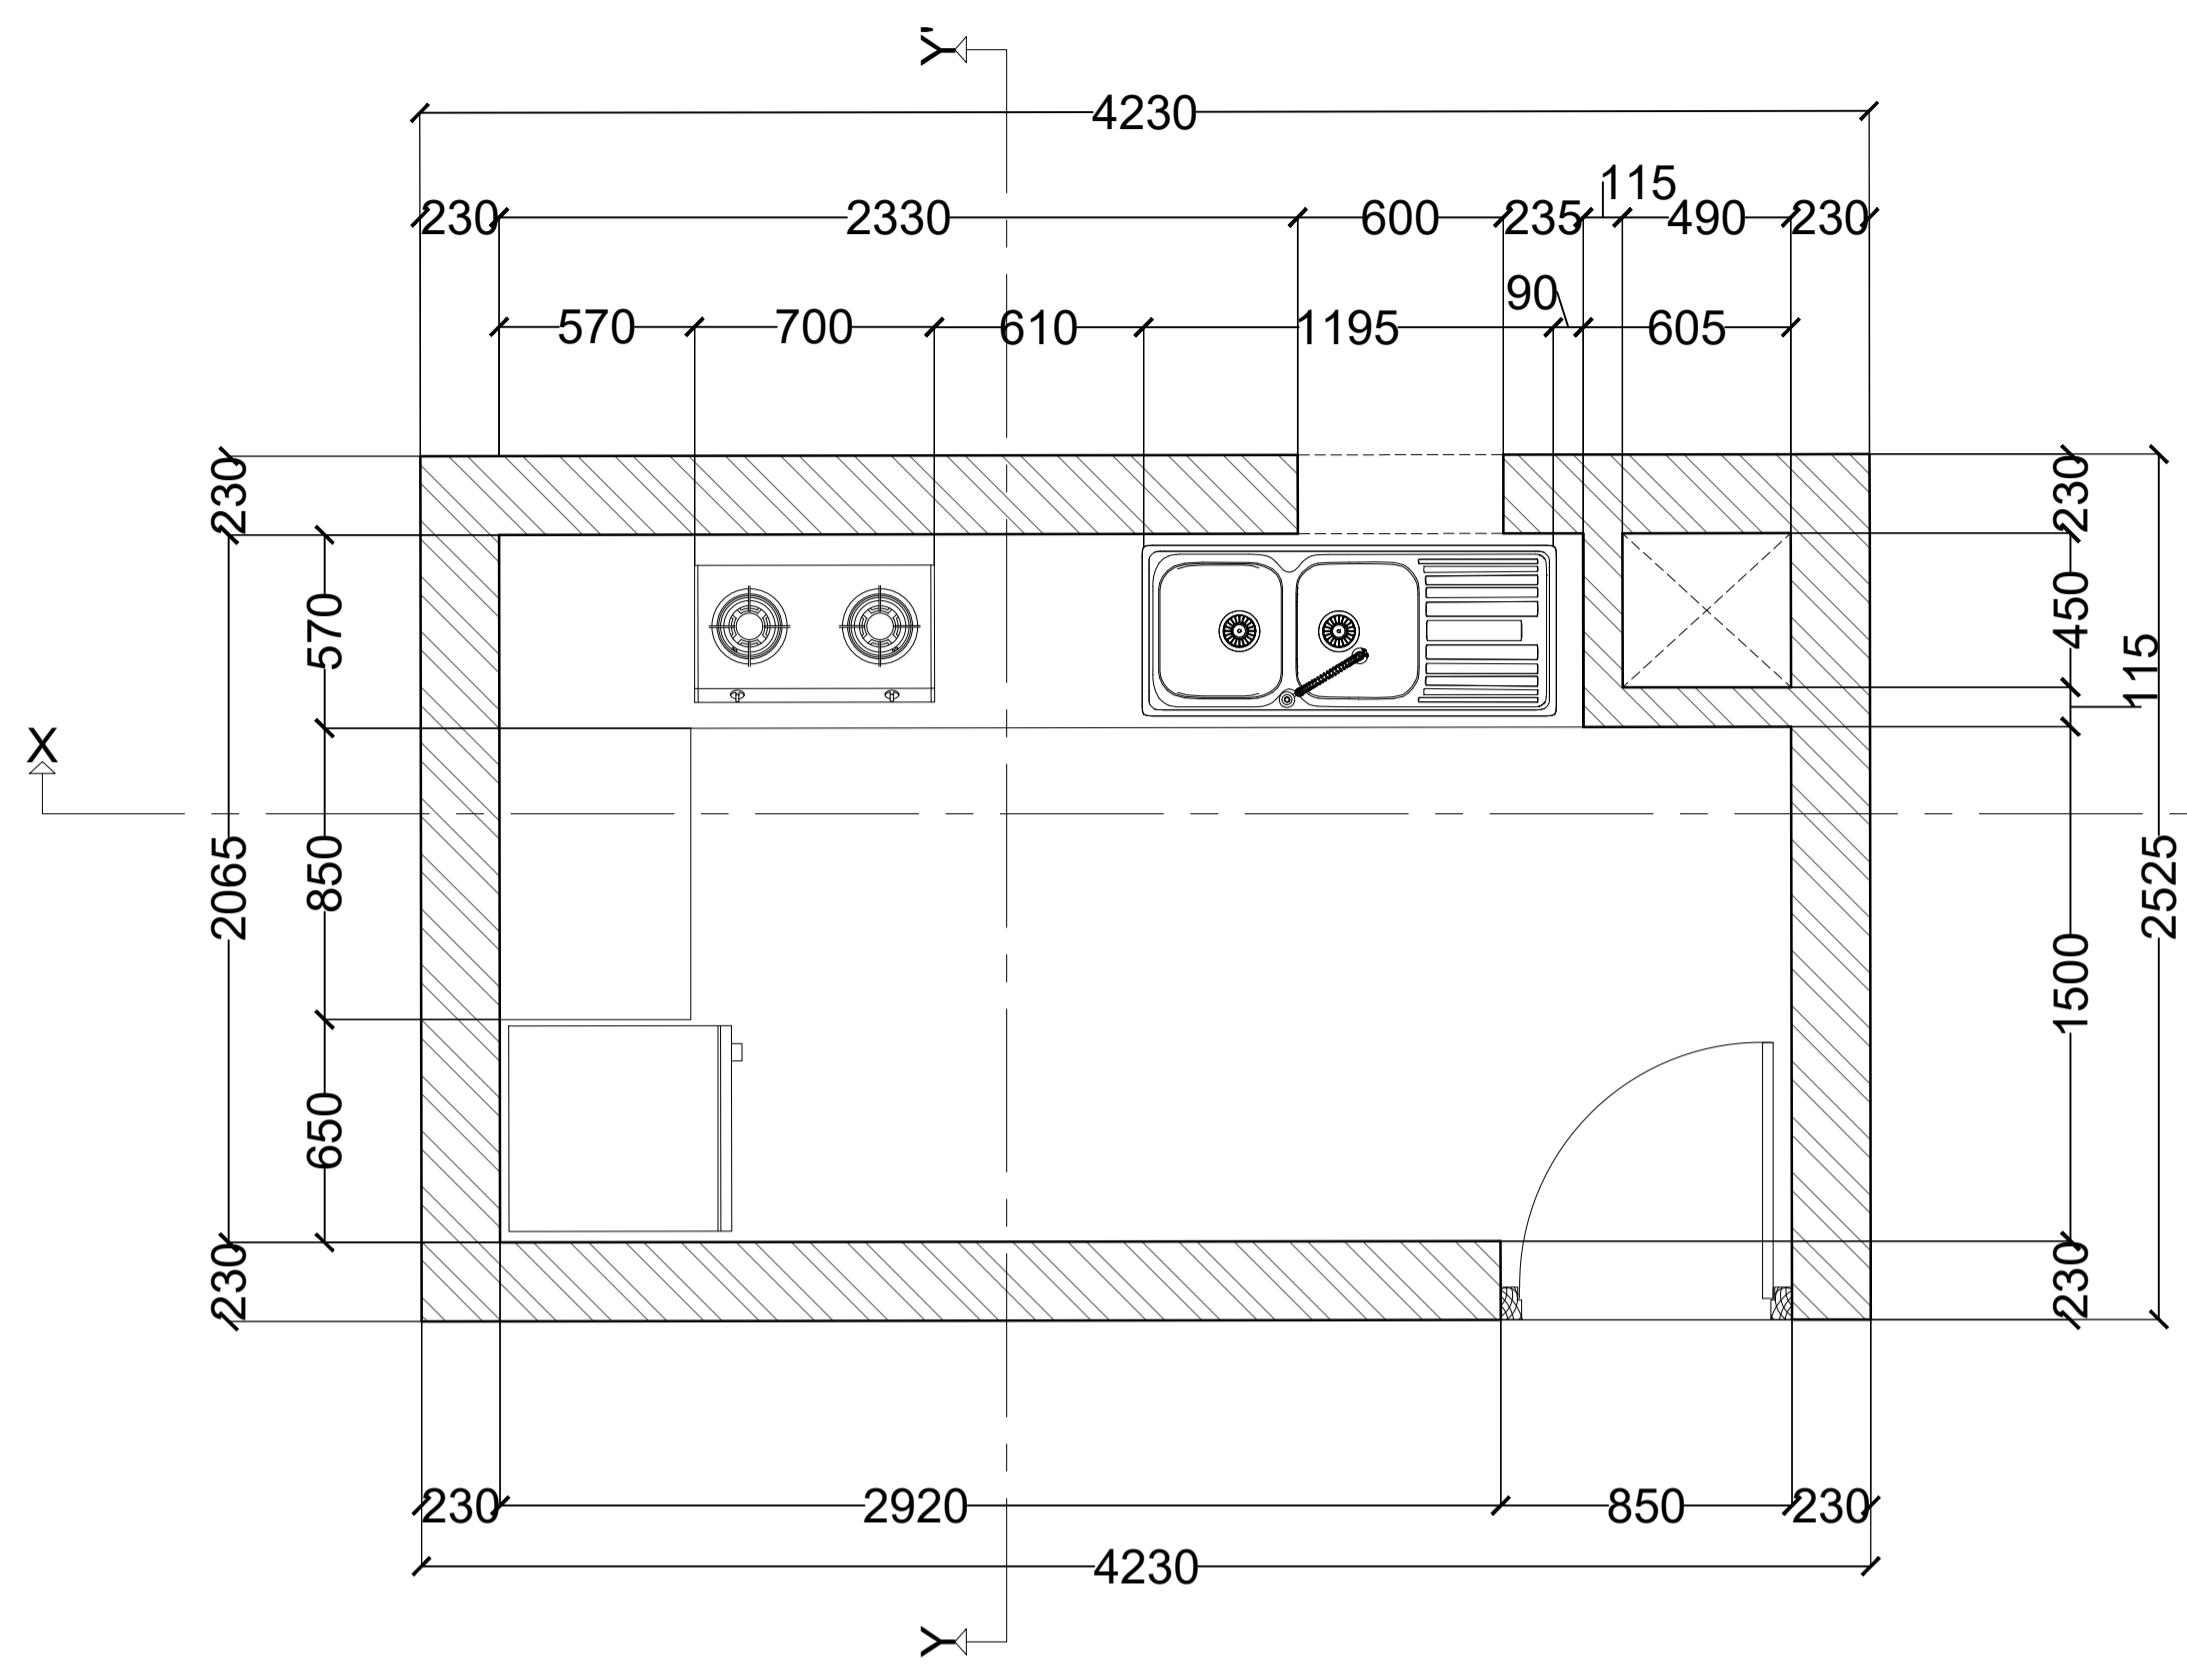


COUNTER LEVEL PLAN

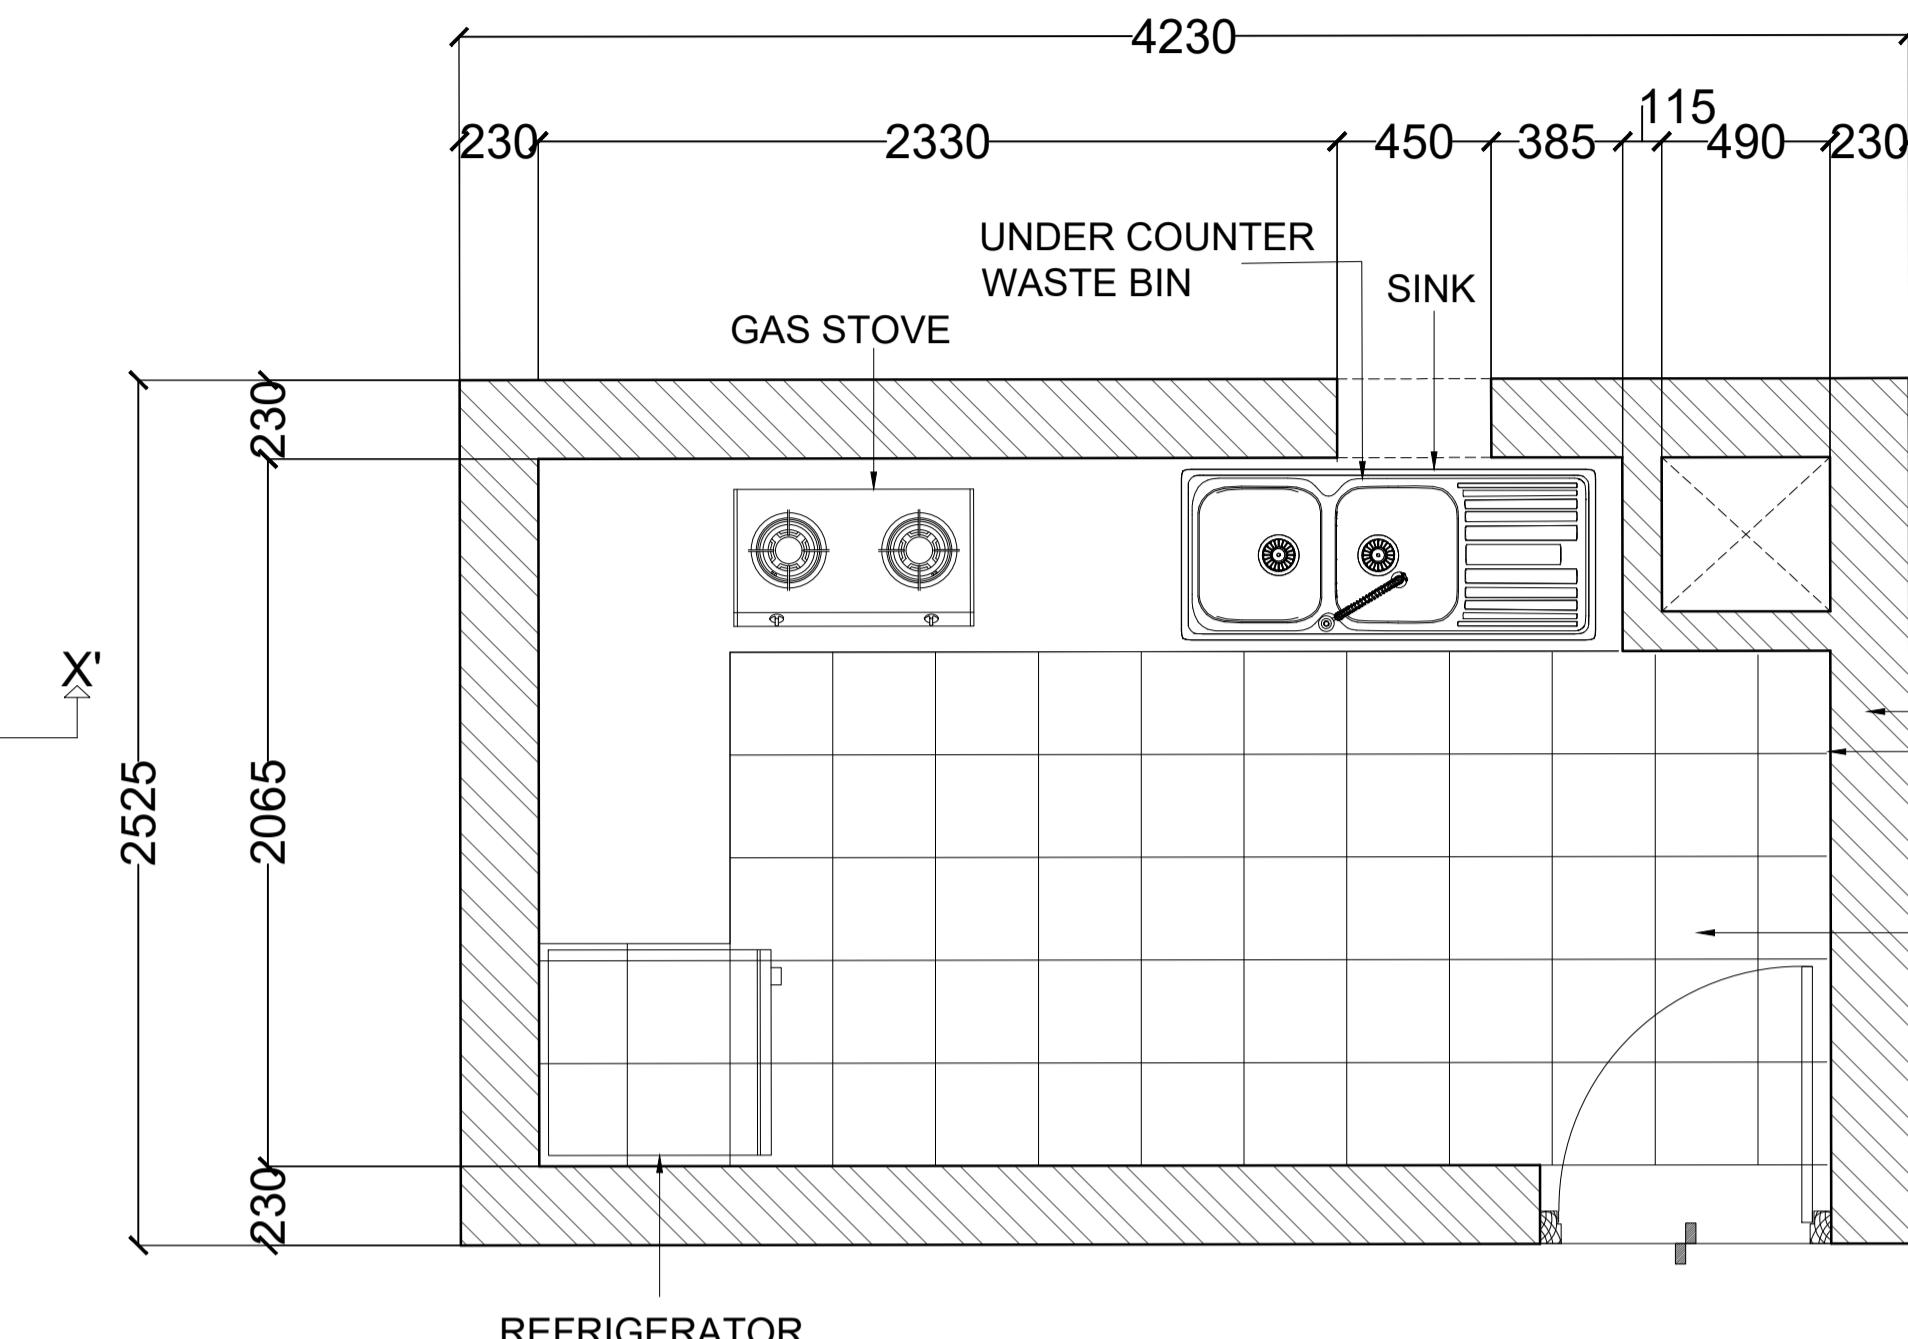

FLOORING PLAN

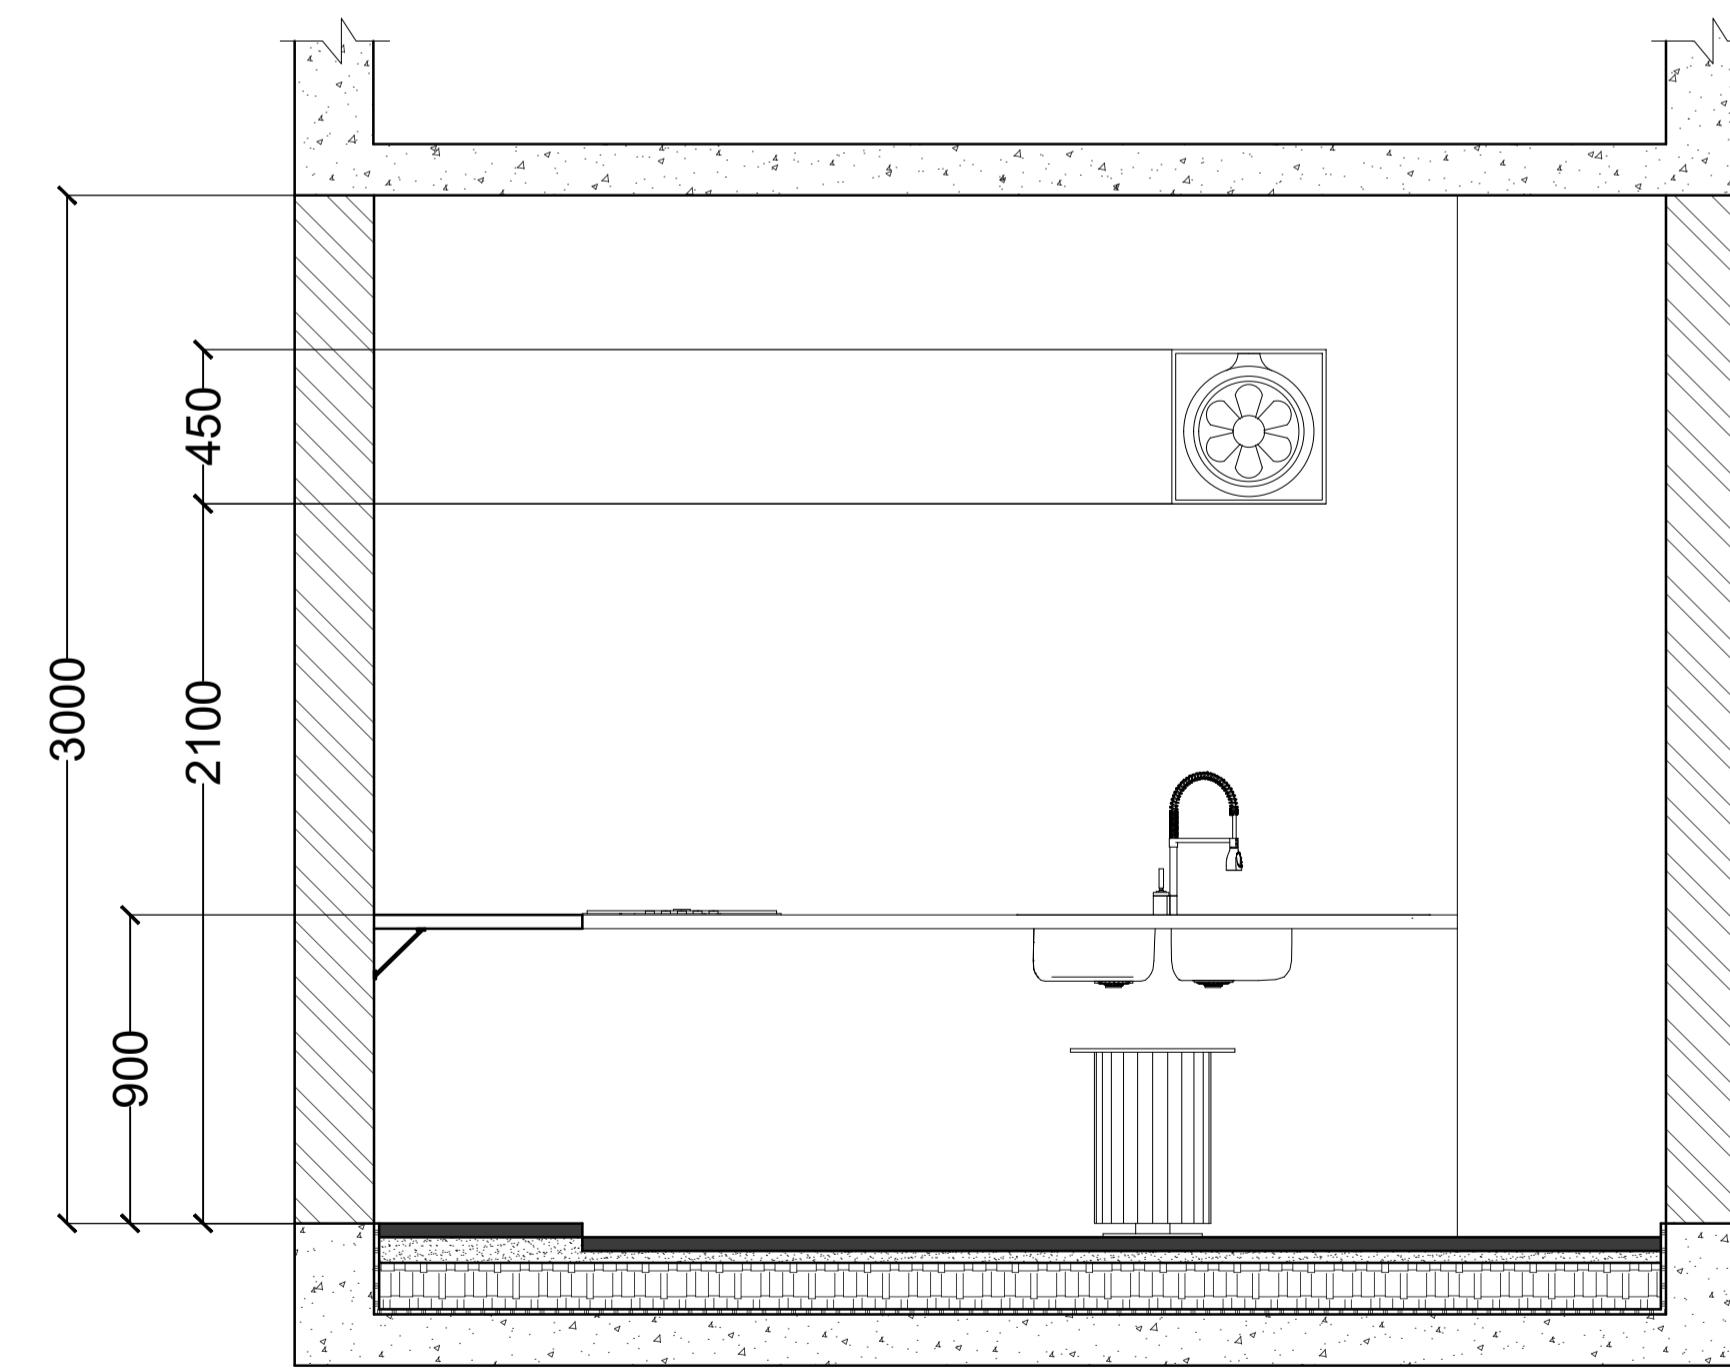

SECTION XX

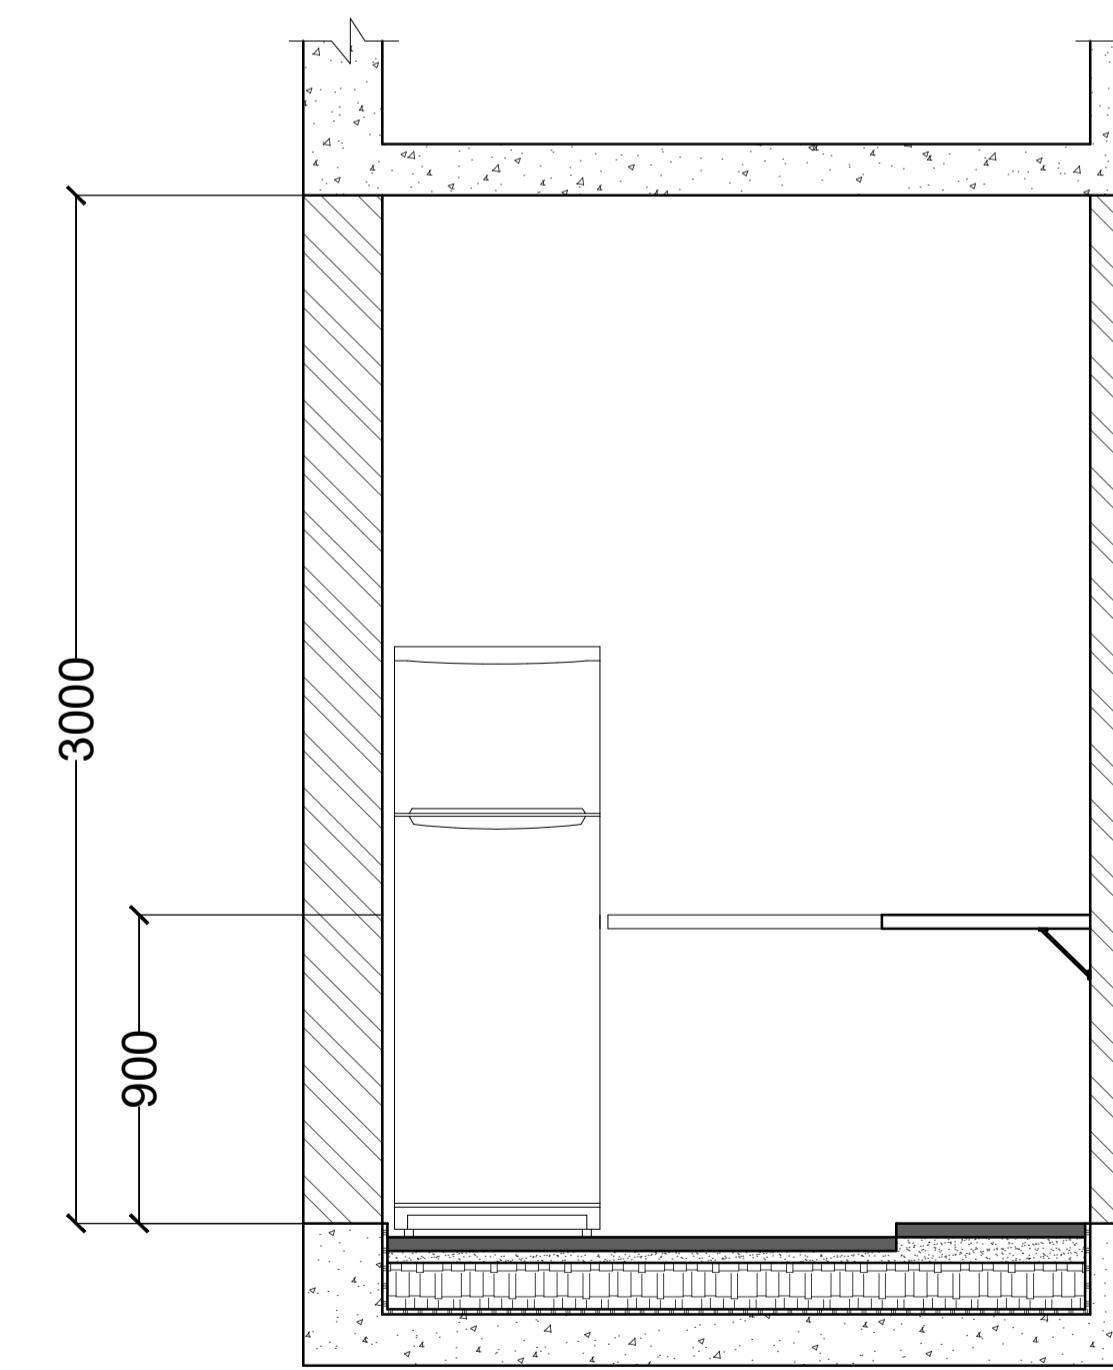

SECTION YY'

SHEET TITLE

KITCHEN DETAIL

SHEET NO. : 18
SCALE : 1 :20


PROJECT HOSTEL WORKING DRW.

DRAWN BY	CHECKED BY
YASH VARDHAN	


UID-SOA

NOTES


ALL DIMENSIONS ARE IN MM
ALL DIMENSIONS TO BE READ NOT MEASURED

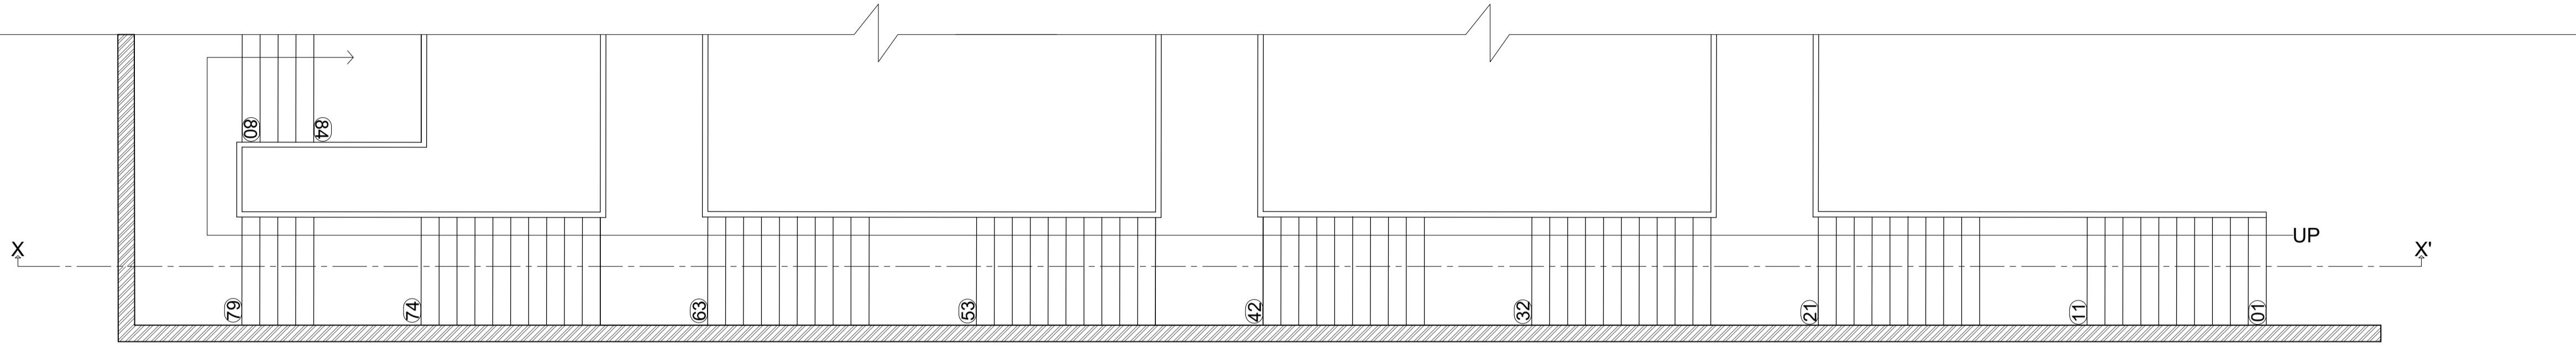

LEGENDS

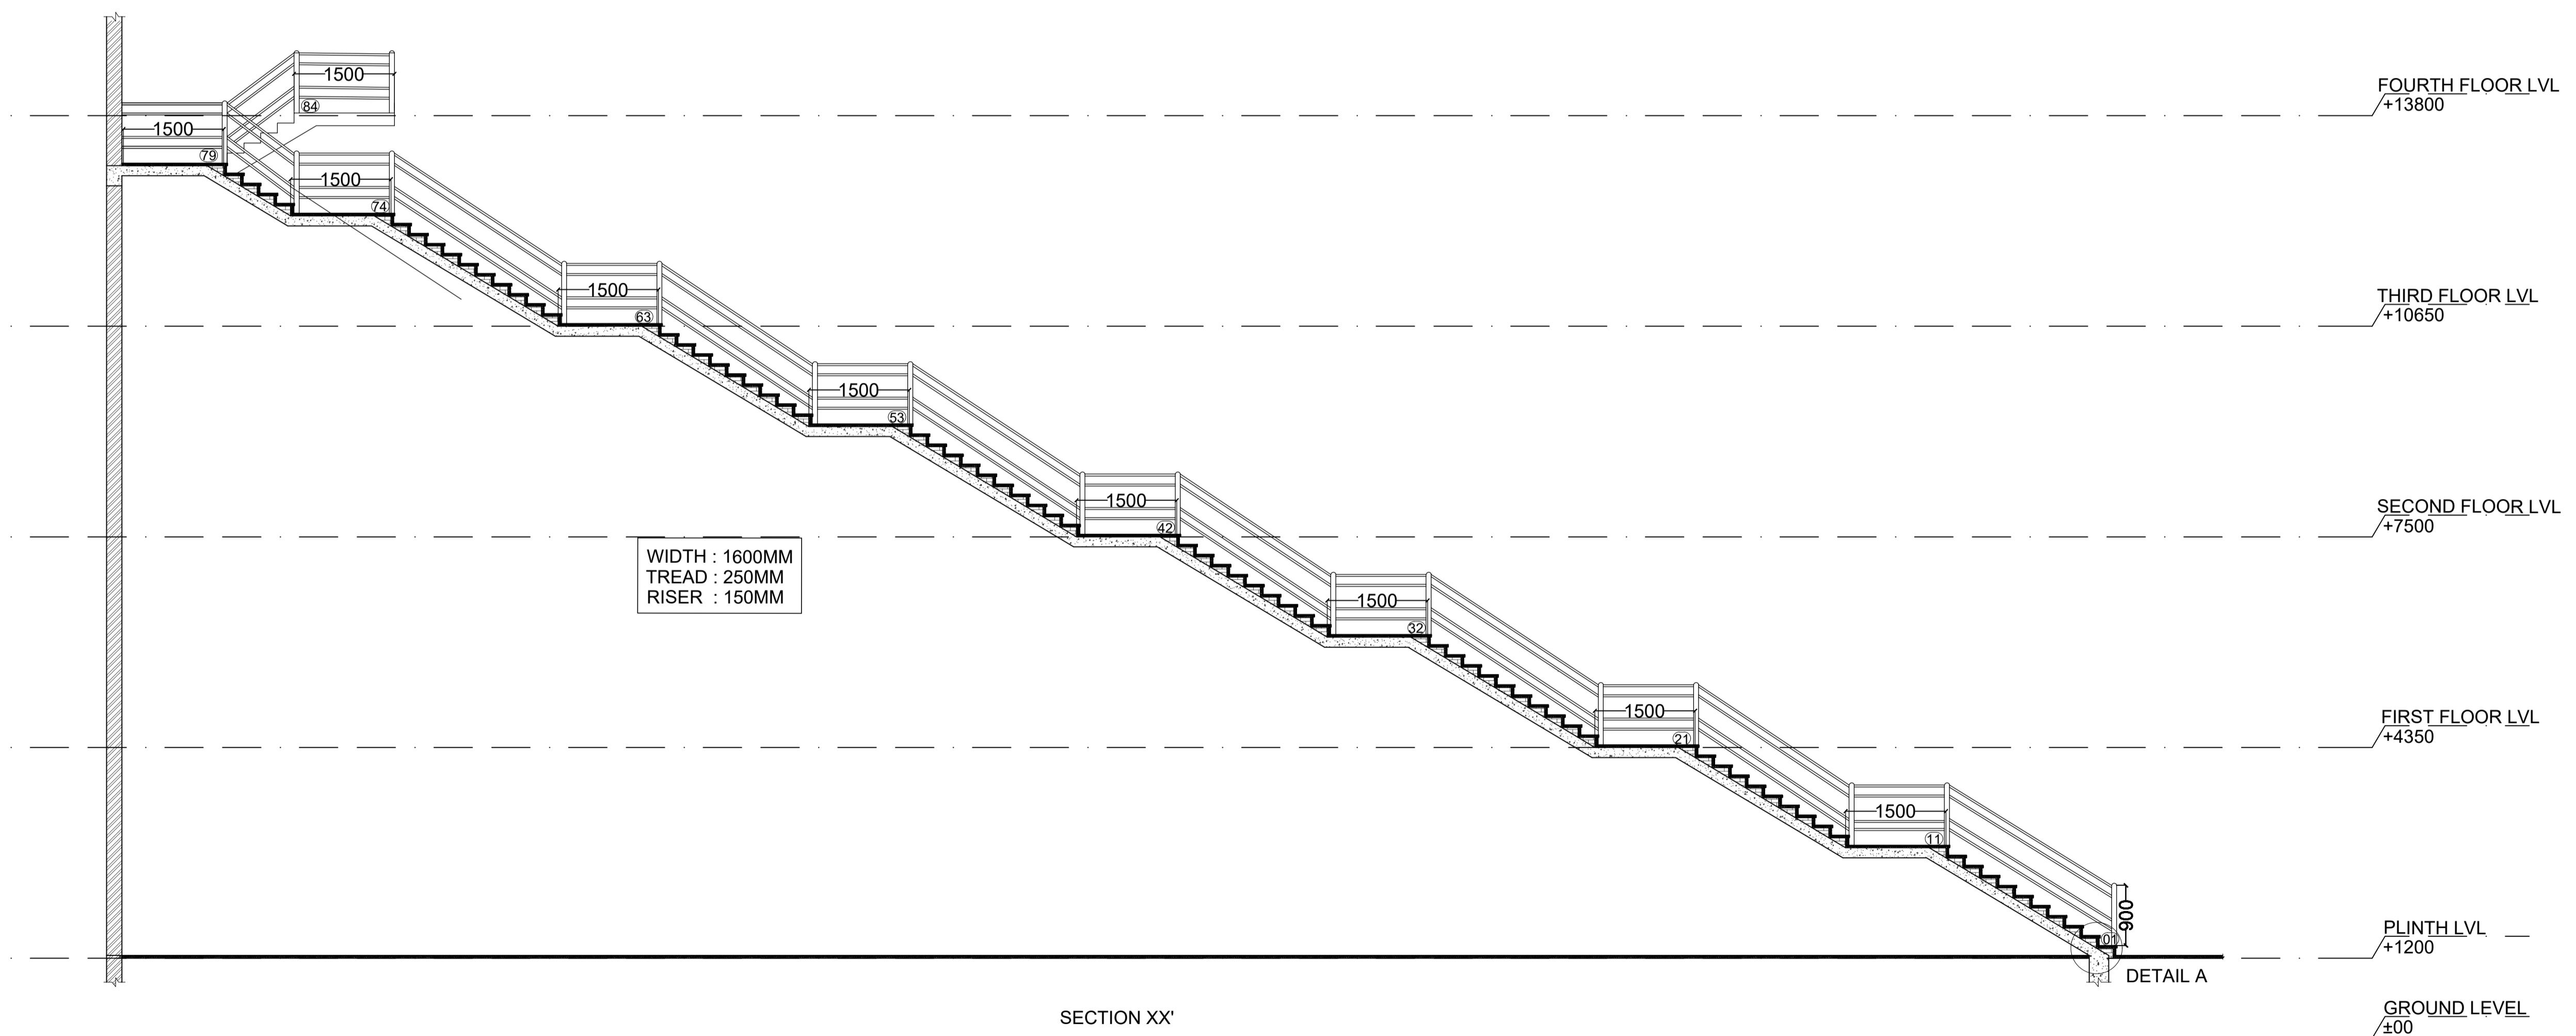

SECTION XX'

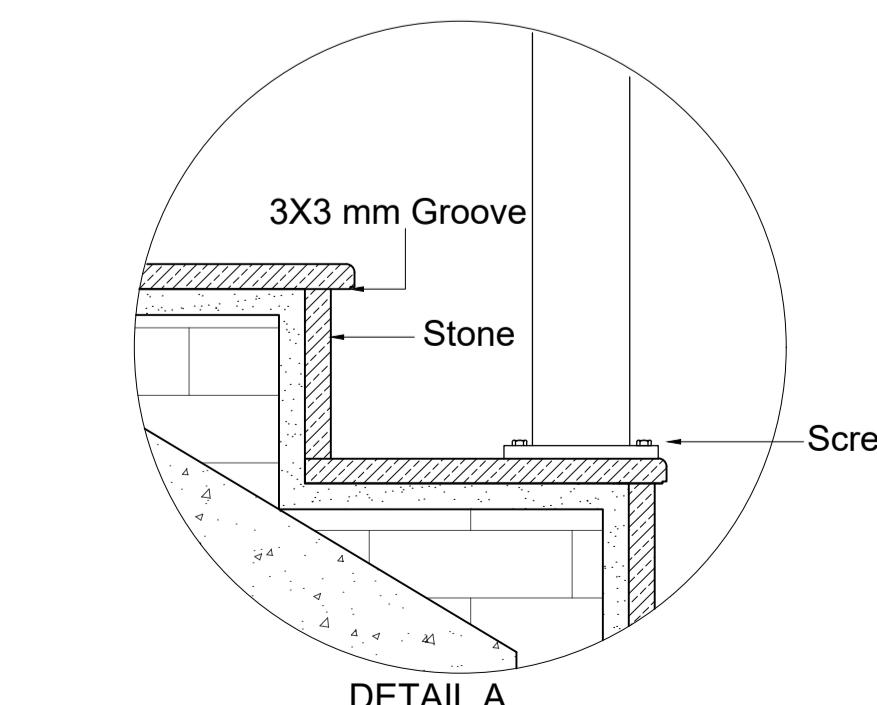

SHEET TITLE

STAIRCASE DETAIL

SHEET NO. : 19

SCALE : 1 : 50

PROJECT
HOSTEL WORKING DRW.

DRAWN BY
YASH VARDHAN

CHECKED BY