



UID-SOA

HOSTEL DESIGN

VIEWS

SUB. BY: YASH VARDHAN

# DESIGN CONCEPT


H  
I  
G  
H  
L  
I  
G  
H  
T  
S

HOSTELS THUS SERVE AS FIT PLATFORMS FOR BRINGING TOGETHER CHILDREN FROM DIFFERENT BACKGROUNDS AND GIVING THEM AN OPPORTUNITY TO INTERACT WITH EACH OTHER, AND LEARN ABOUT CULTURES OTHER THAN THEIR OWN.

EXISTING HOSTEL BLOCKS ONLY HAVE MECHANICAL VENTILATION AND HAVE NO INTERACTION SPACE

OUR PROPOSED DESIGN WOULD HAVE COMMON SPACES WHICH MAKES UP 50% OF THE PRIVATE SPACES


## DESIGN CONCEPT : THREE WINGS

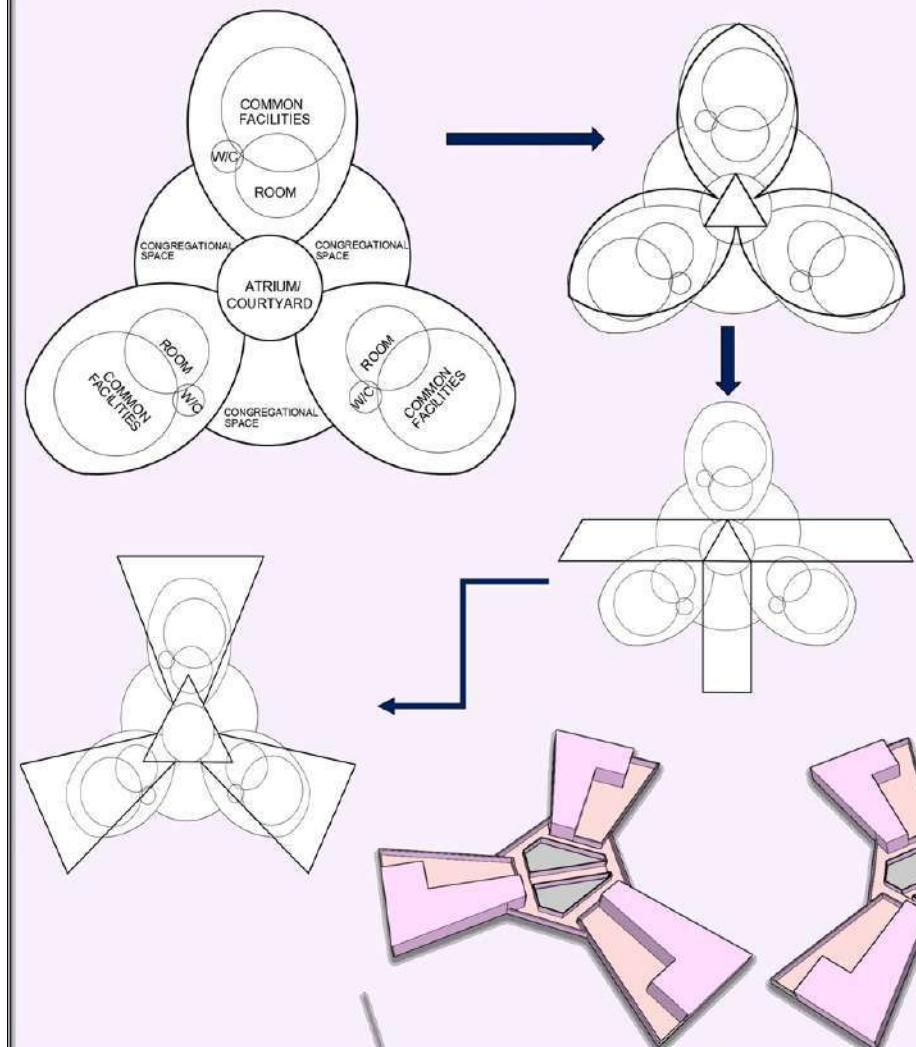

ATRIUM WITH CONNECTING BRIDGES






TAKE AWAY THE LONG CORRIDORS  
CENTRALIZED COMMON SPACE

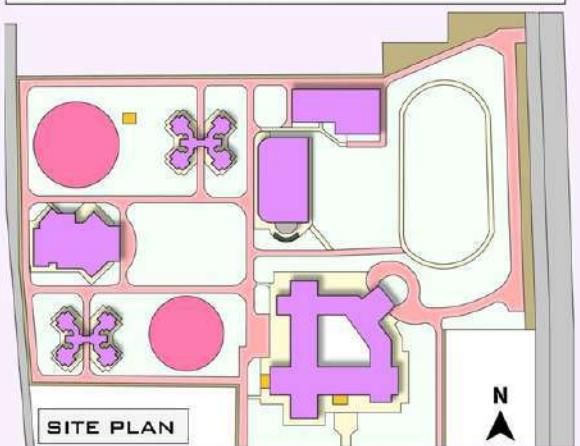


SITE PLAN

EXISTING BLOCKS  
VEHICULAR MOVEMENT

PROPOSED HOSTEL BLOCKS  
PEDESTRIAN MOVEMENT

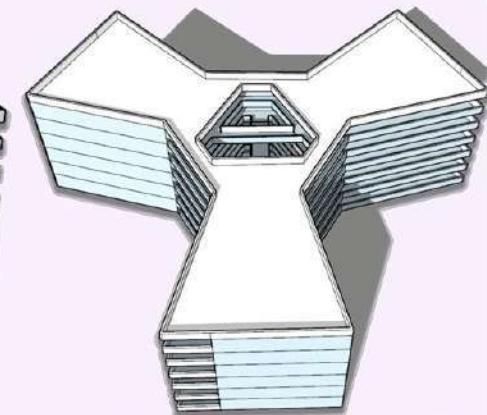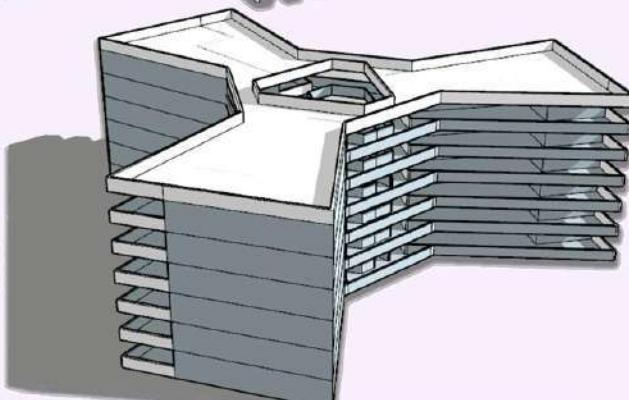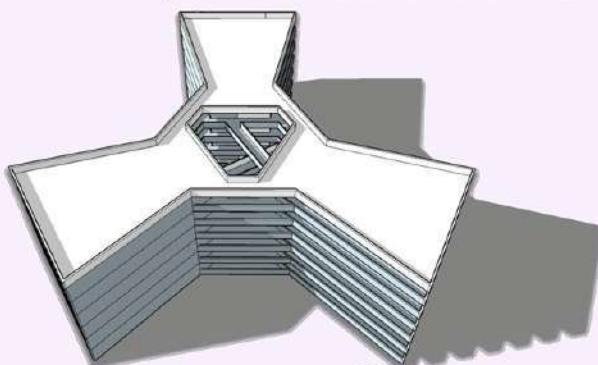

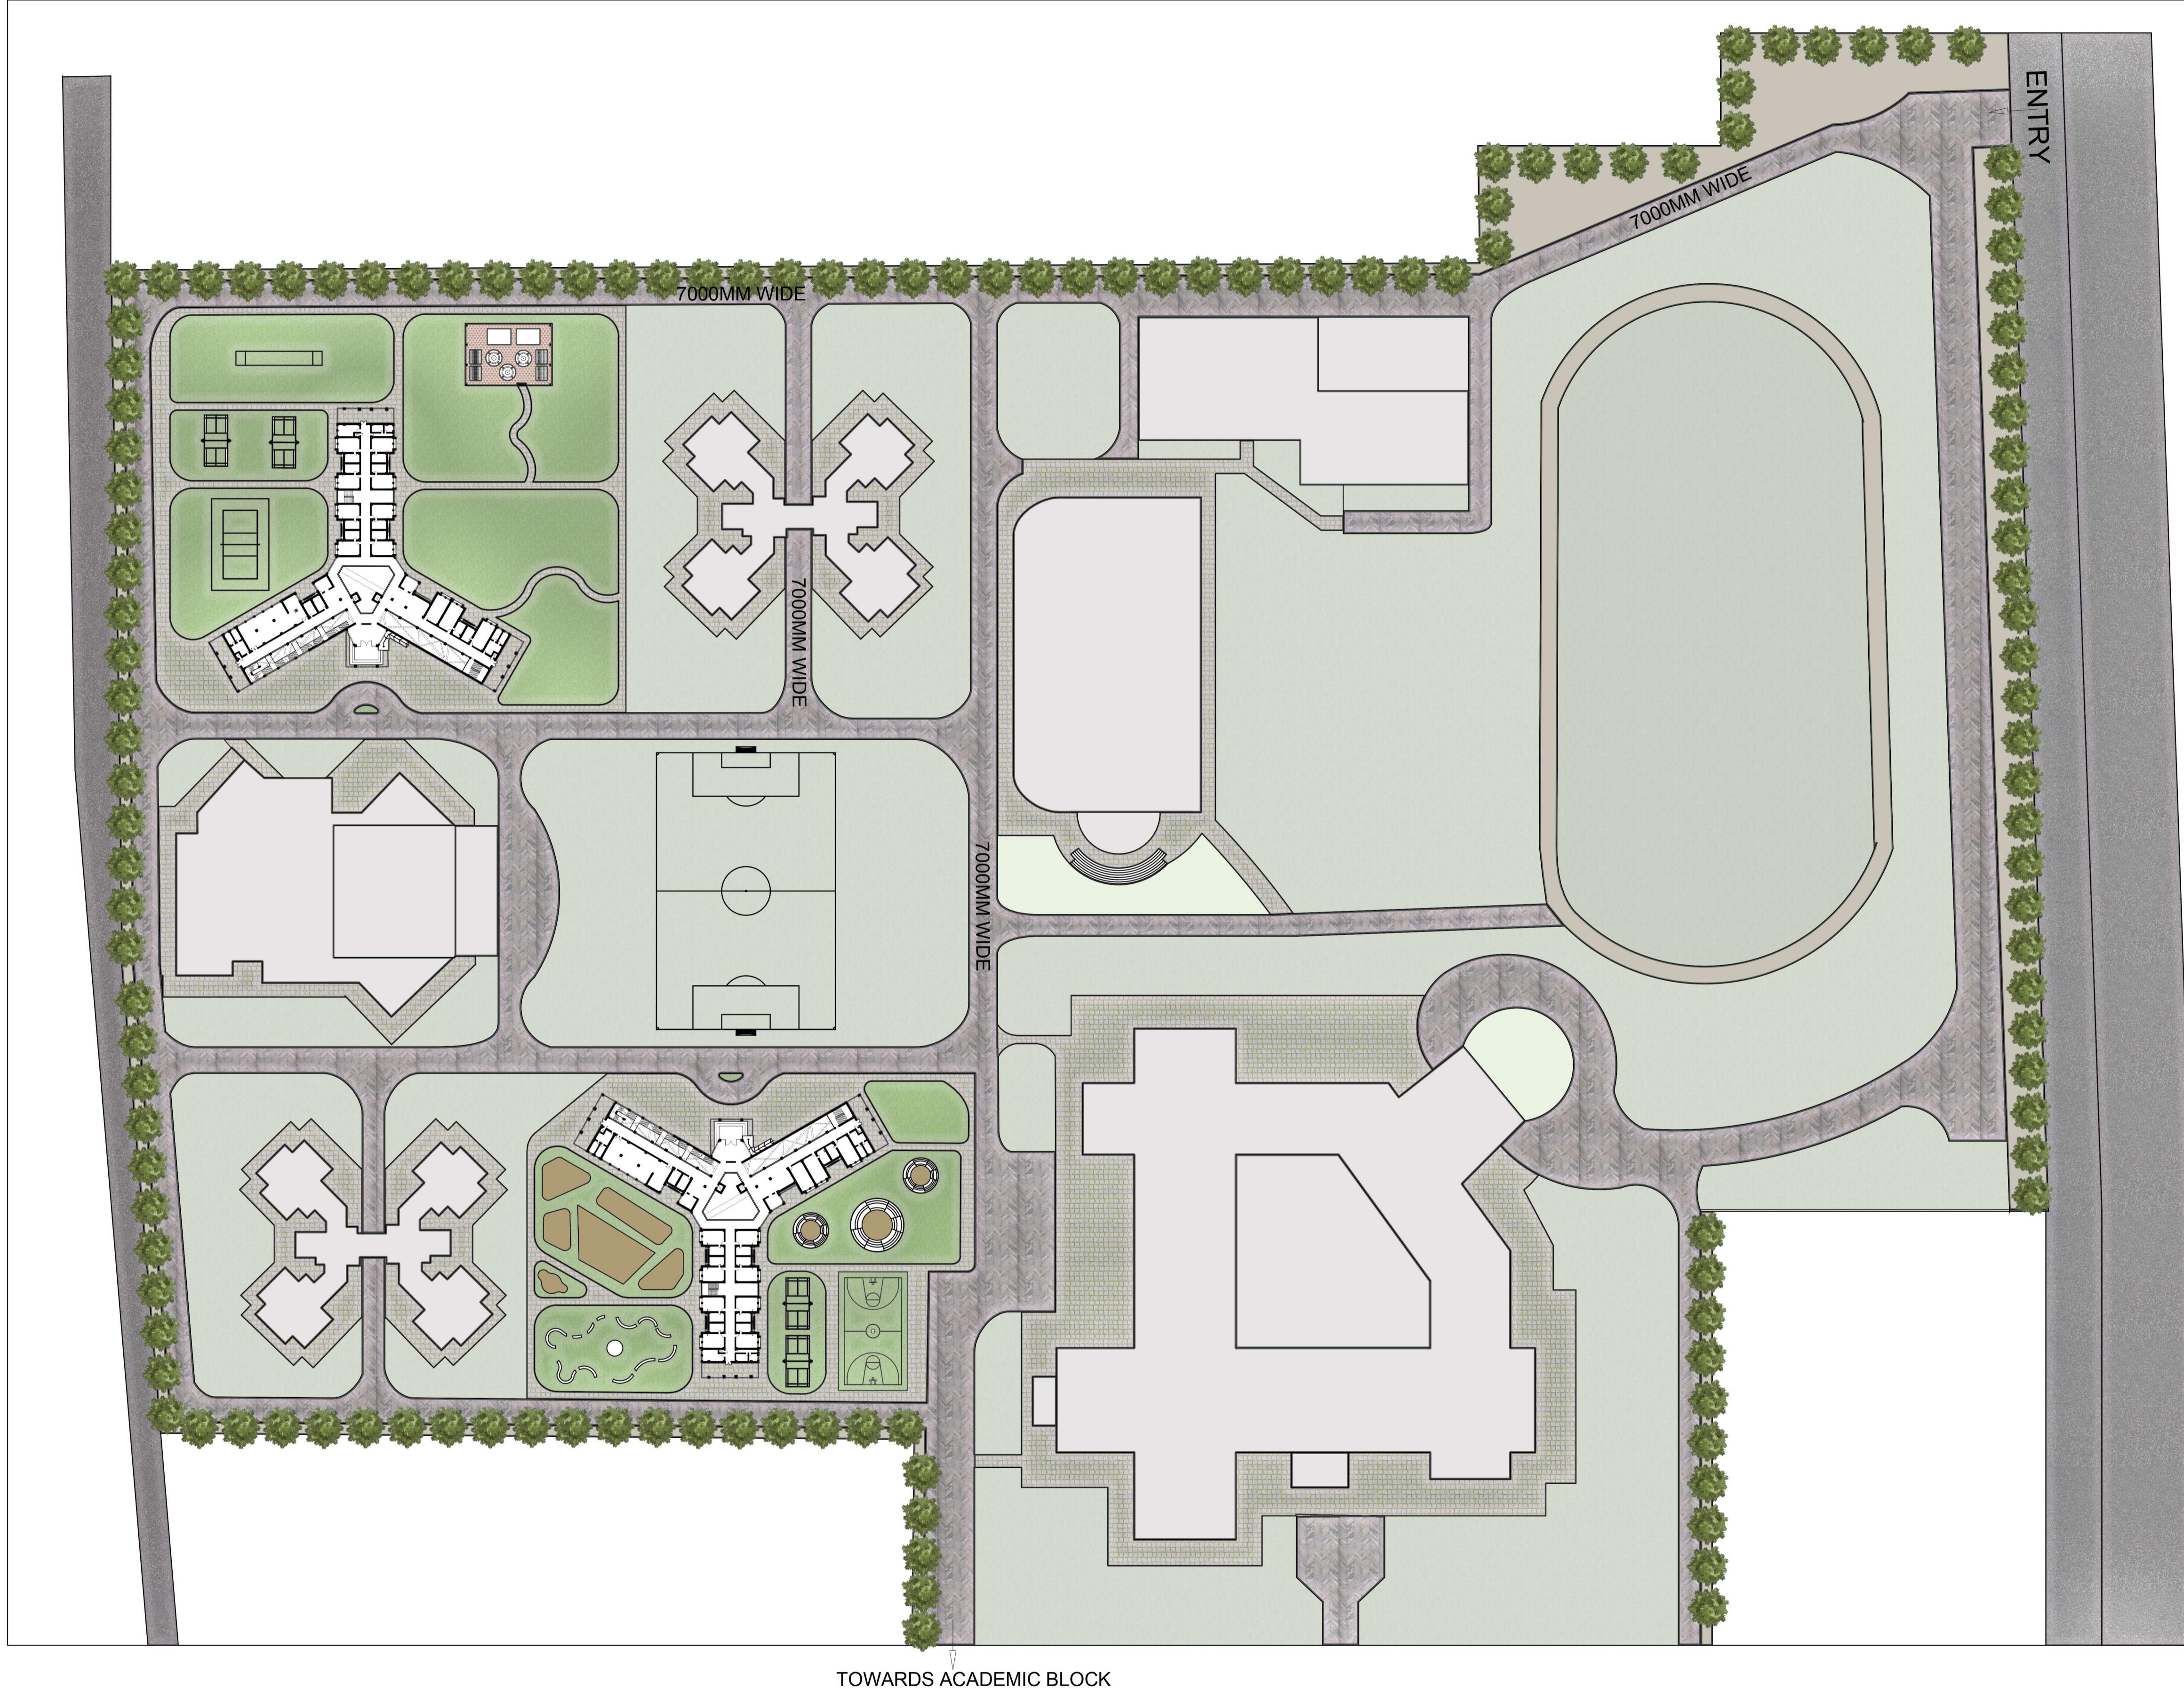

PROJECT TITLE- HOSTEL DESIGN

DATE- 08/12/2022

DRAWN BY- YASH VARDHAN


ADMISSION NO.- 20210634


SHEET TITLE- SITE PLAN

SHEET NO.- 01

SUBJECT- DESIGN NARRATIVE-V

SCALE-1:1000

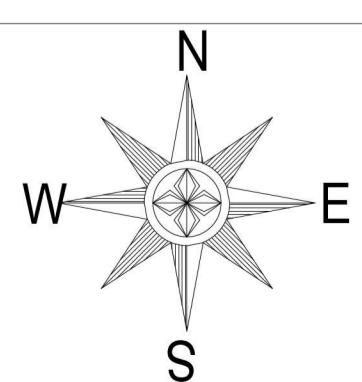

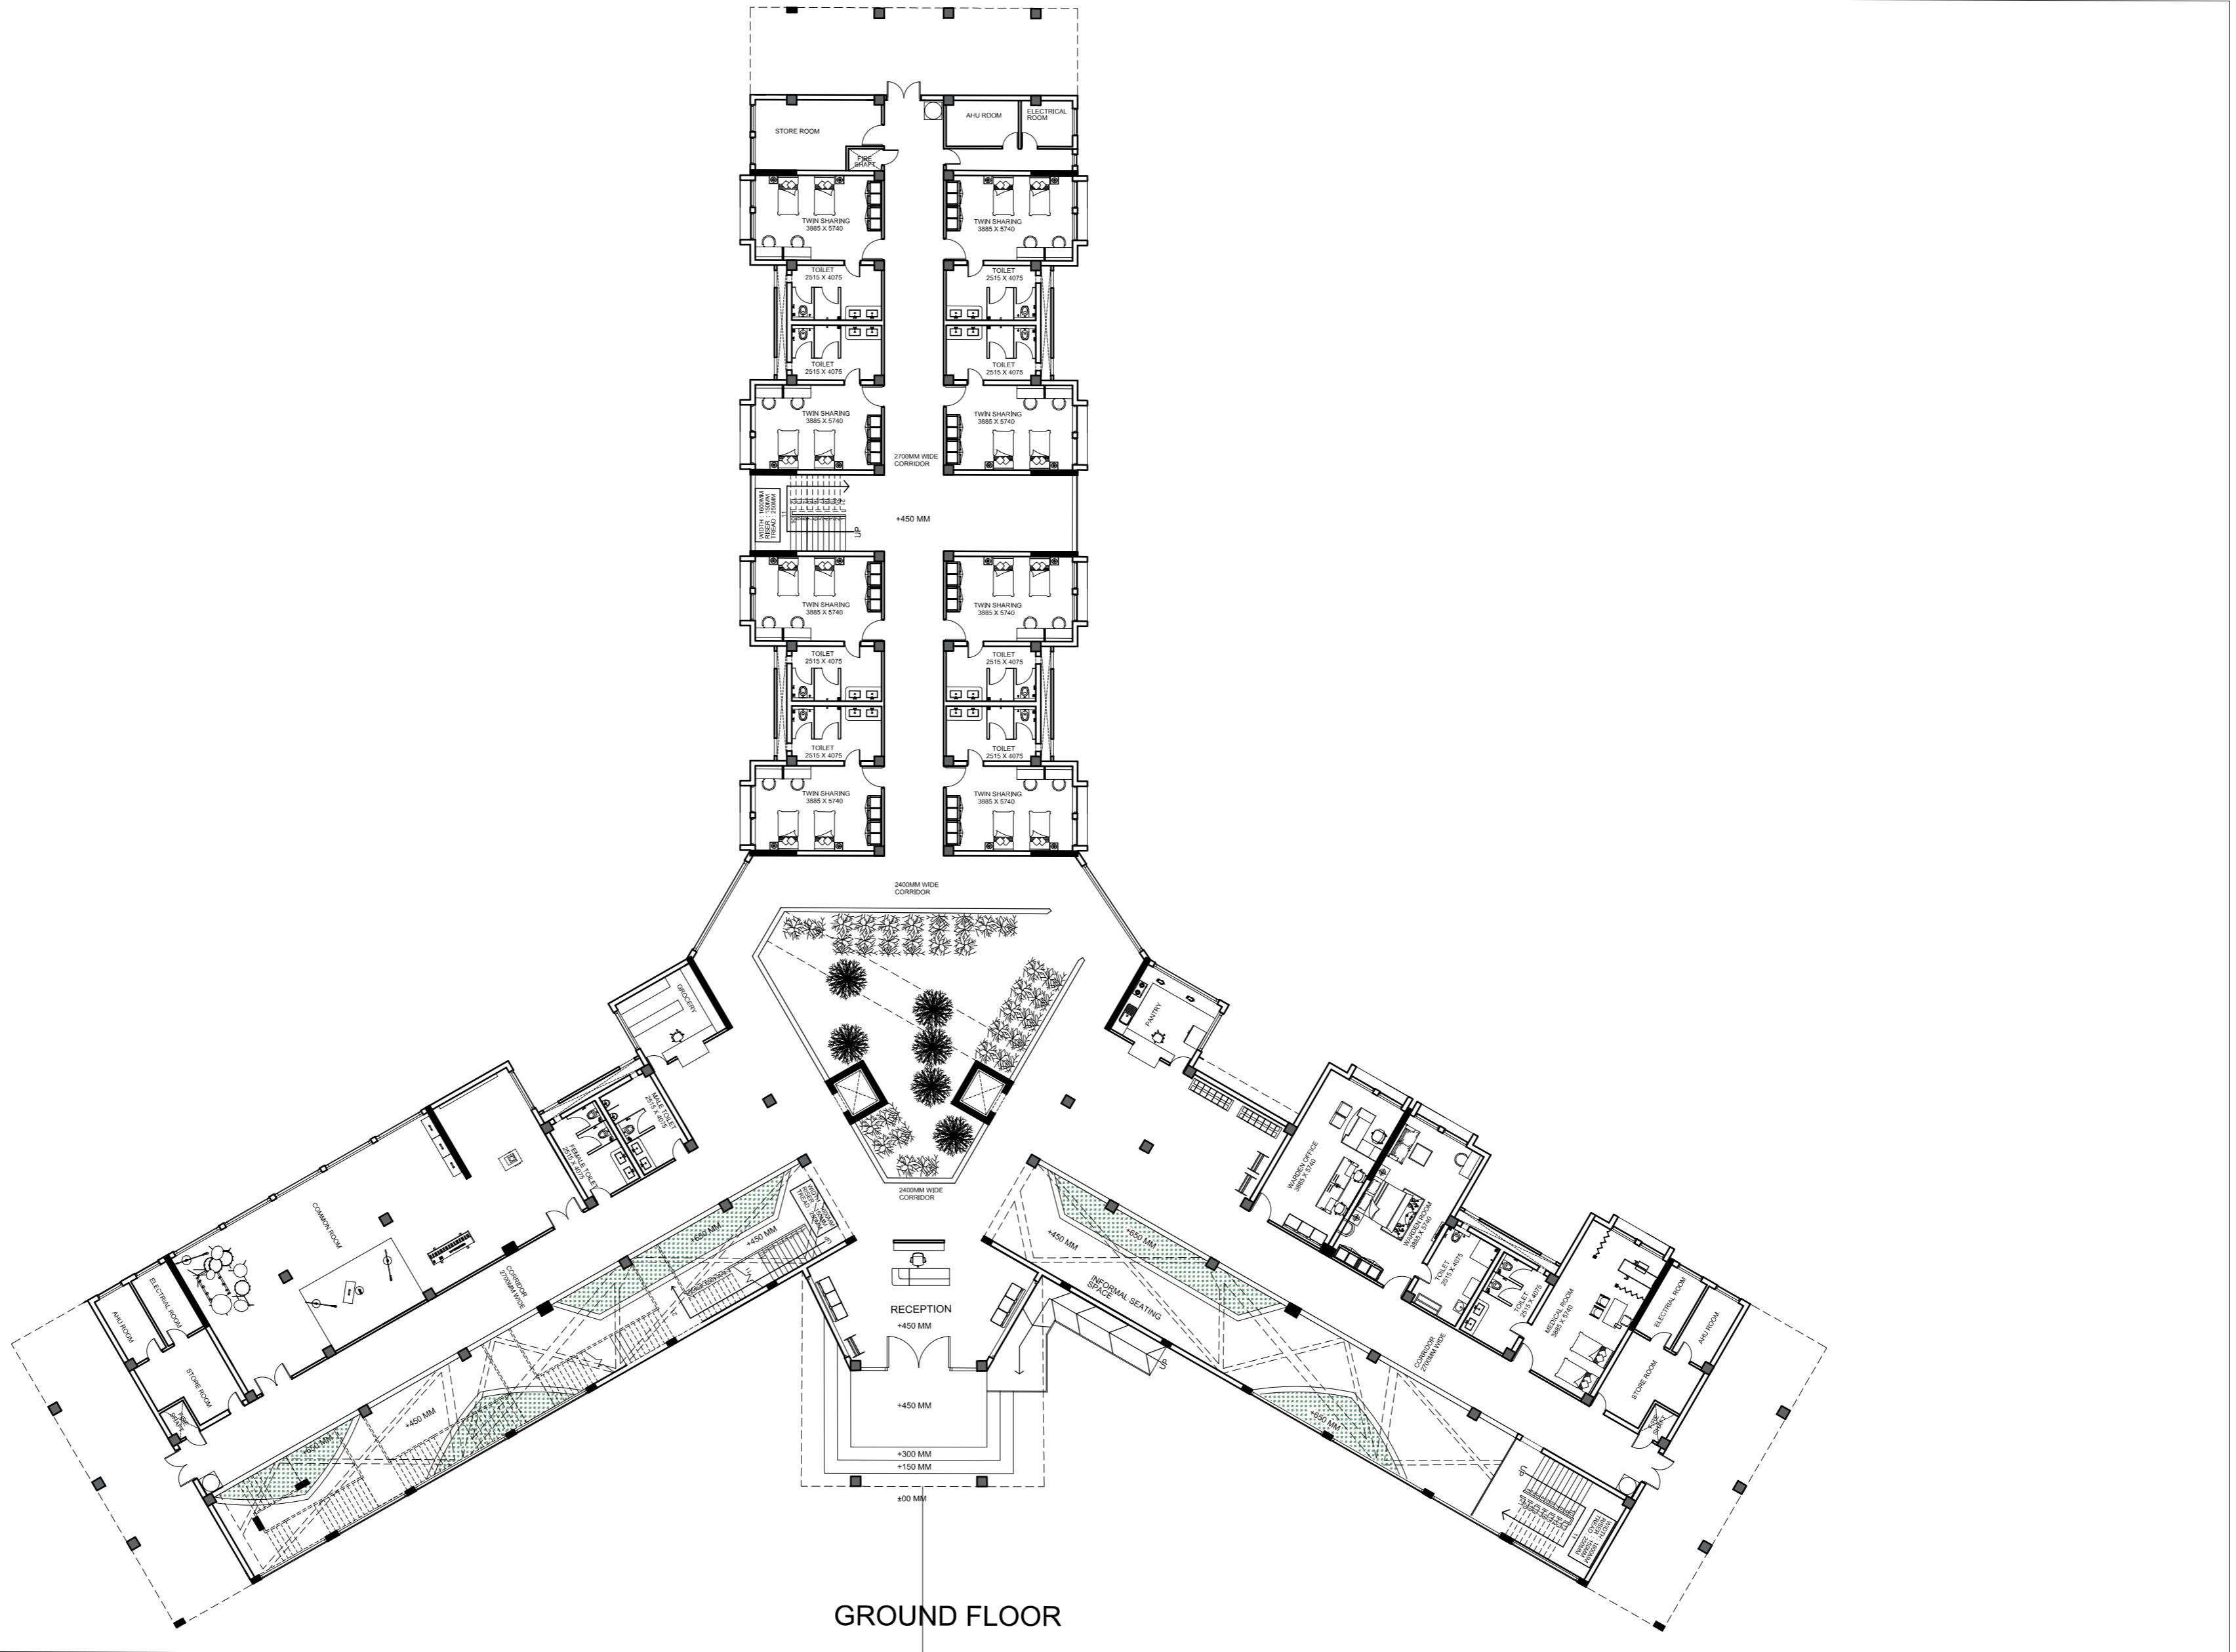

PROJECT TITLE- HOSTEL DESIGN

DATE- 08/12/2022

DRAWN BY- YASH VARDHAN


ADMISSION NO.- 20210634


SHEET TITLE- GROUND FLOOR PLAN

SHEET NO.- 02

SUBJECT- DESIGN NARRATIVE-V

SCALE-1:200

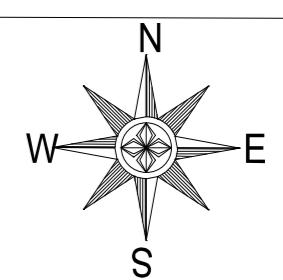

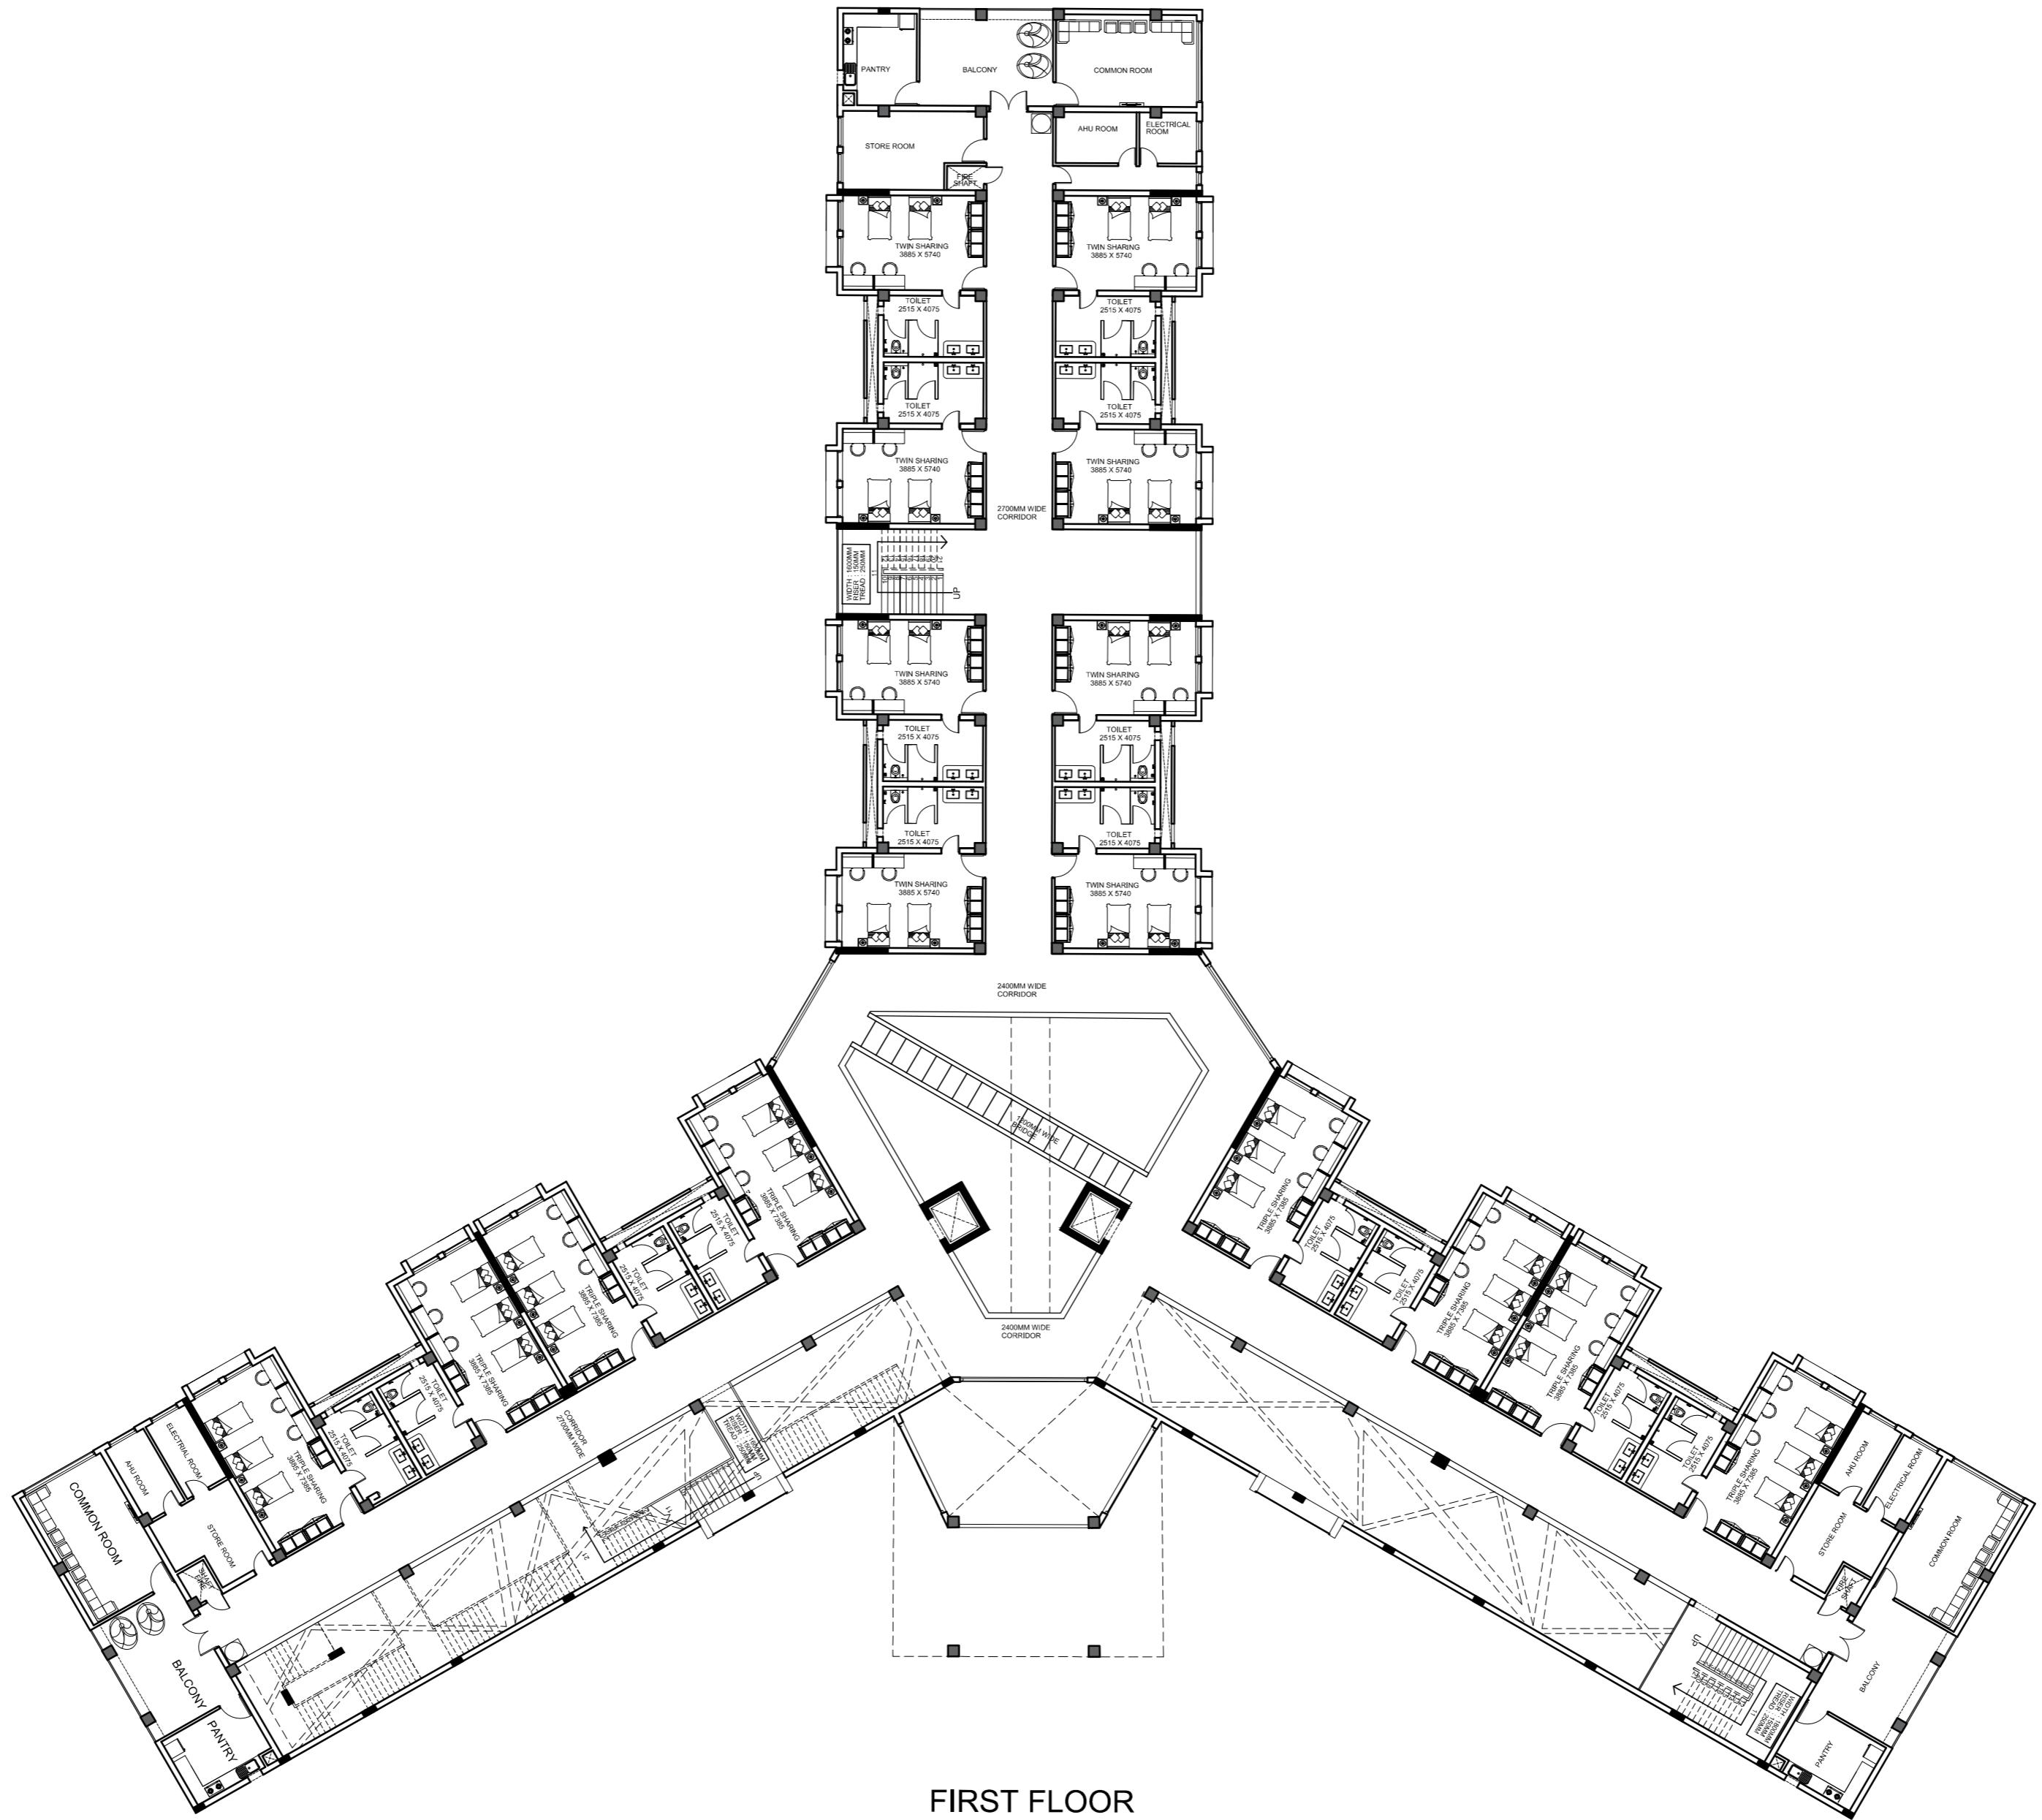

PROJECT TITLE- HOSTEL DESIGN

DATE- 08/12/2022

DRAWN BY- YASH VARDHAN


ADMISSION NO.- 20210634


SHEET TITLE- FIRST FLOOR PLAN

SHEET NO.- 03

SUBJECT- DESIGN NARRATIVE-V

SCALE-1:200

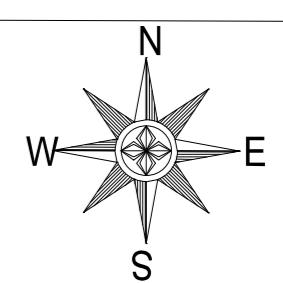

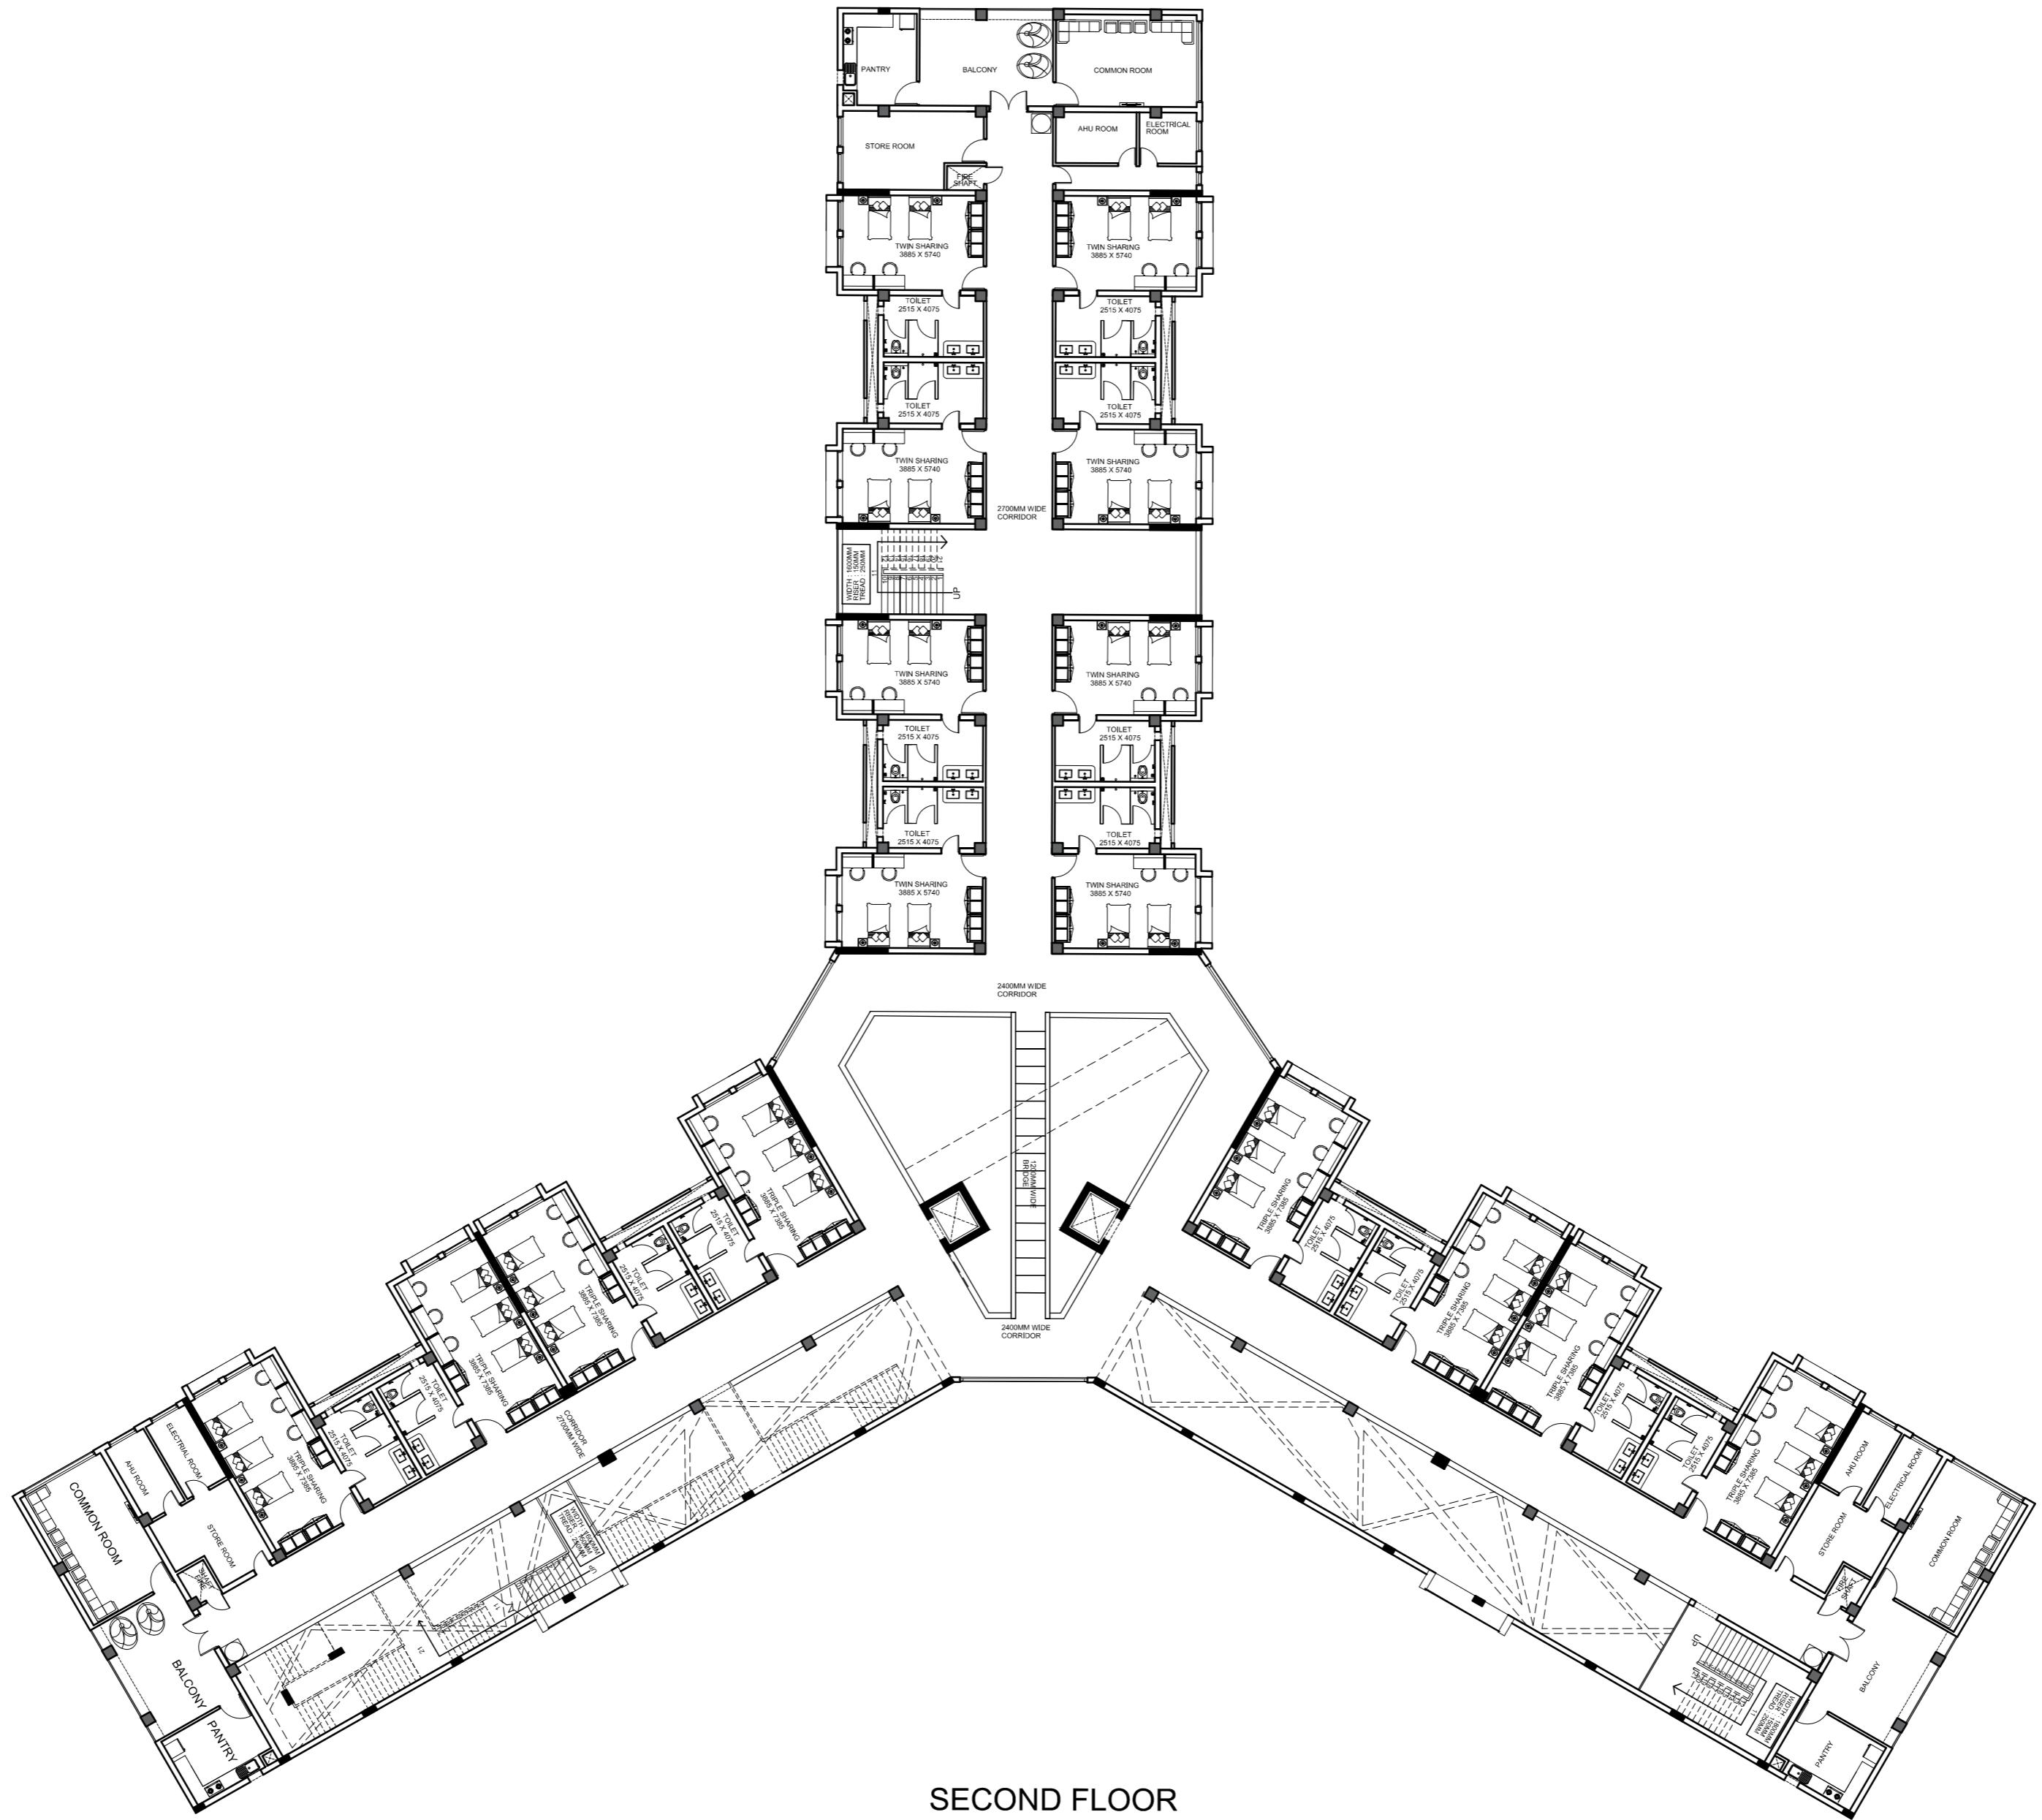

SECOND FLOOR

PROJECT TITLE- HOSTEL DESIGN

DATE- 08/12/2022

DRAWN BY- YASH VARDHAN


ADMISSION NO.- 20210634


SHEET TITLE- SECOND FLOOR PLAN

SHEET NO.- 04


SUBJECT- DESIGN NARRATIVE-V

SCALE-1:200

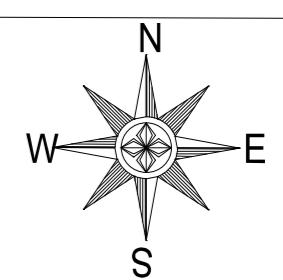

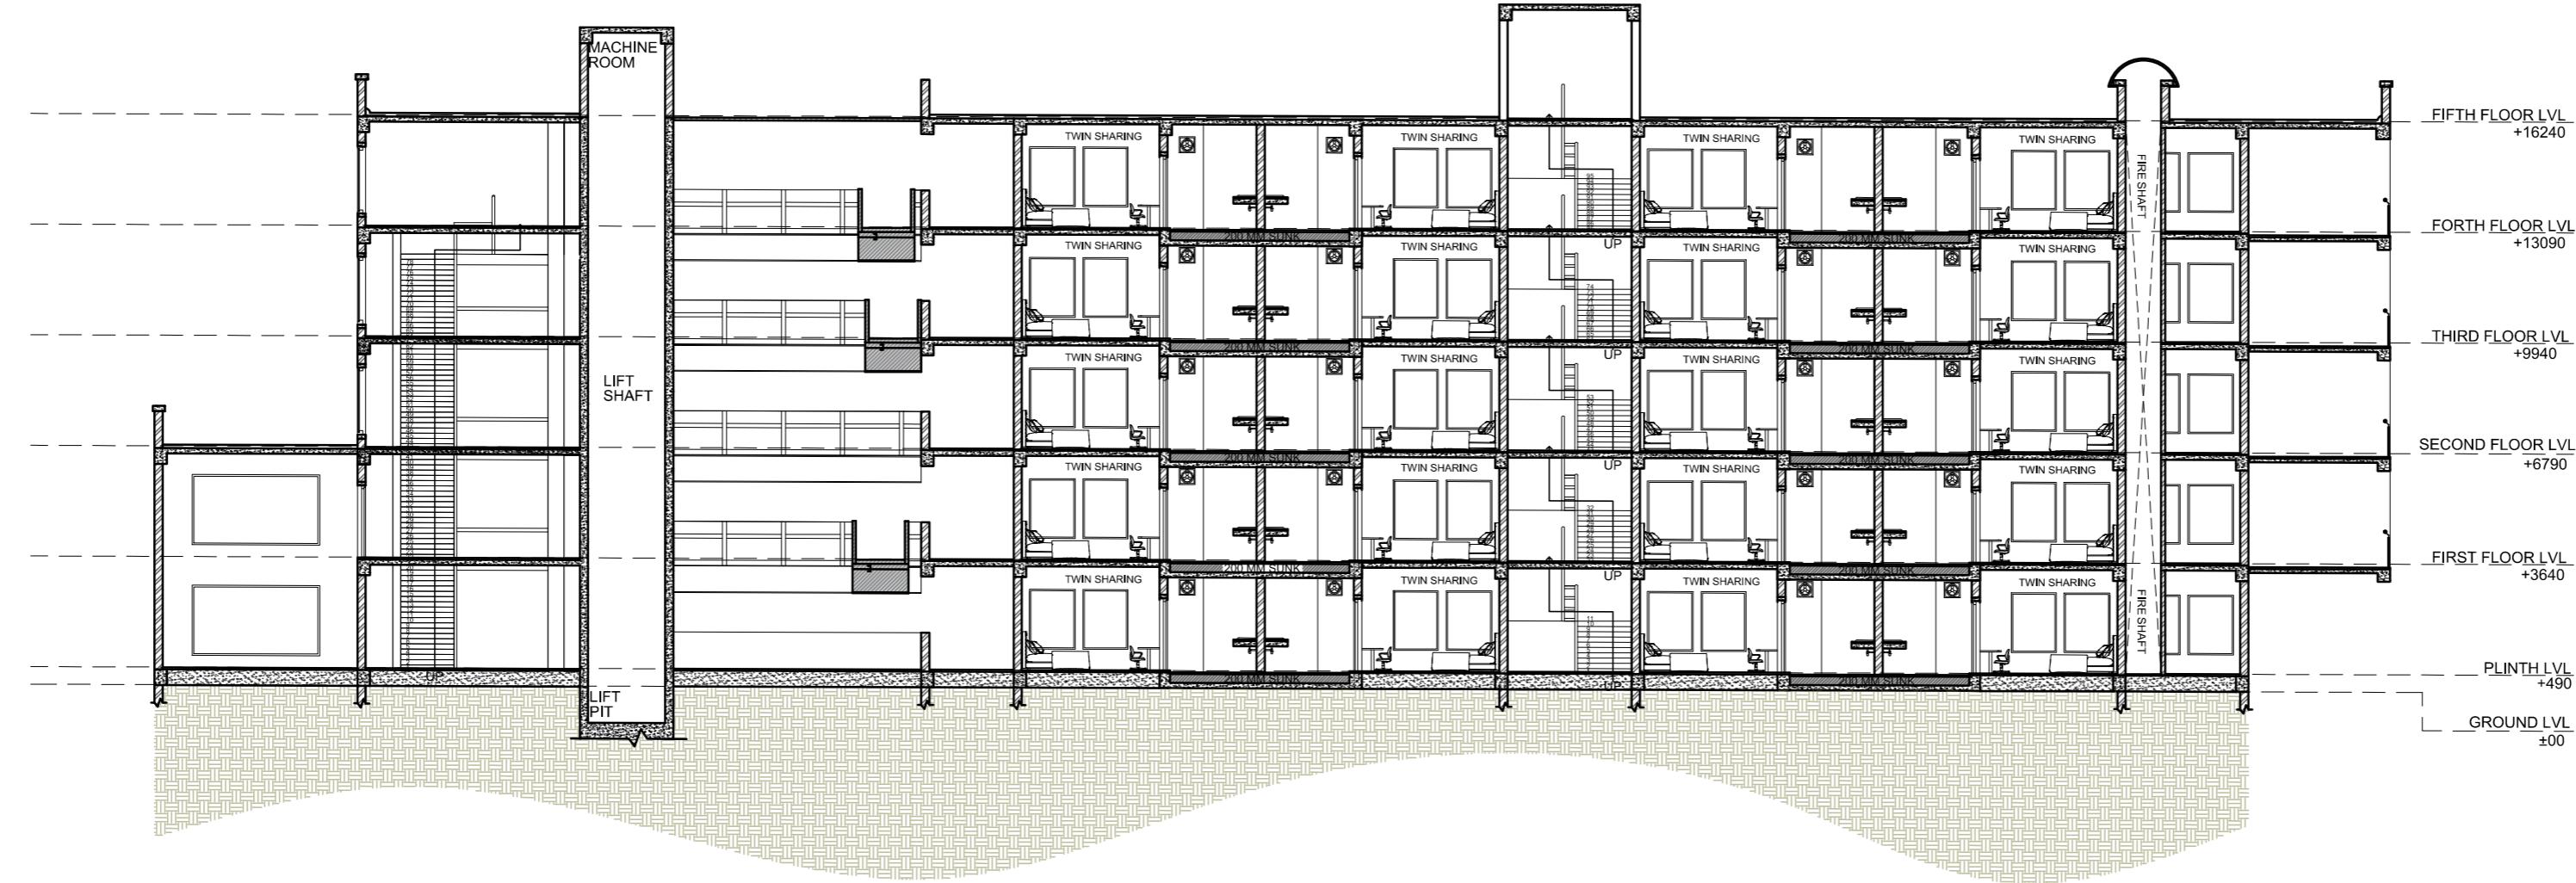

SECTION YY'

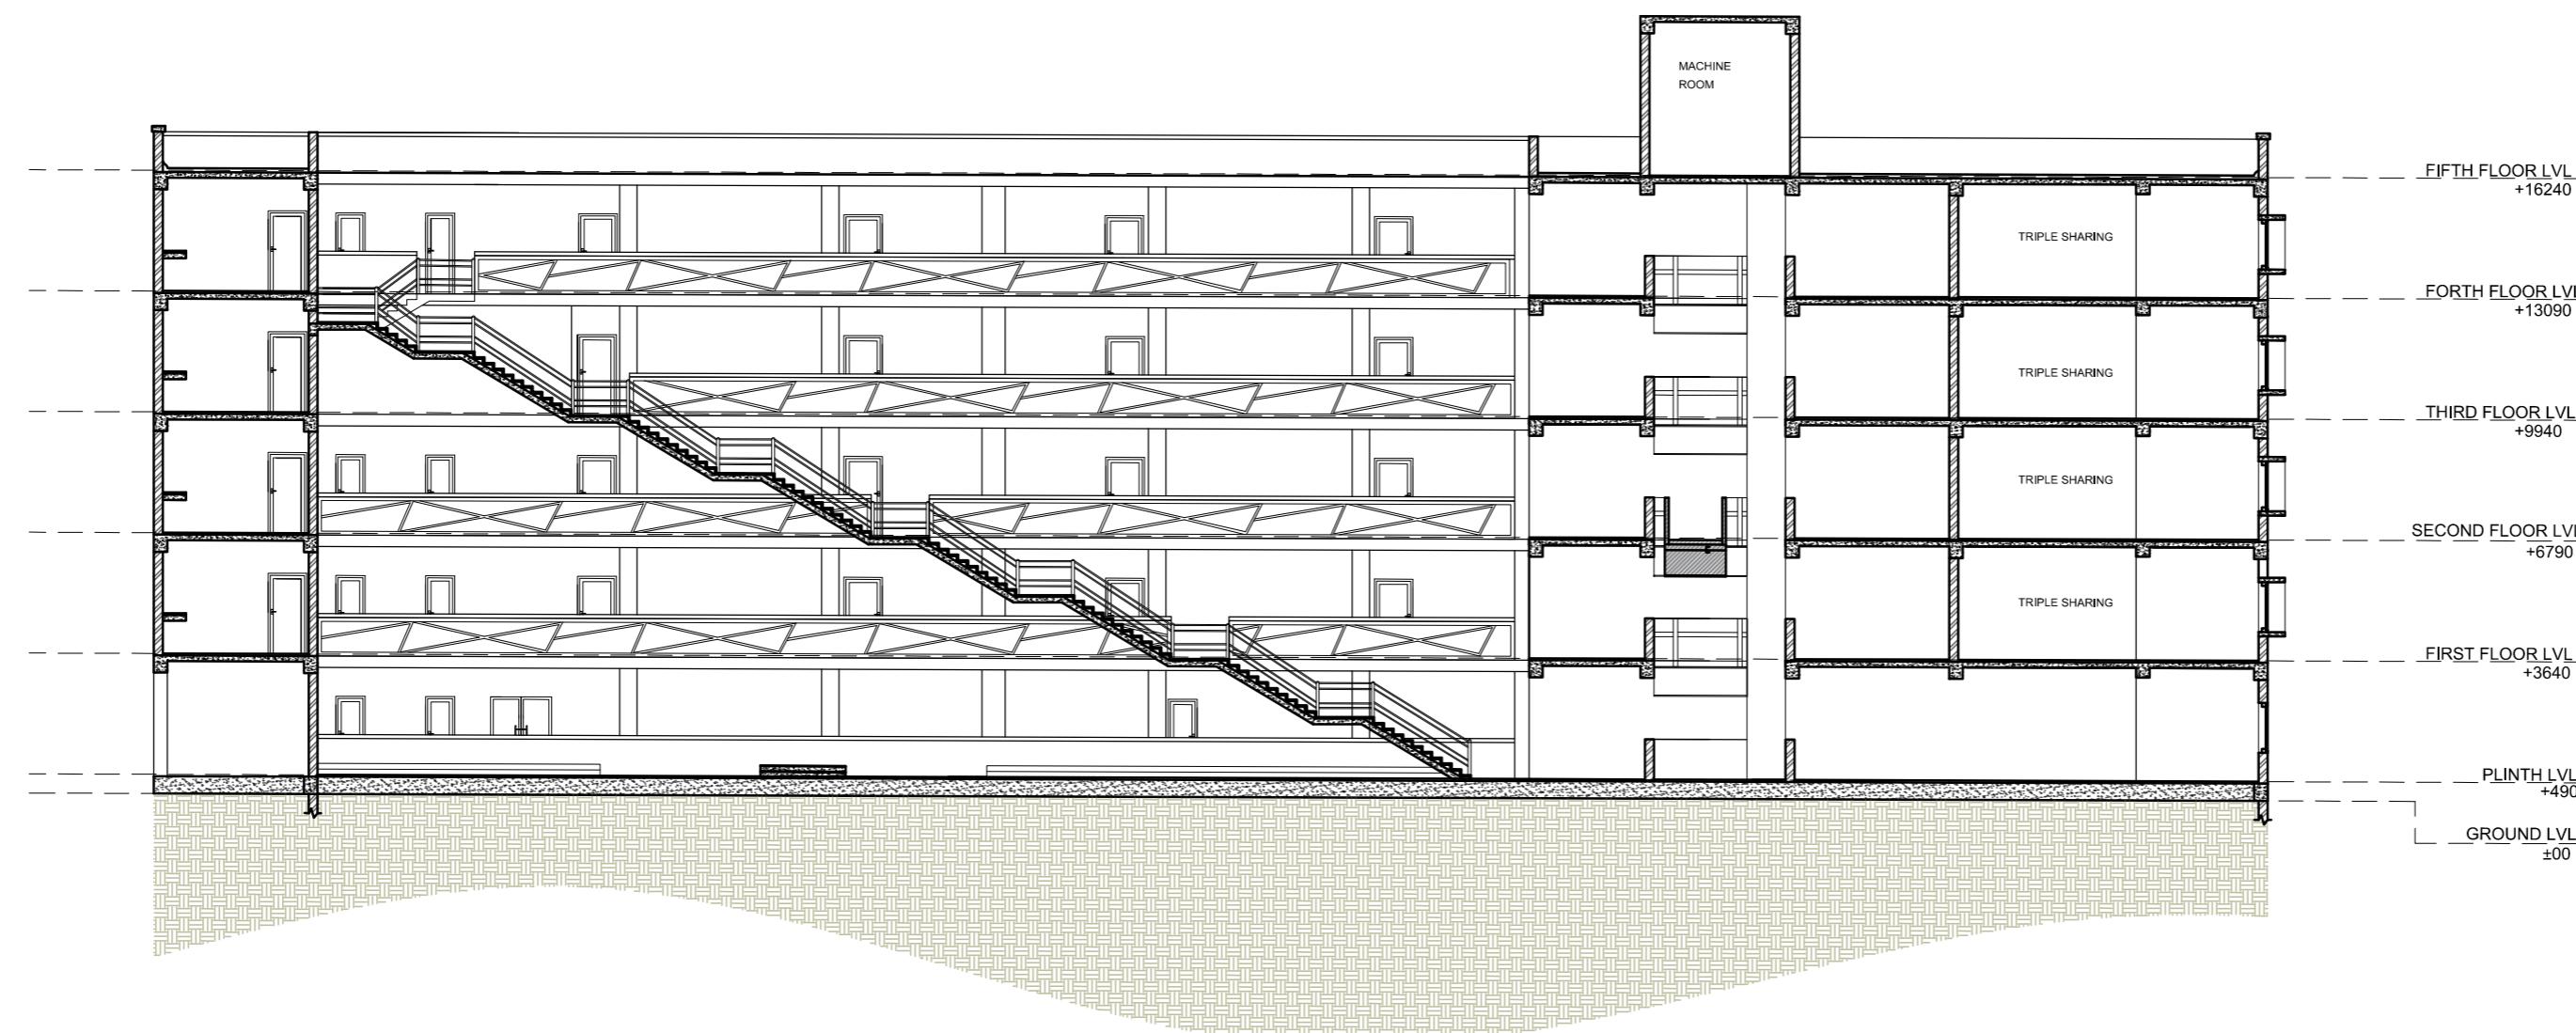

SECTION XX'

PROJECT TITLE- HOSTEL DESIGN

DATE- 08/12/2022

DRAWN BY- YASH VARDHAN


ADMISSION NO.- 20210634


SHEET TITLE- SECTION

SHEET NO.- 08


SUBJECT- DESIGN NARRATIVE-V

SCALE-1:150

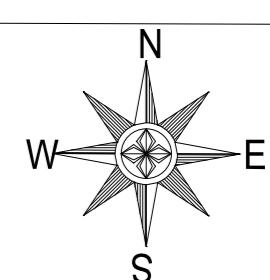


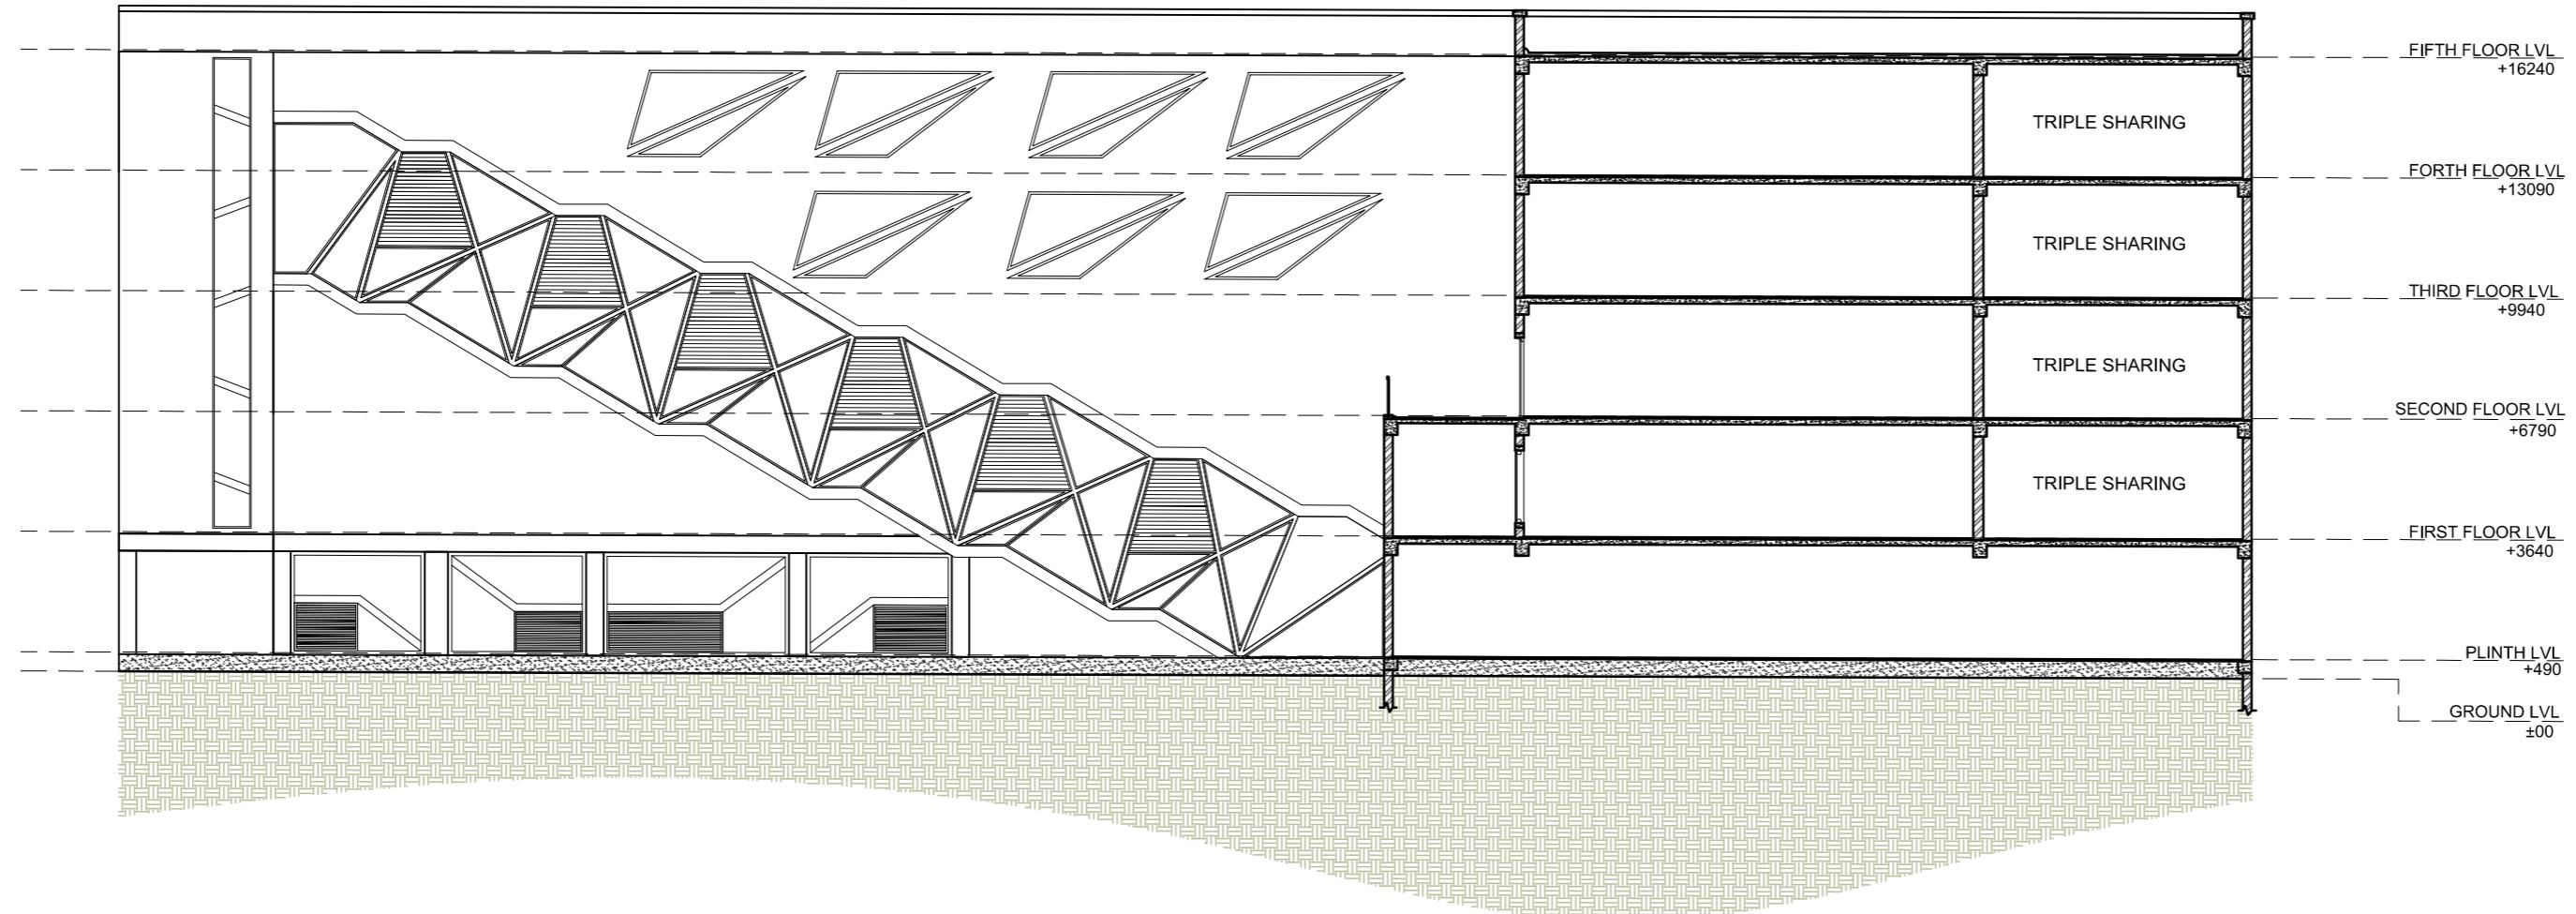

SECTIONAL ELEVATION ZZ'

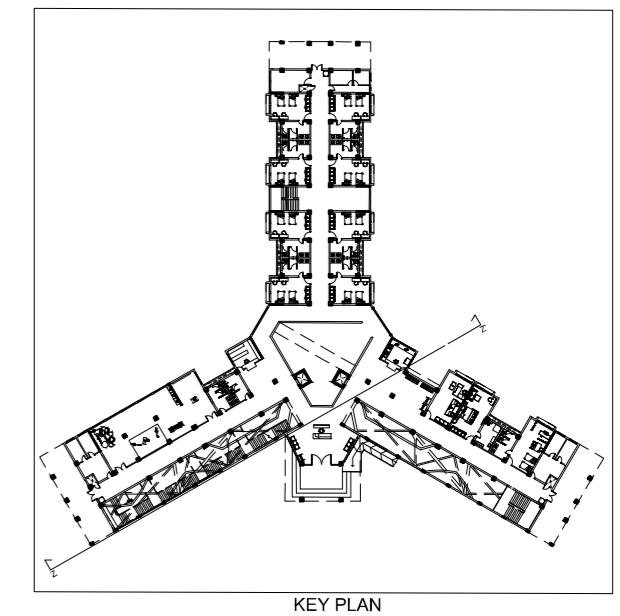

KEY PLAN

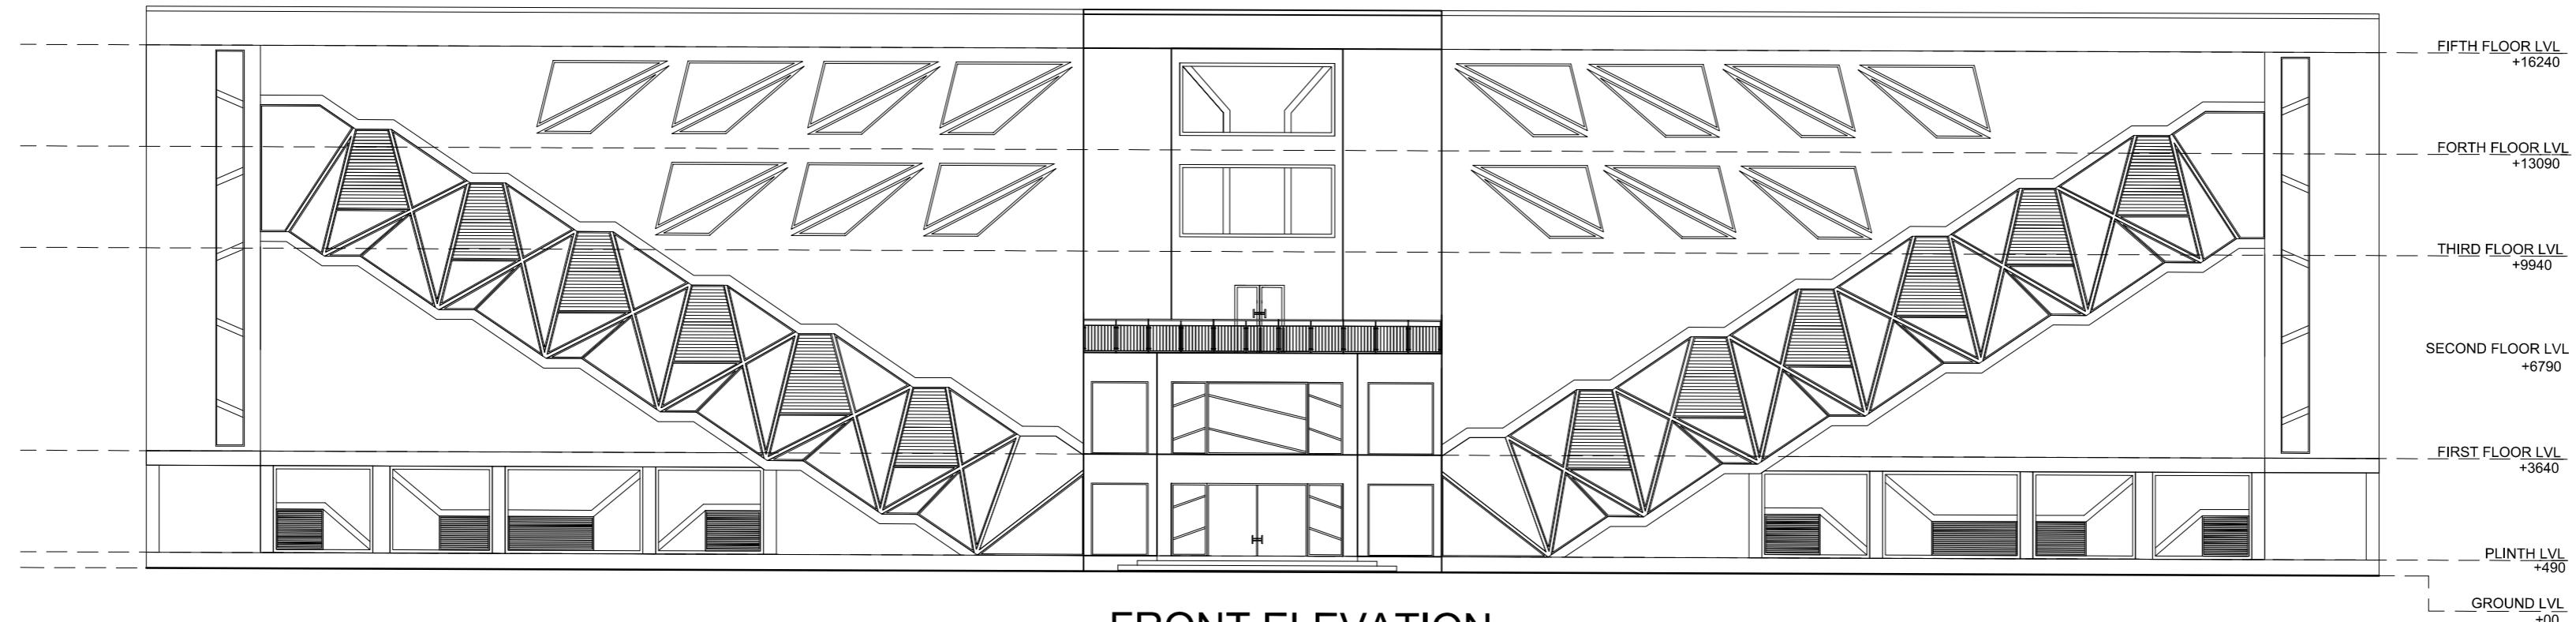

FRONT ELEVATION

PROJECT TITLE- HOSTEL DESIGN

DATE- 08/12/2022

DRAWN BY- YASH VARDHAN


ADMISSION NO.- 20210634


SHEET TITLE- SECTION & ELEVATION

SHEET NO.- 09


SUBJECT- DESIGN NARRATIVE-V

SCALE-1:150

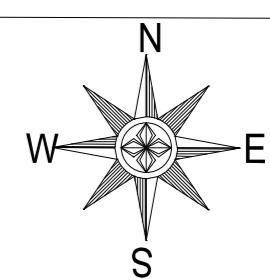

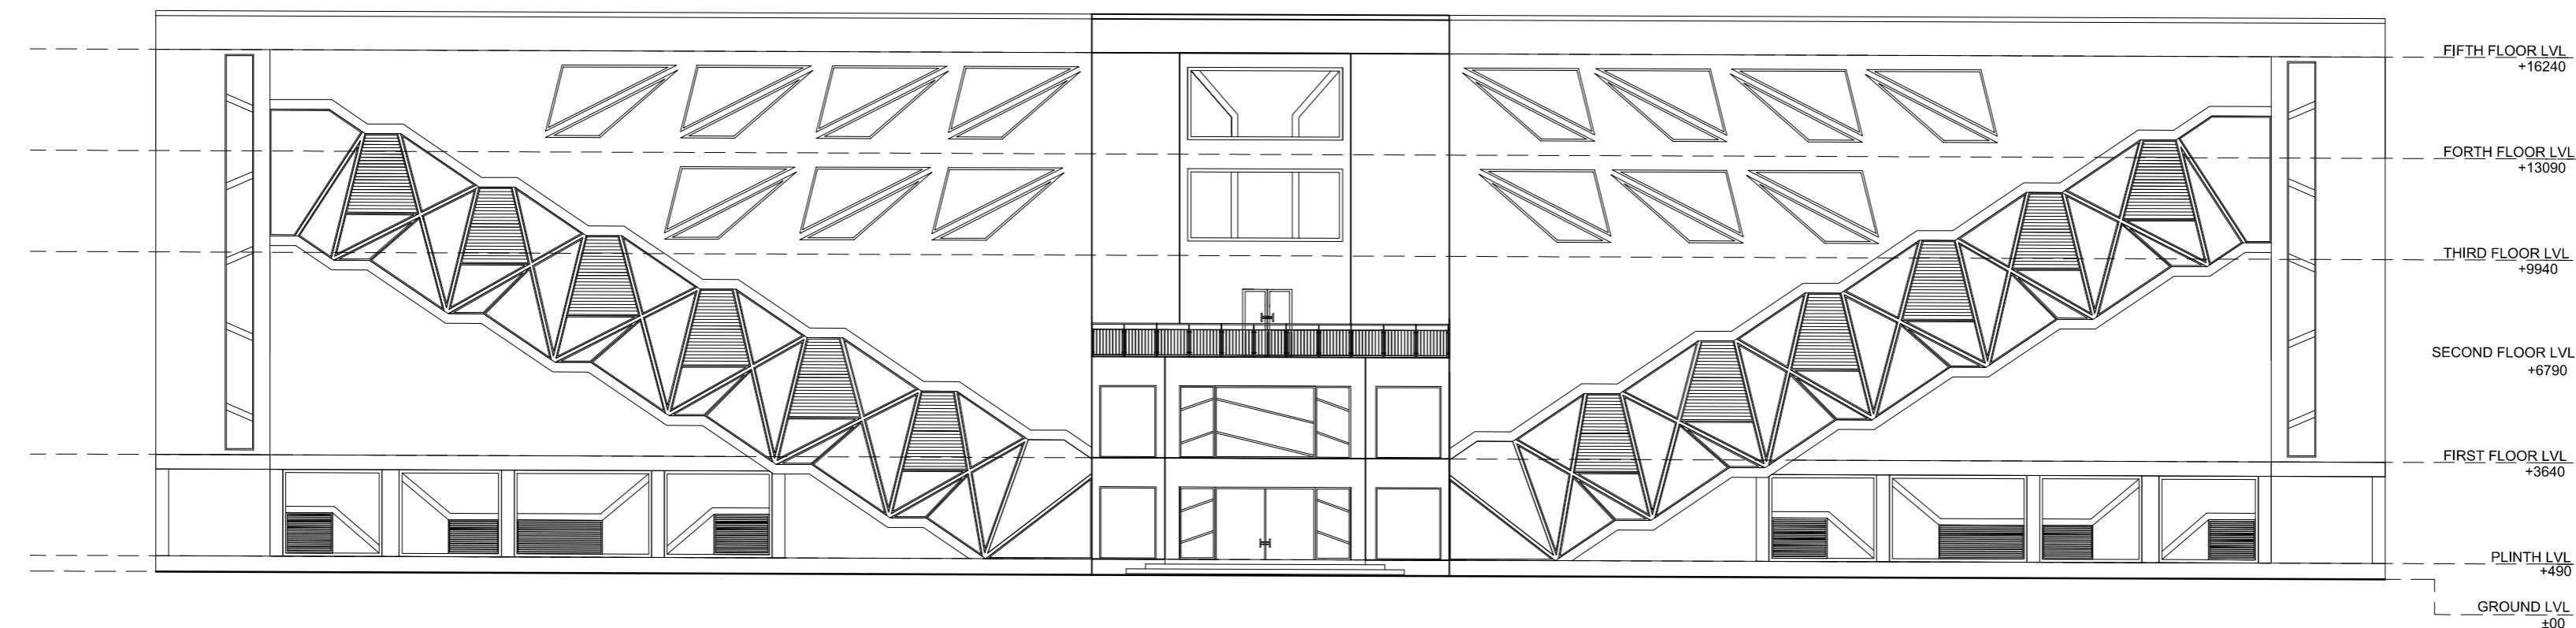

FRONT ELEVATION

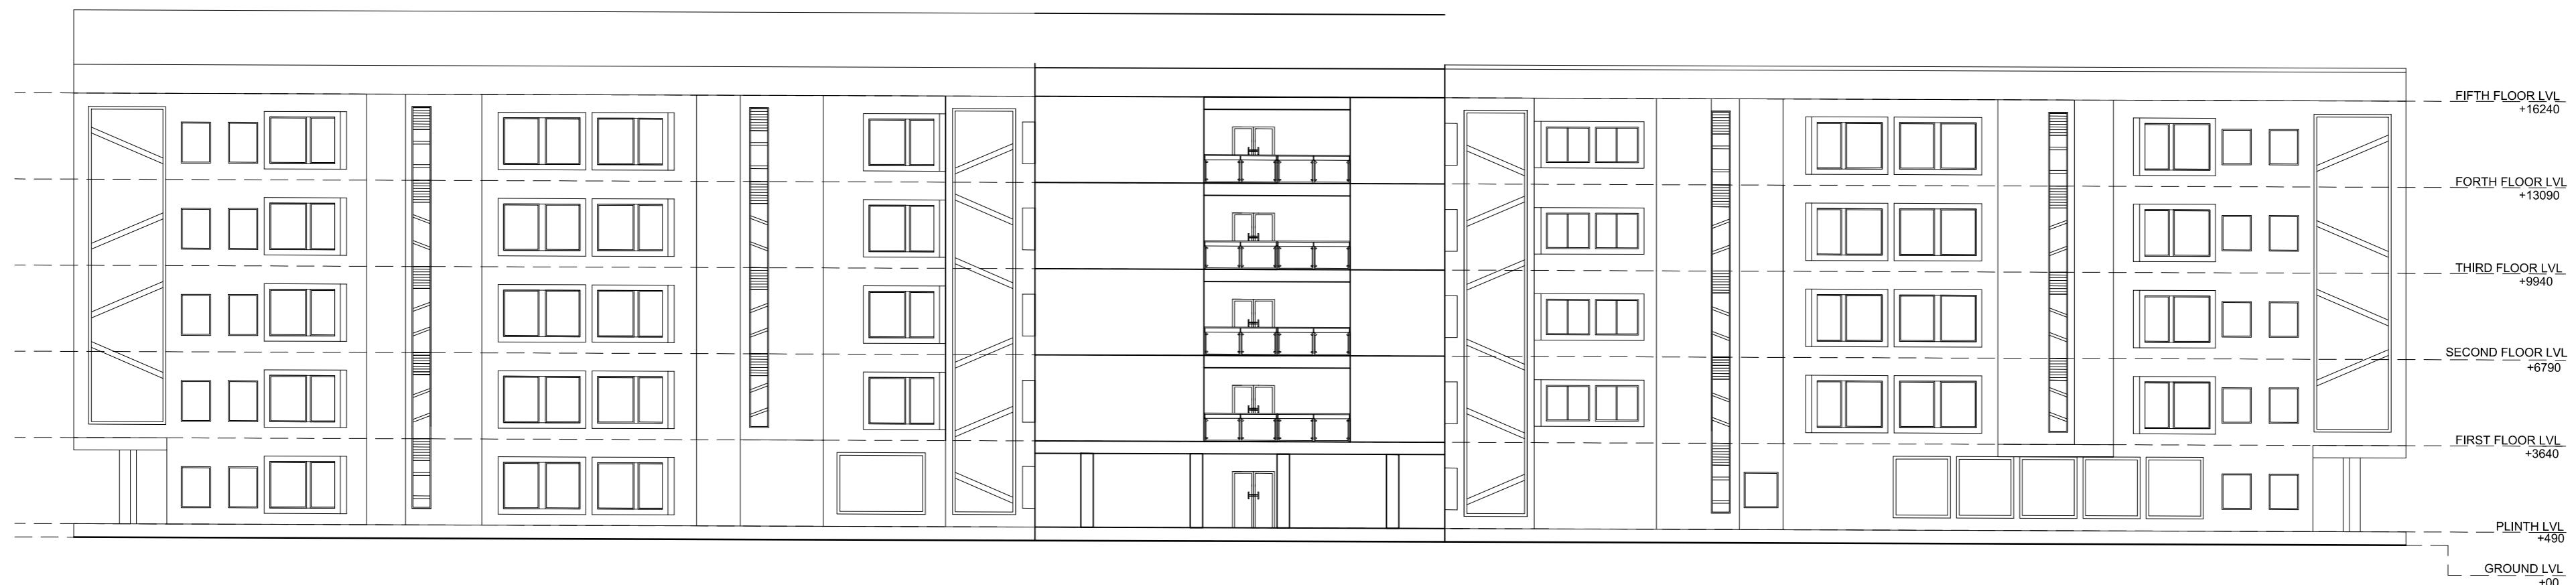

REAR ELEVATION

PROJECT TITLE- HOSTEL DESIGN

DATE- 08/12/2022

DRAWN BY- YASH VARDHAN


ADMISSION NO.- 20210634


SHEET TITLE- ELEVATION

SHEET NO.- 10

SUBJECT- DESIGN NARRATIVE-V

SCALE-1:150

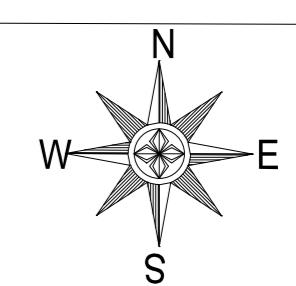

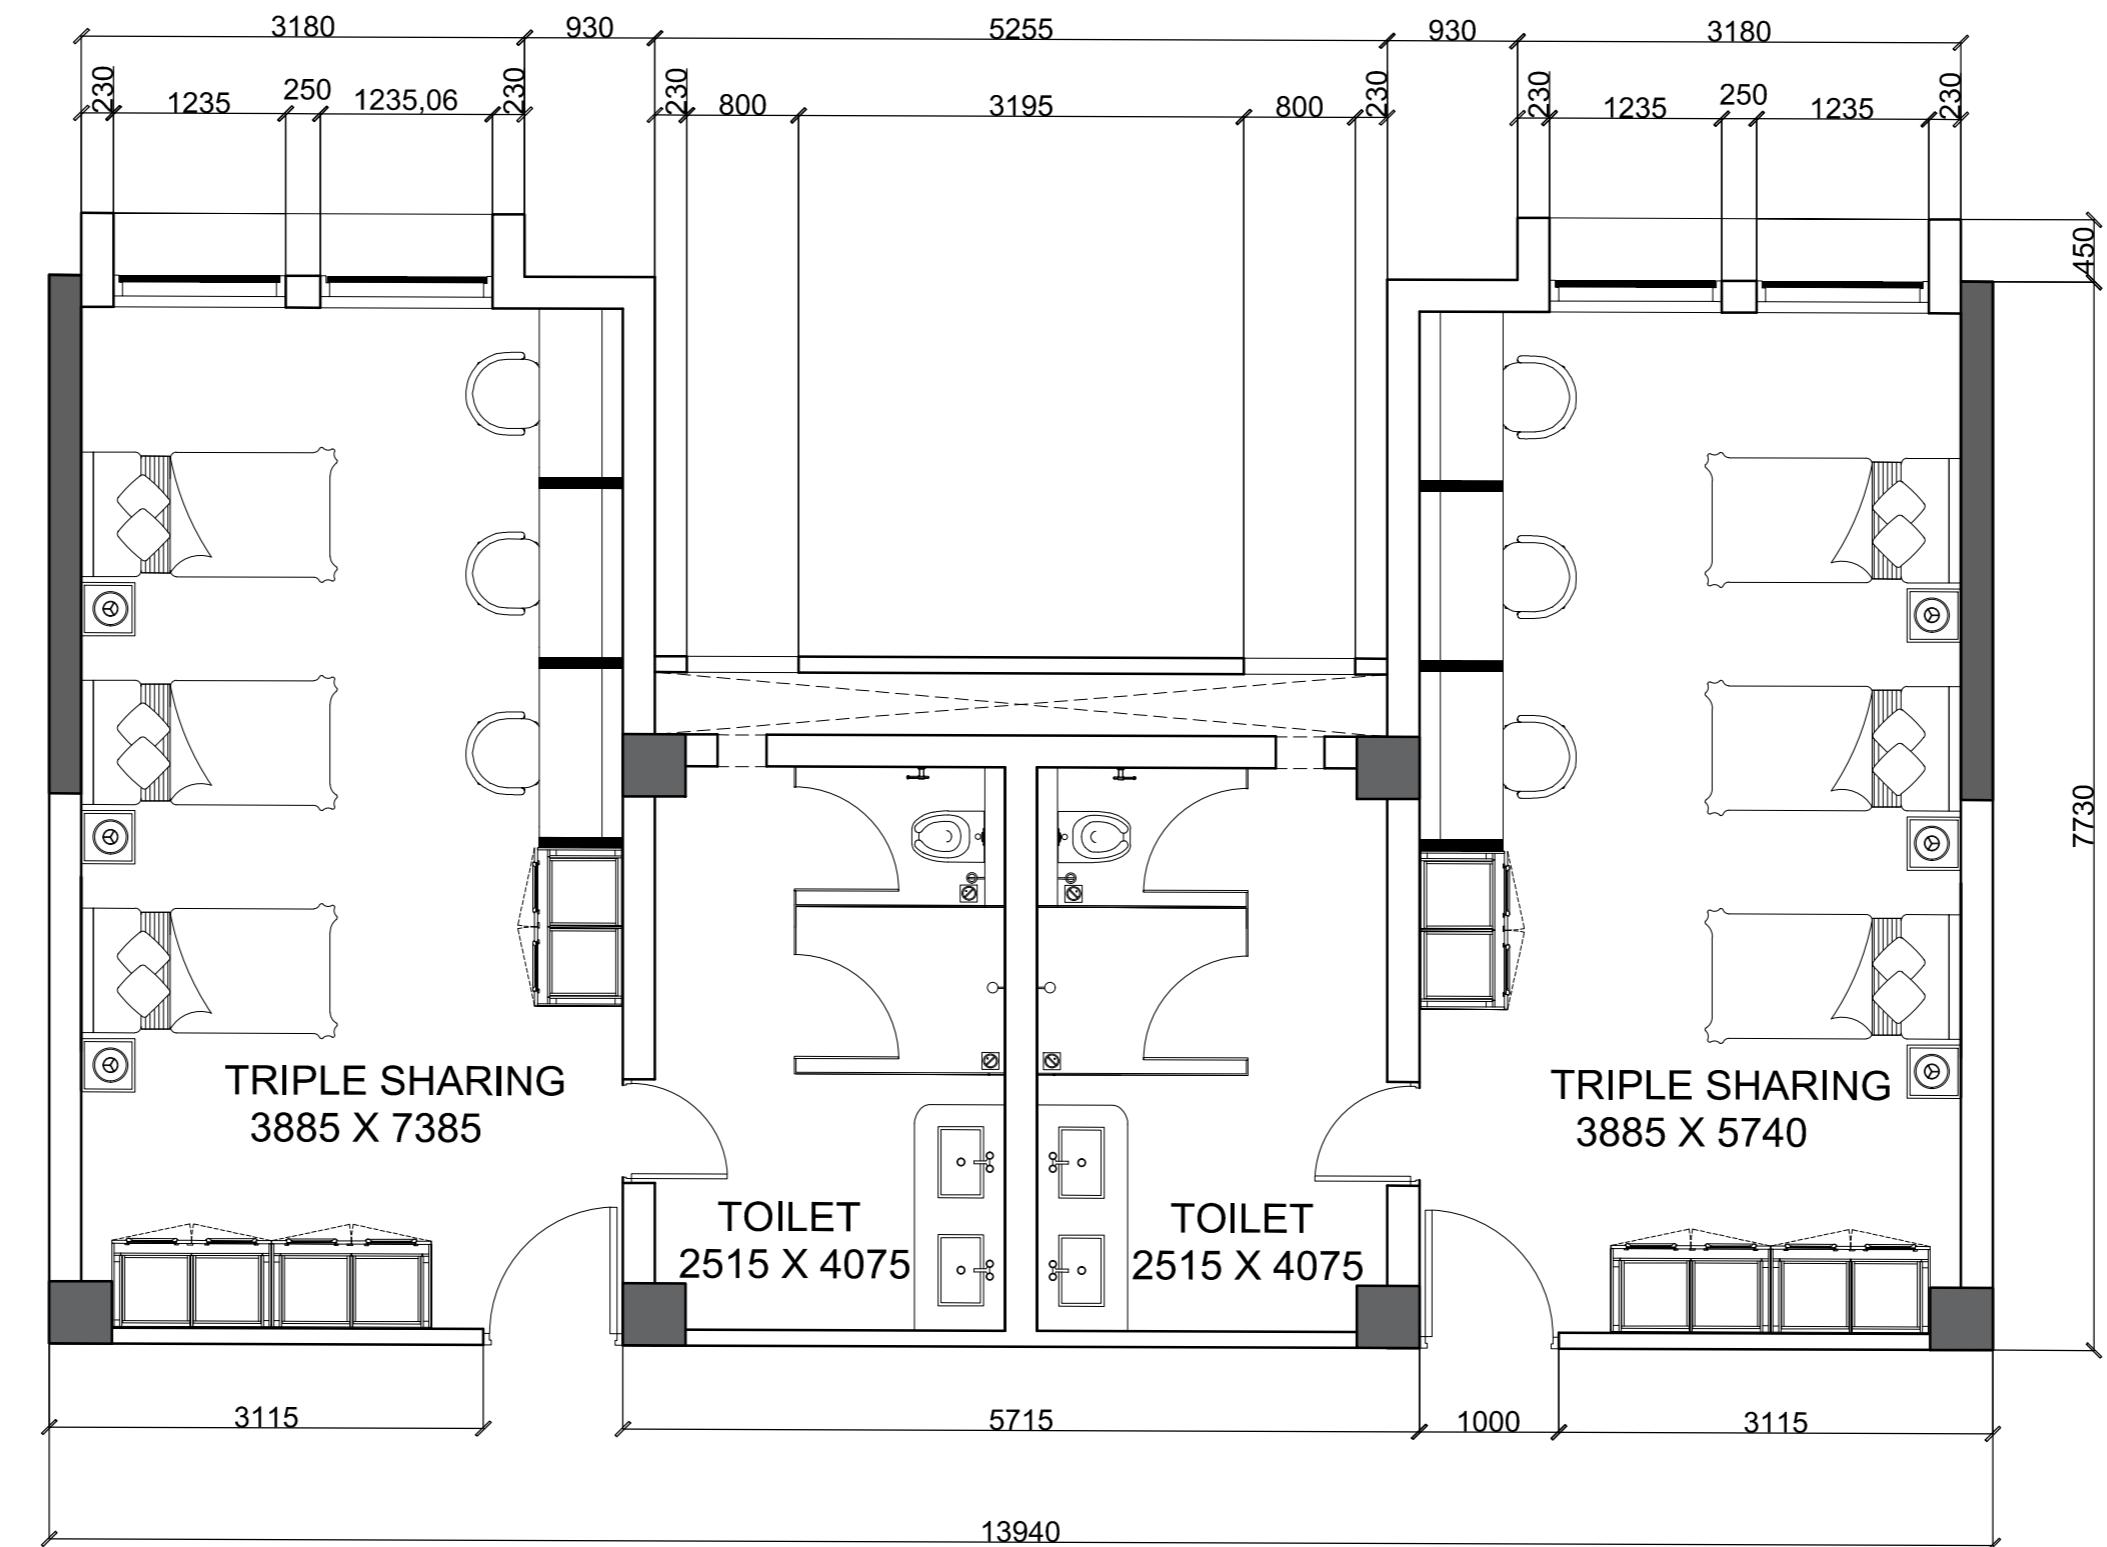

TRIPLE SHARING

PROJECT TITLE- HOSTEL DESIGN

DATE- 08/12/2022

DRAWN BY- YASH VARDHAN


ADMISSION NO.- 20210634


SHEET TITLE- UNIT PLAN

SHEET NO.- 12

SUBJECT- DESIGN NARRATIVE-V

SCALE-1:150

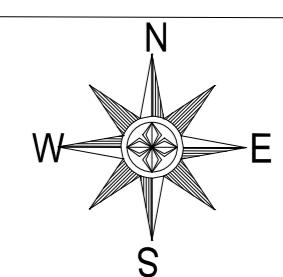

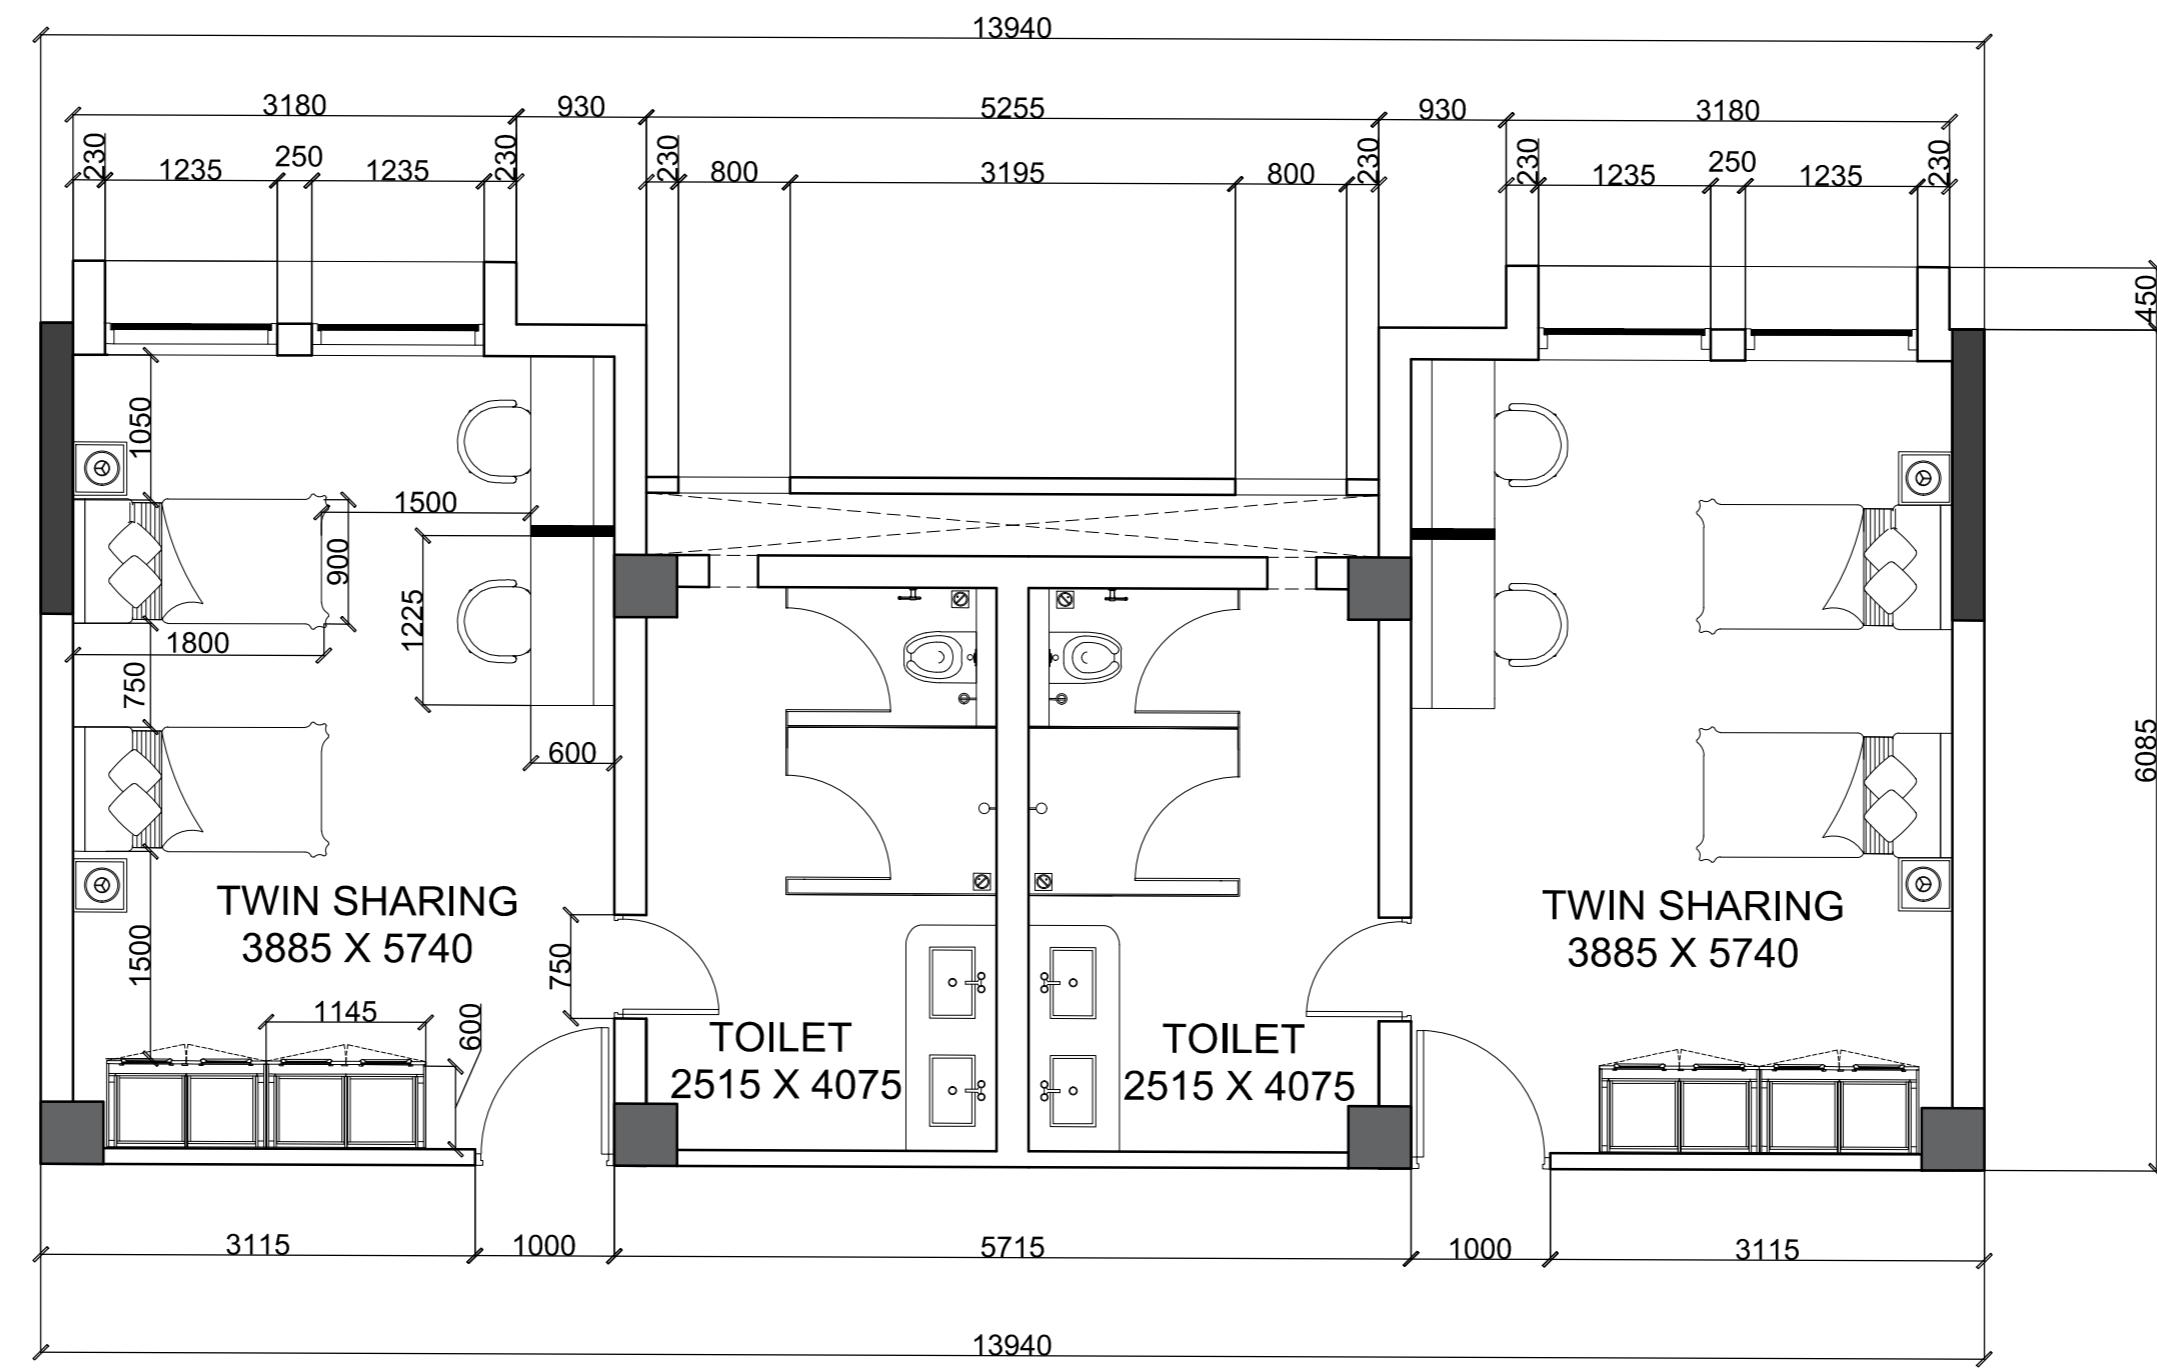

TWIN SHARING

PROJECT TITLE- HOSTEL DESIGN

DATE- 08/12/2022

DRAWN BY- YASH VARDHAN

ADMISSION NO.- 20210634

SHEET TITLE- UNIT PLAN

SHEET NO.- 13

SUBJECT- DESIGN NARRATIVE-V

SCALE-1:150

