









**LEGEND**


- CLASSROOM
- WASHROOM
- STAFFROOM
- COMPUTER LAB
- CORRIDOR
- VERTICAL CIRCULATION




LOWERGROUND FLOOR

LEGEND

- ACTIVITY ROOM
- ADMIN AREA
- CORRIDOR

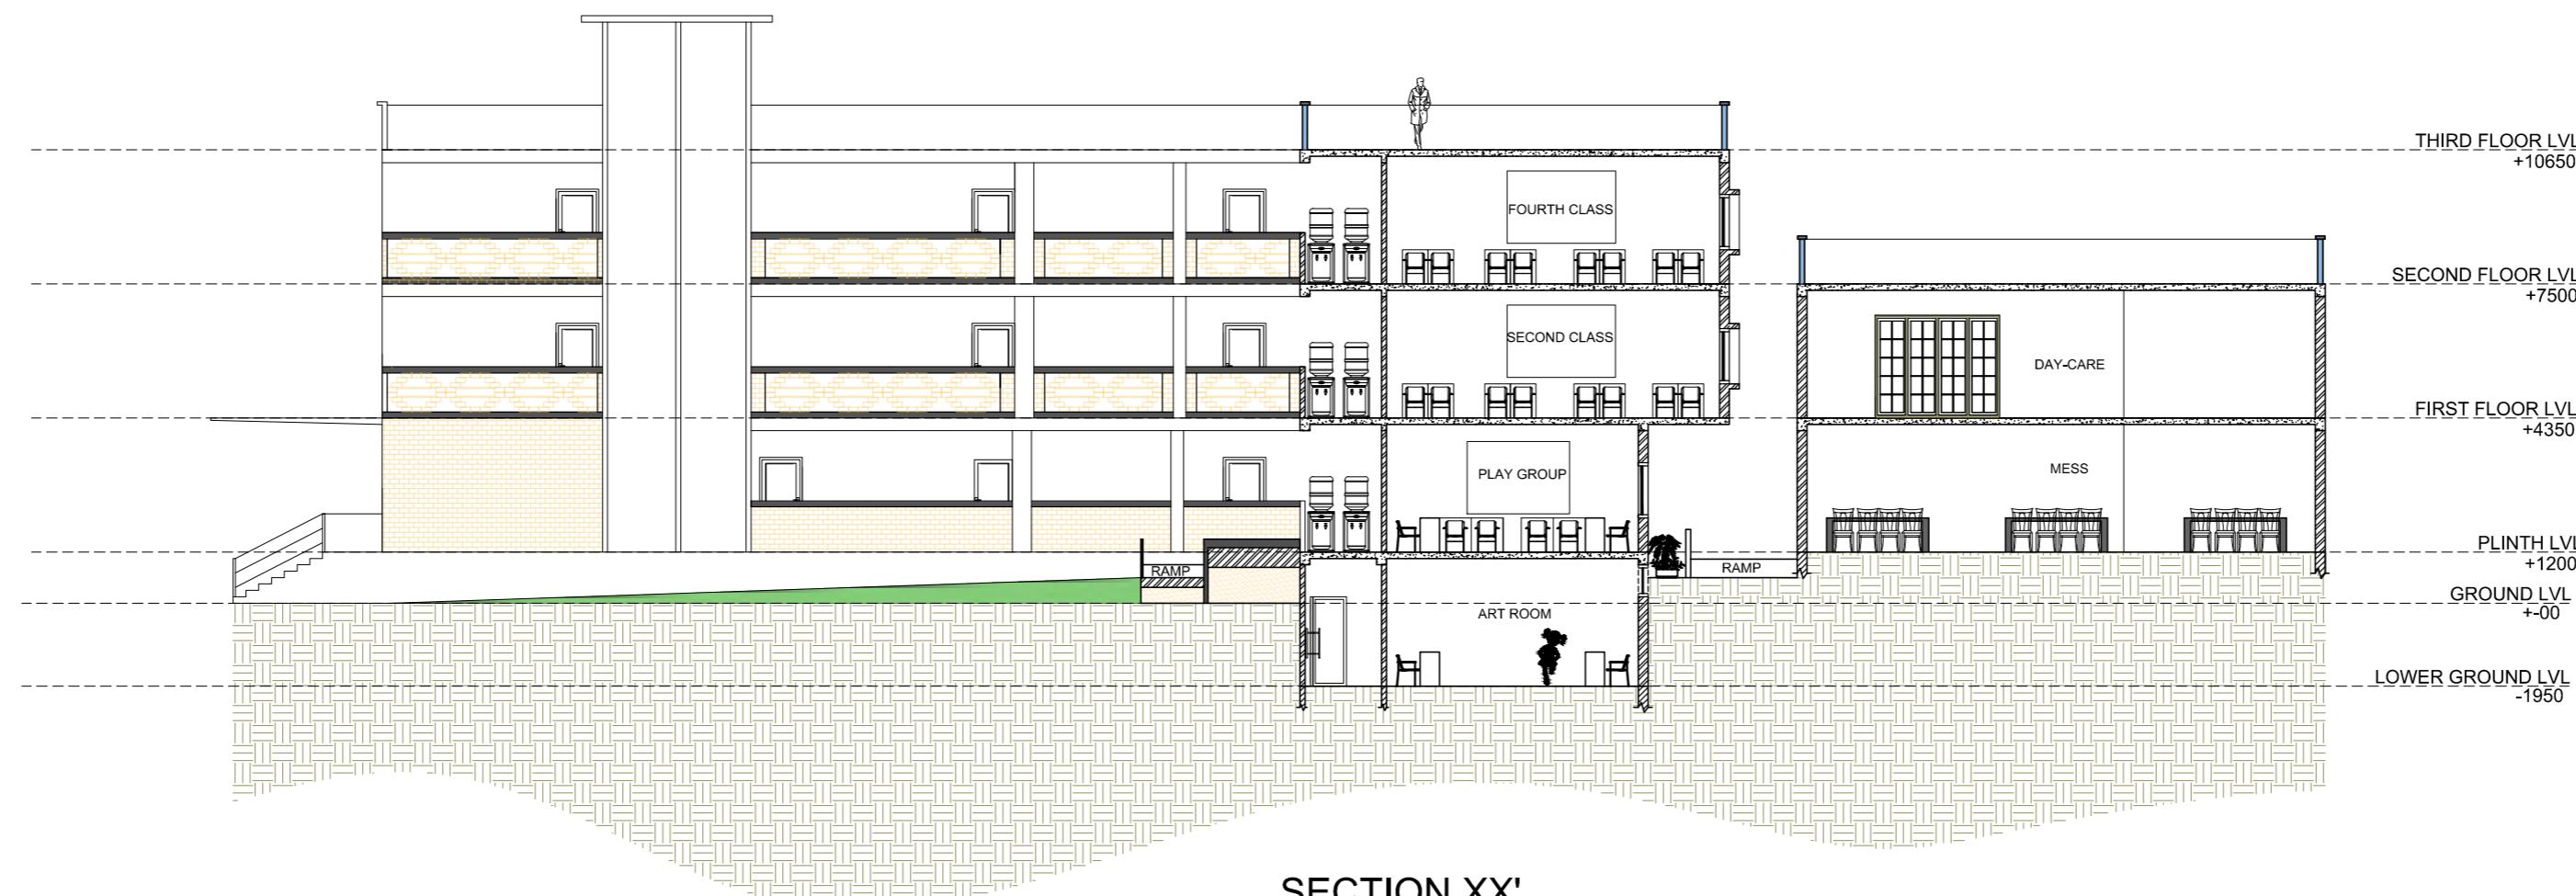

SECTION XX'

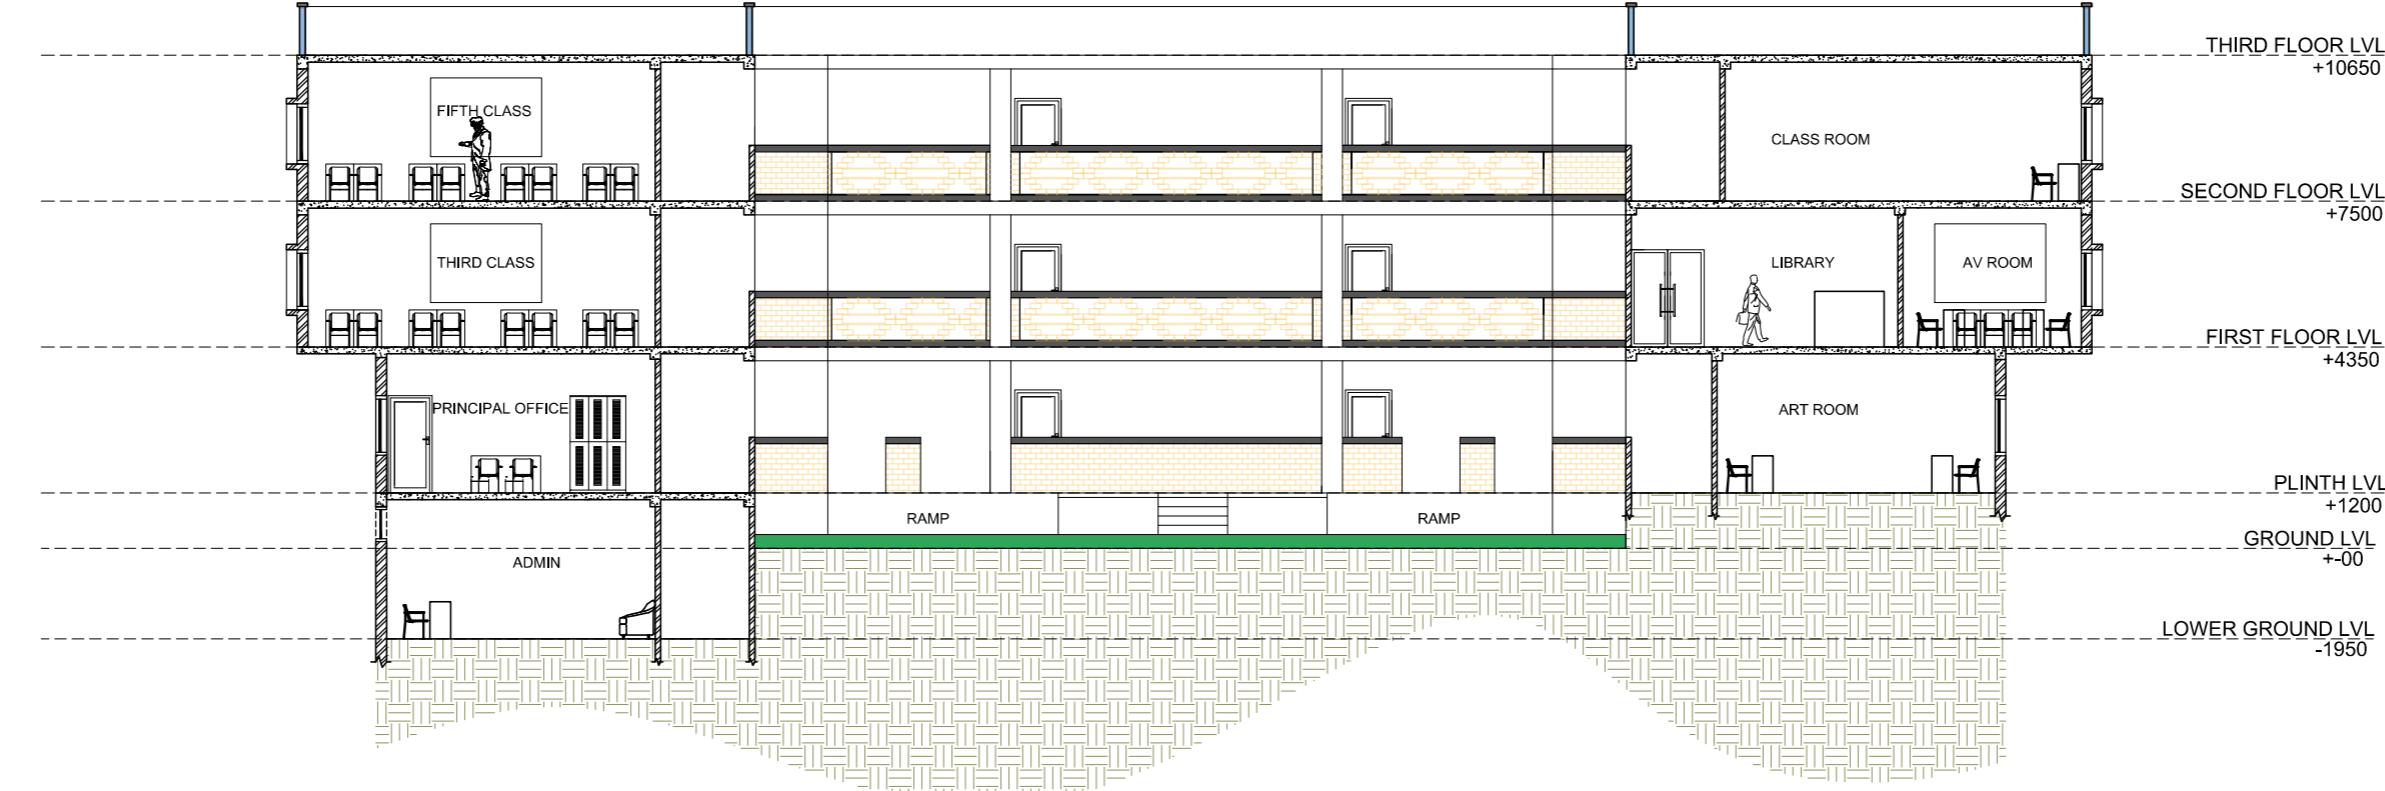


SECTION YY'

GD GOENKA UNIVERSITY, SOHNA SoAP (SEM-IV)	PROPOSED PRIMARY SCHOOL DESIGN (SITE- M3M GOLF ESTATE, SECTOR- 65)	SCALE- 1:150	FACULTIES- MRS. HARMAN MR. VIKAS GOYAL	SUBMITTED BY- YASH VARDHAN GOYAL
---	---	--------------	---	----------------------------------



SECTION CC'

GD GOENKA UNIVERSITY, SOHNA SoAP (SEM-IV)	PROPOSED PRIMARY SCHOOL DESIGN (SITE- M3M GOLF ESTATE, SECTOR- 65)	SCALE- 1:150	FACULTIES- MRS. HARMAN MR. VIKAS GOYAL	SUBMITTED BY- YASH VARDHAN GOYAL
---	---	--------------	---	----------------------------------

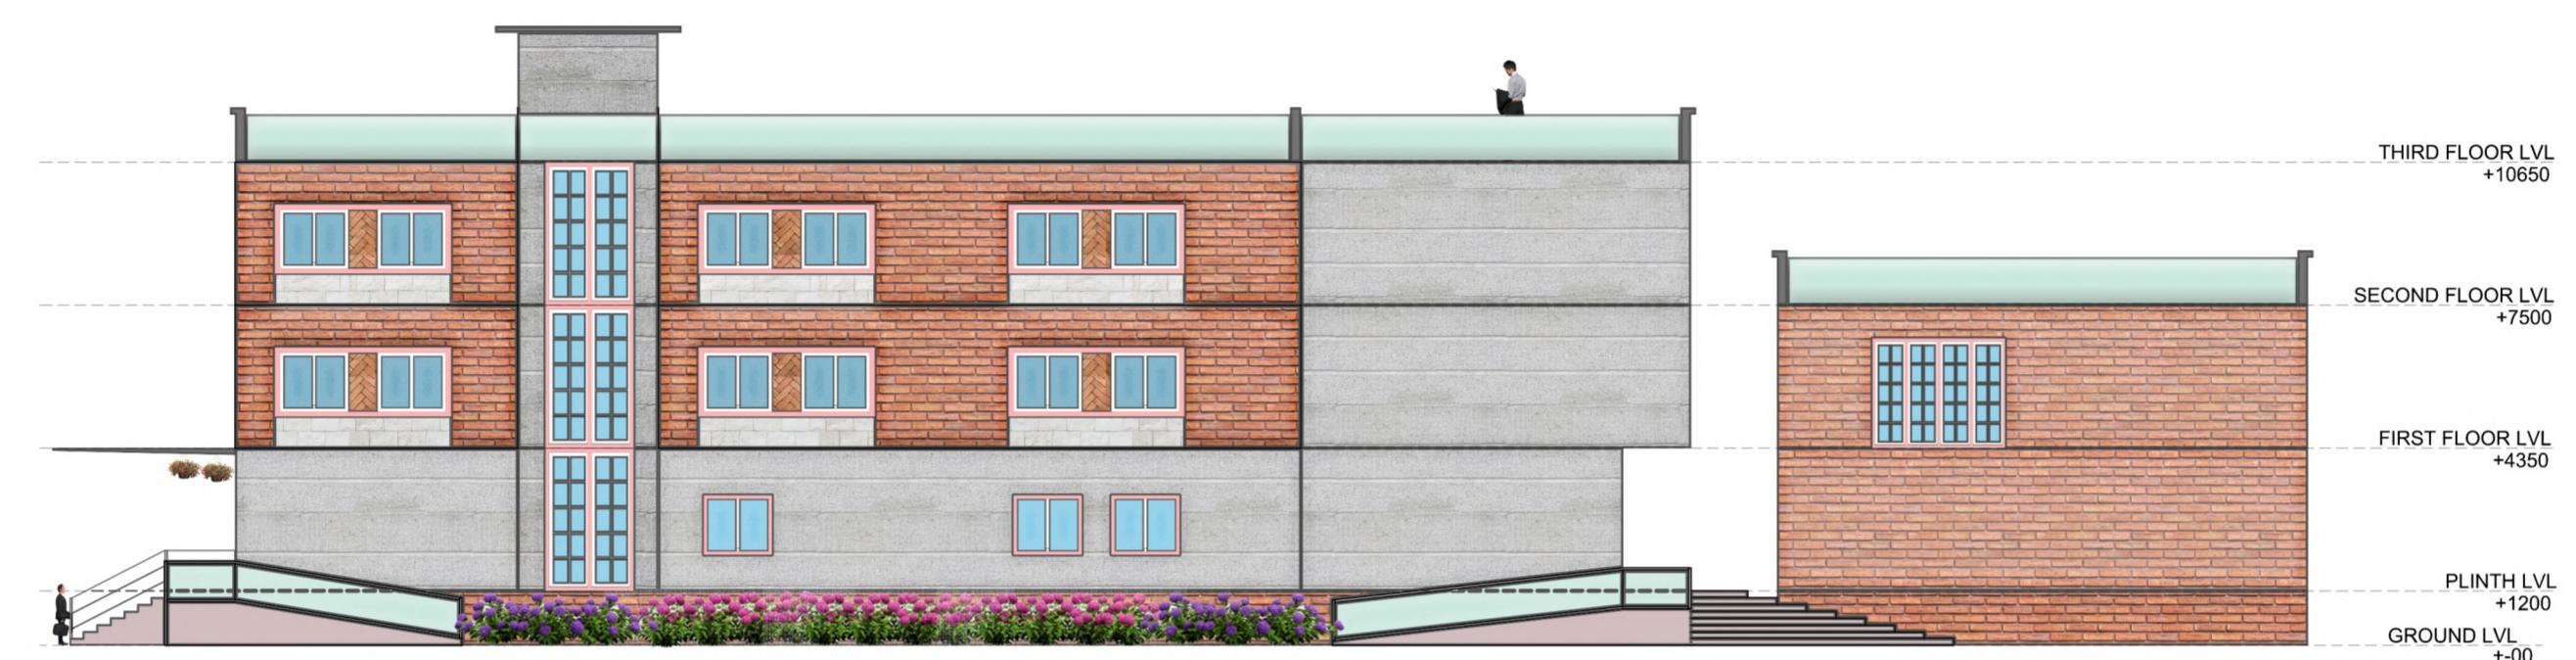


NORTH-WEST ELEVATION




SOUTH-EAST ELEVATION


GD GOENKA UNIVERSITY, SOHNA SoAP (SEM-IV)	PROPOSED PRIMARY SCHOOL DESIGN (SITE- M3M GOLF ESTATE, SECTOR- 65)	SCALE- 1:150	FACULTIES- MRS. HARMAN MR. VIKAS GOYAL	SUBMITTED BY- YASH VARDHAN GOYAL
---	---	--------------	---	----------------------------------

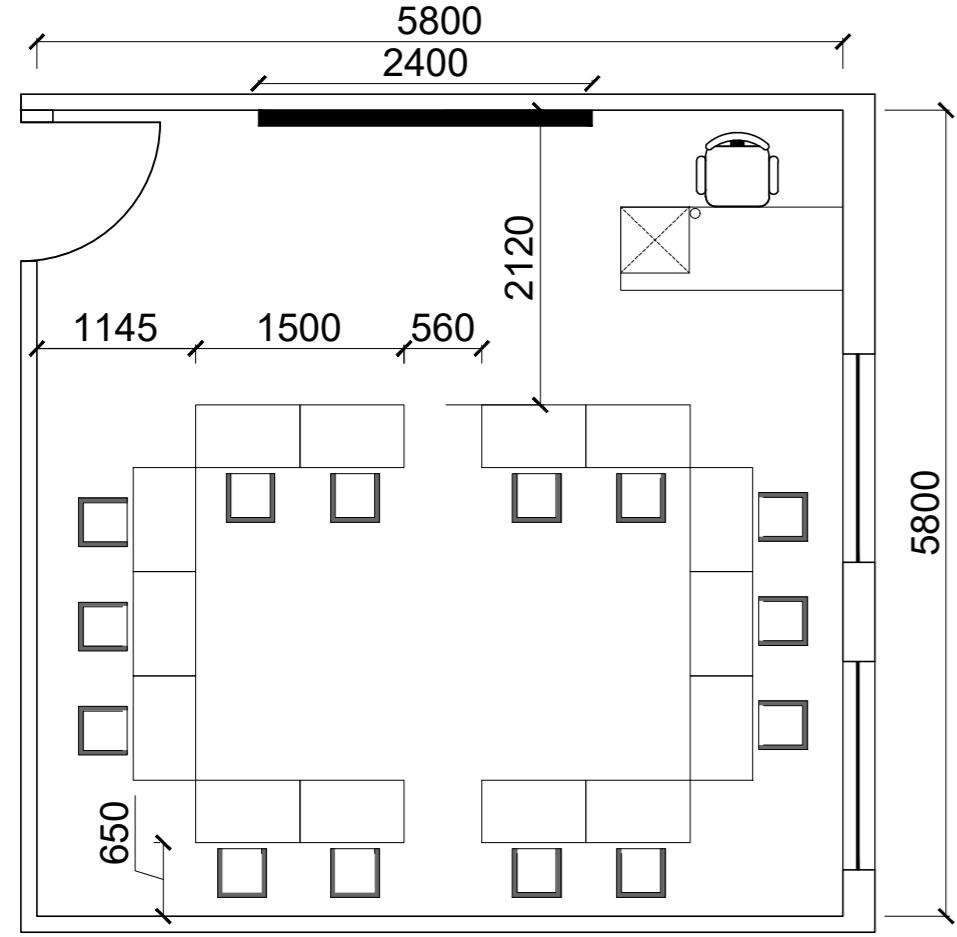


PLAY GROUP CLASSROOM

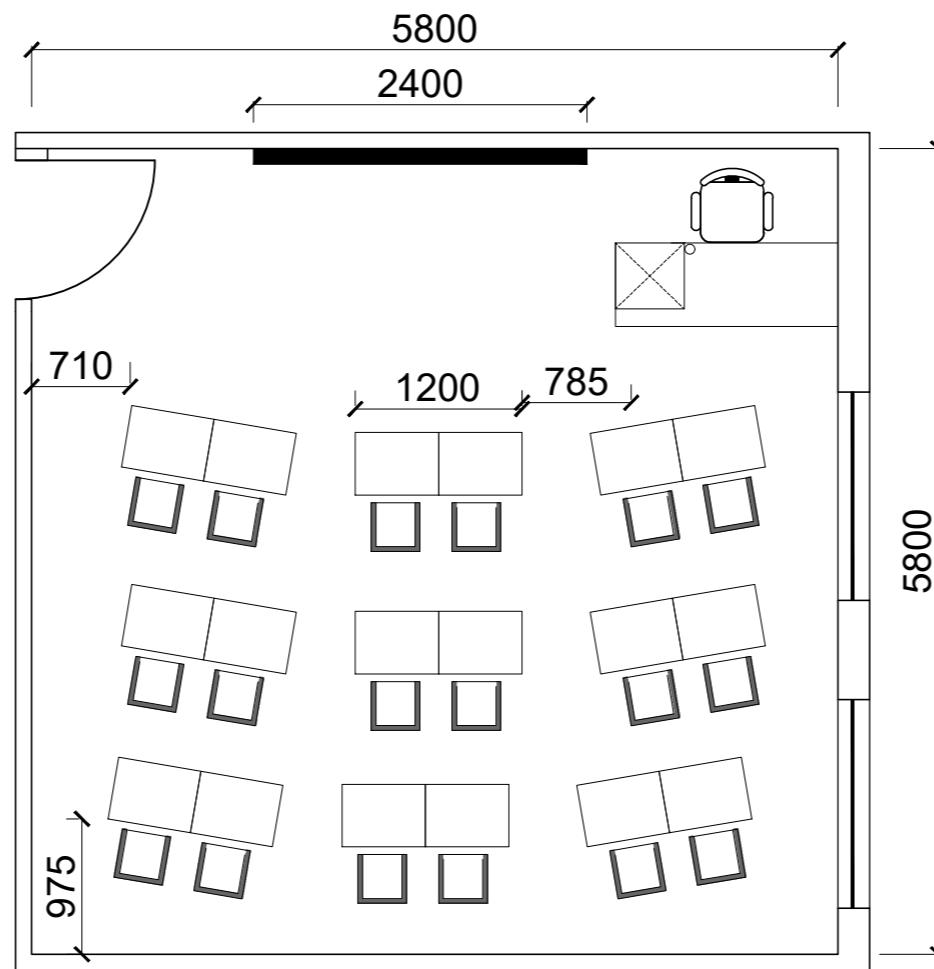


K.G. CLASSROOM

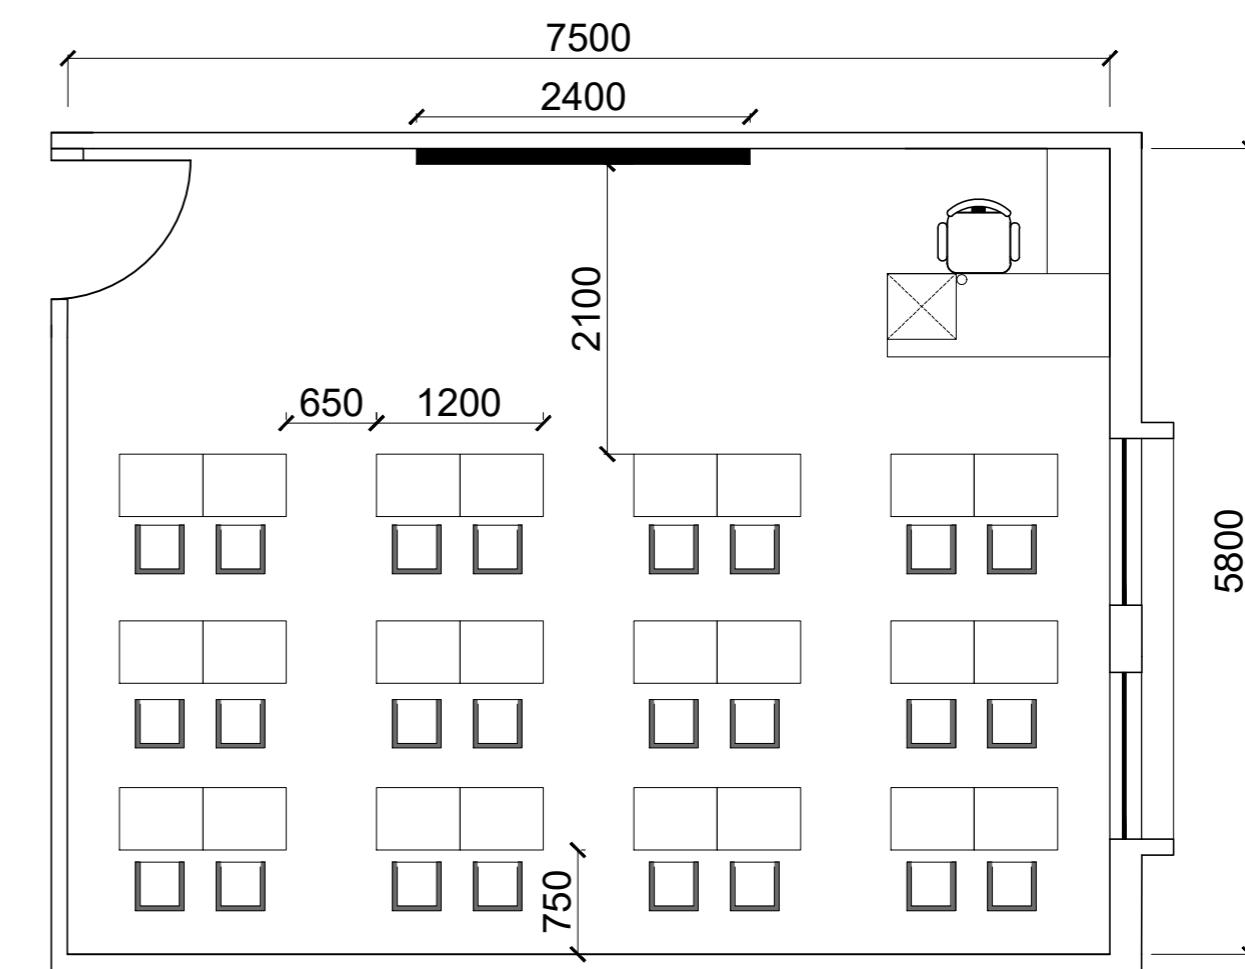


1st TO 5th CLASS CLASSROOM

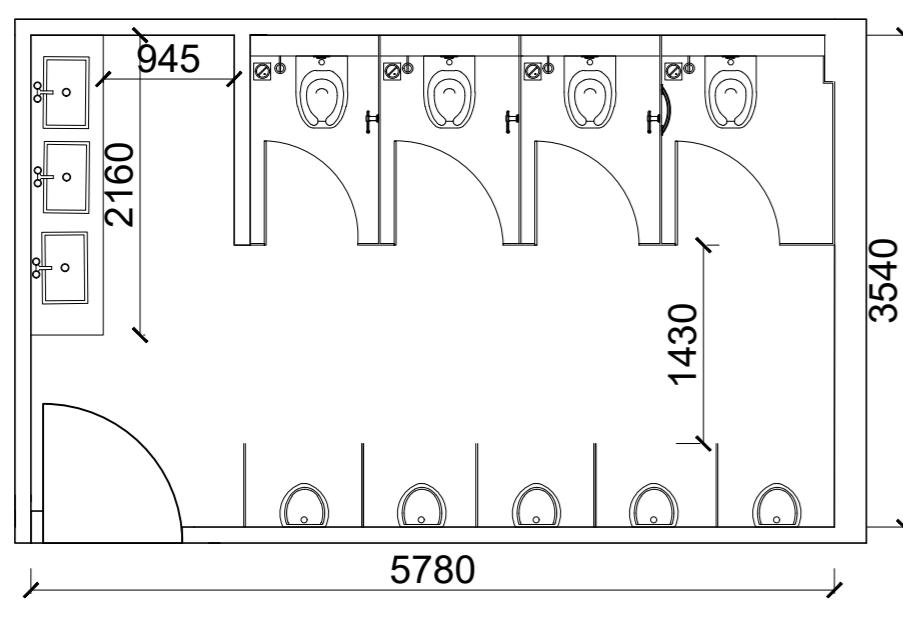


BOYS WASHROOM

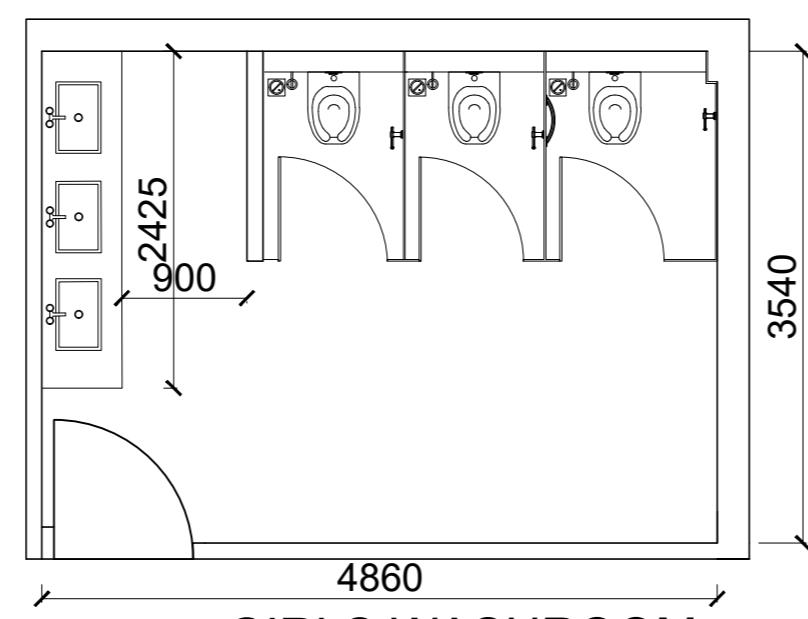



GIRLS WASHROOM

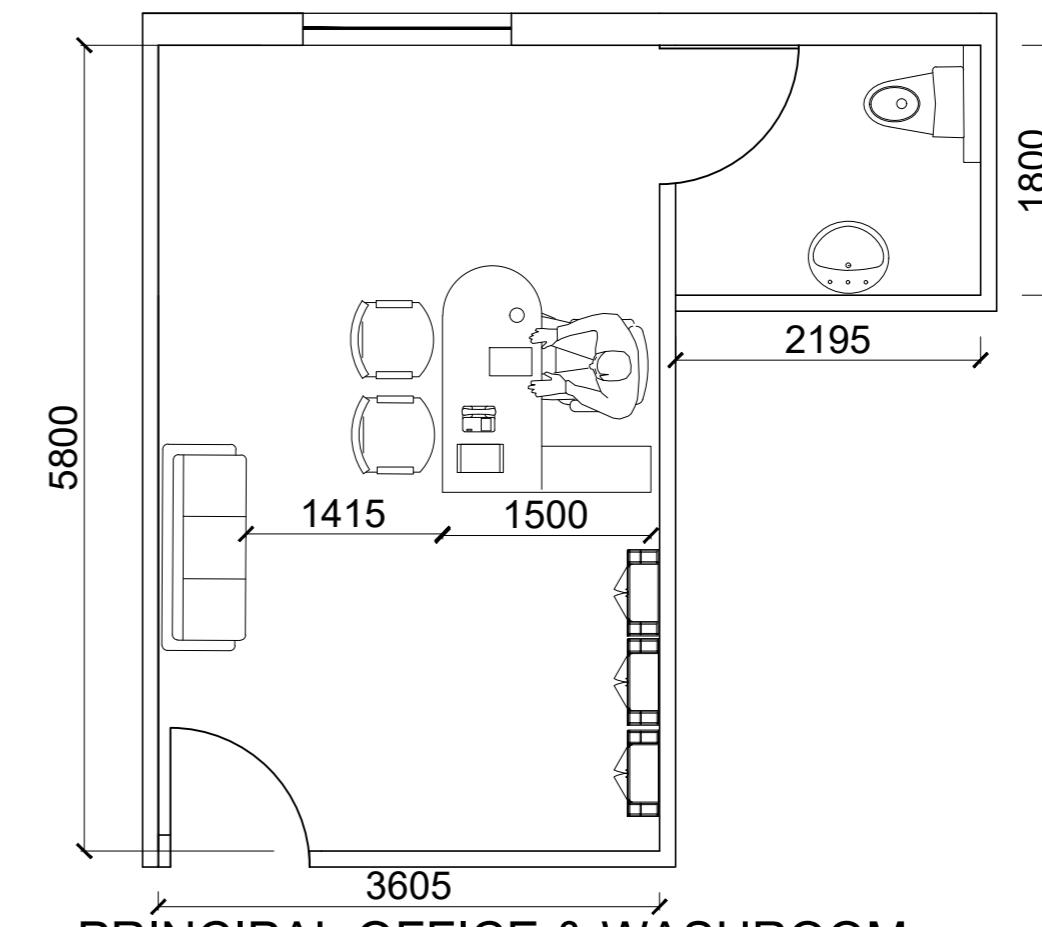

PRINCIPAL OFFICE & WASHROOM

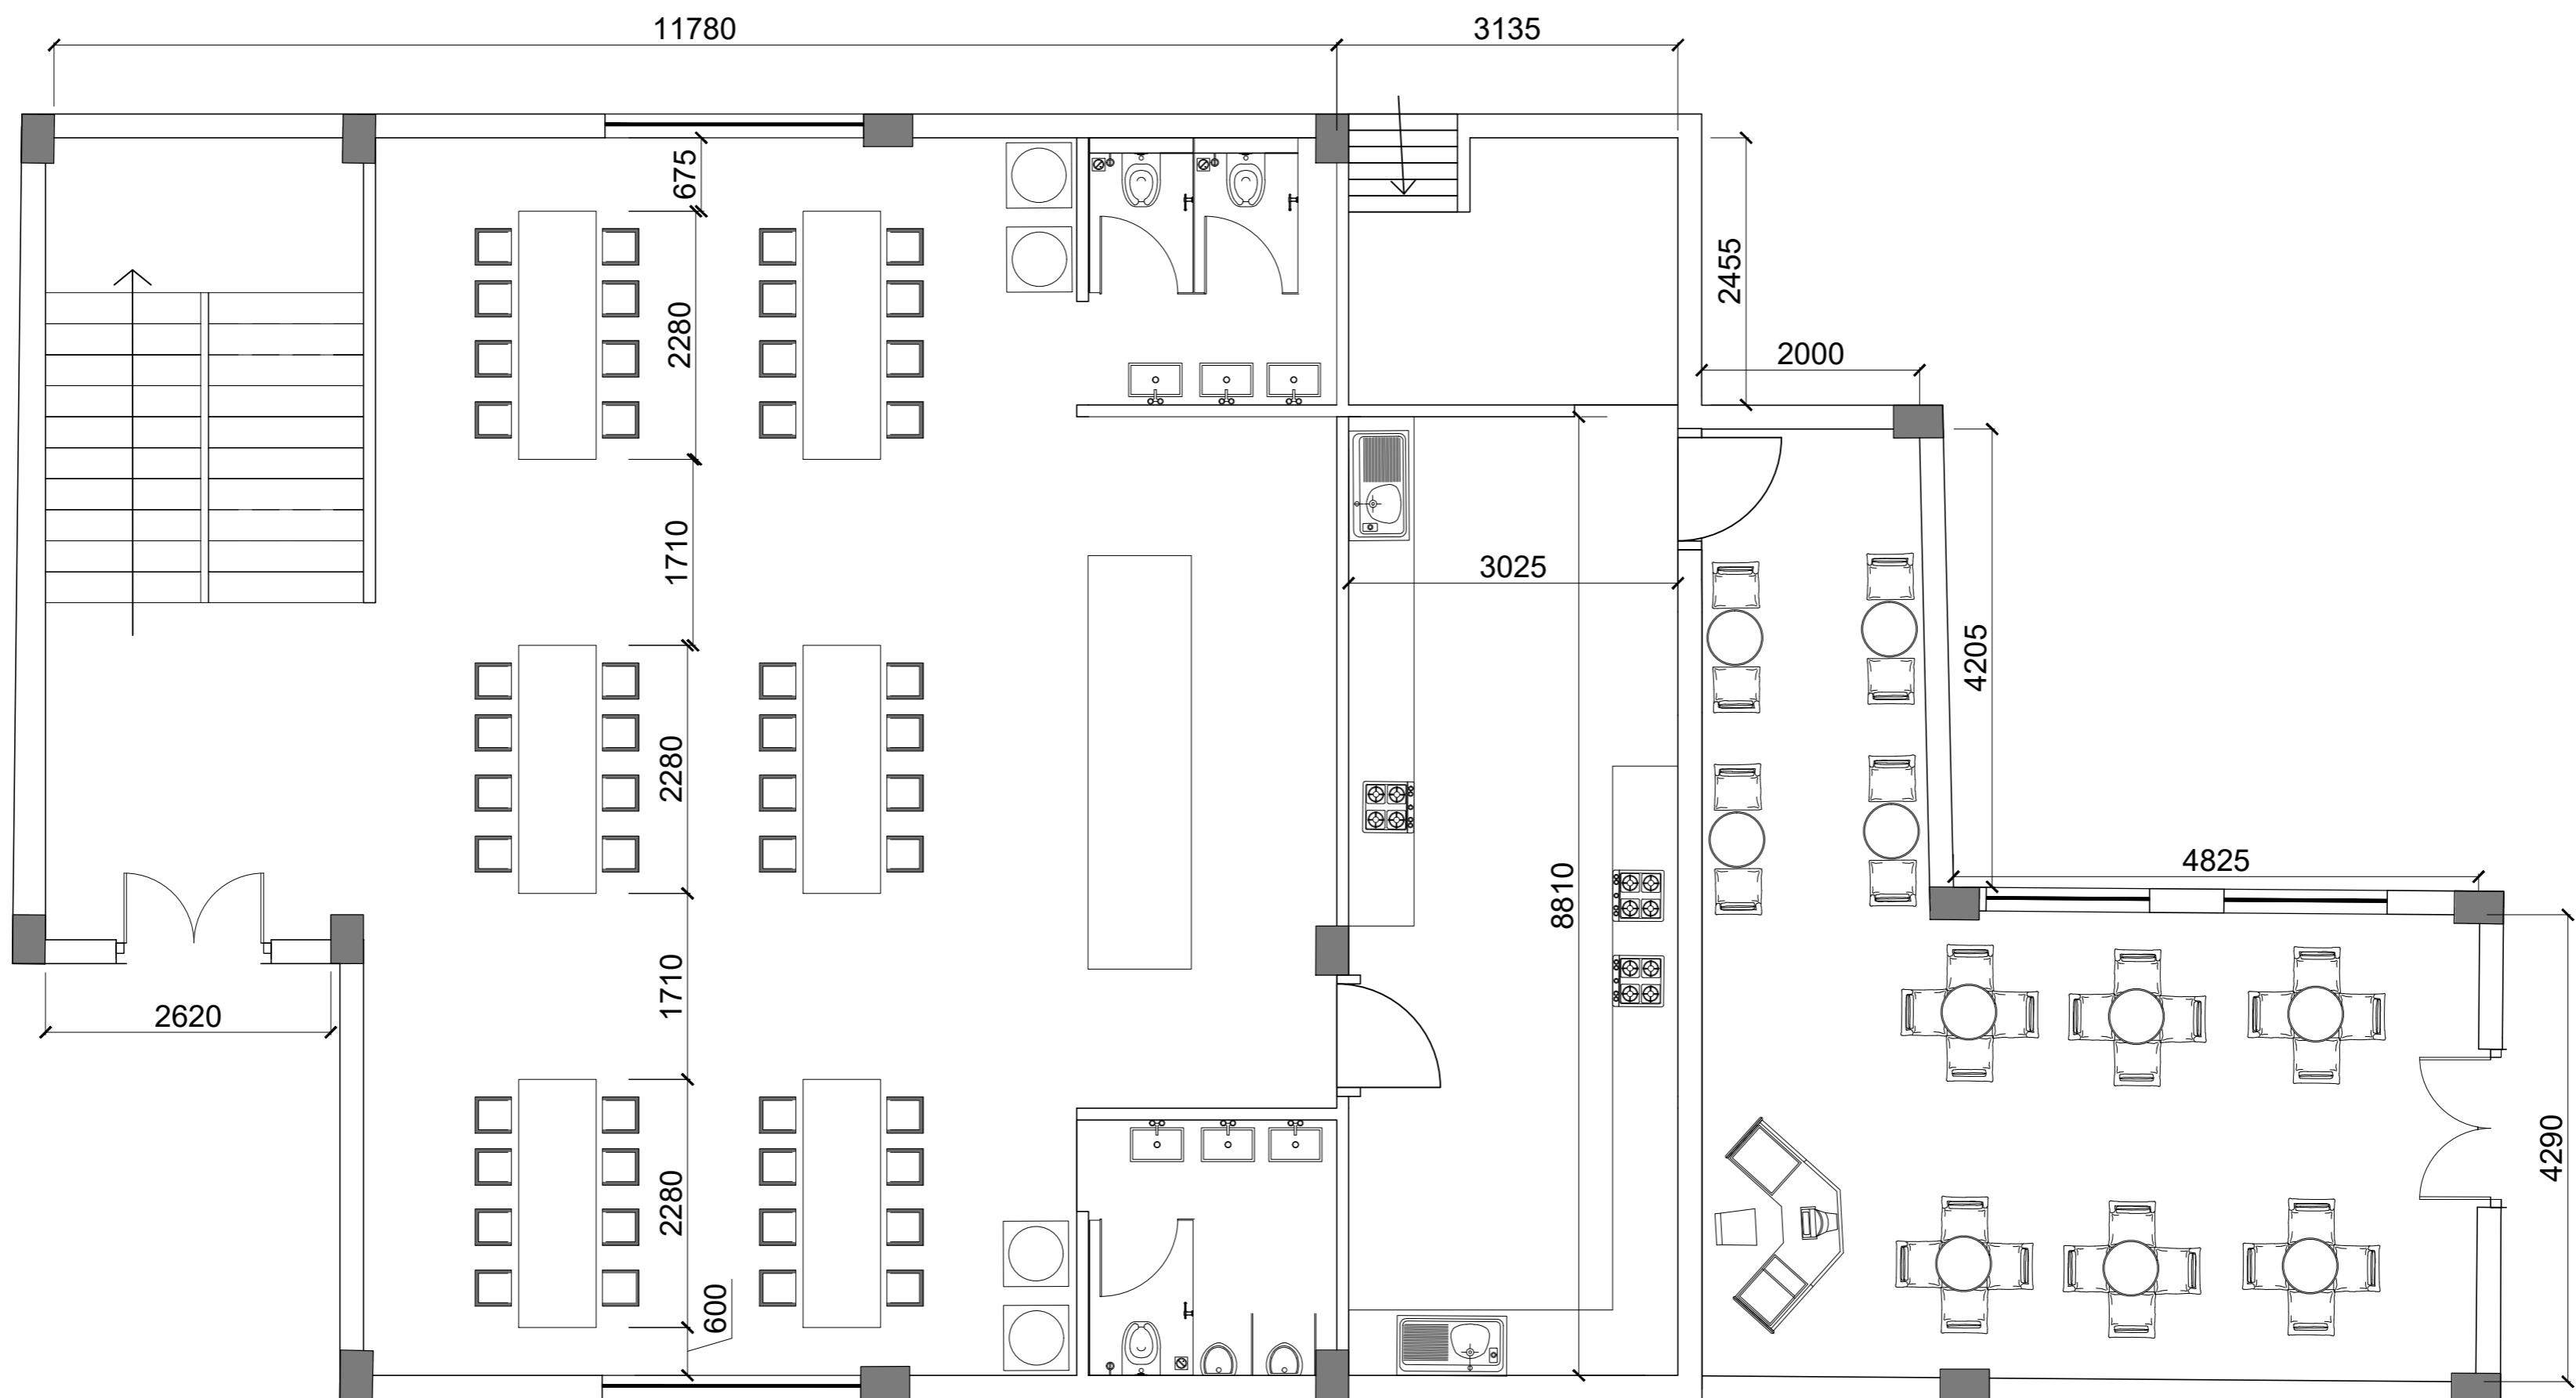


DINNING AREA + KITCHEN & CAFETERIA

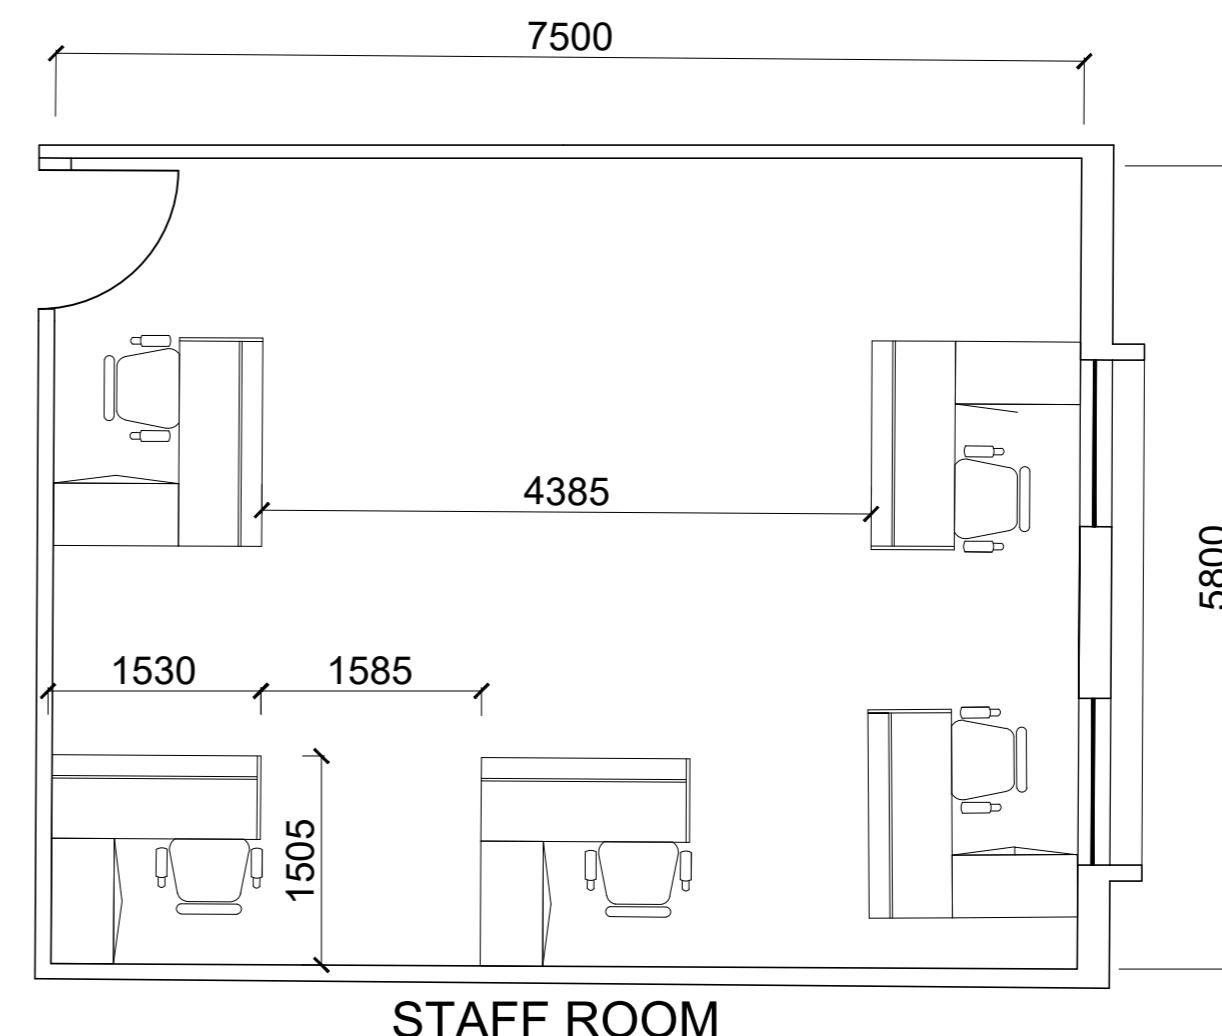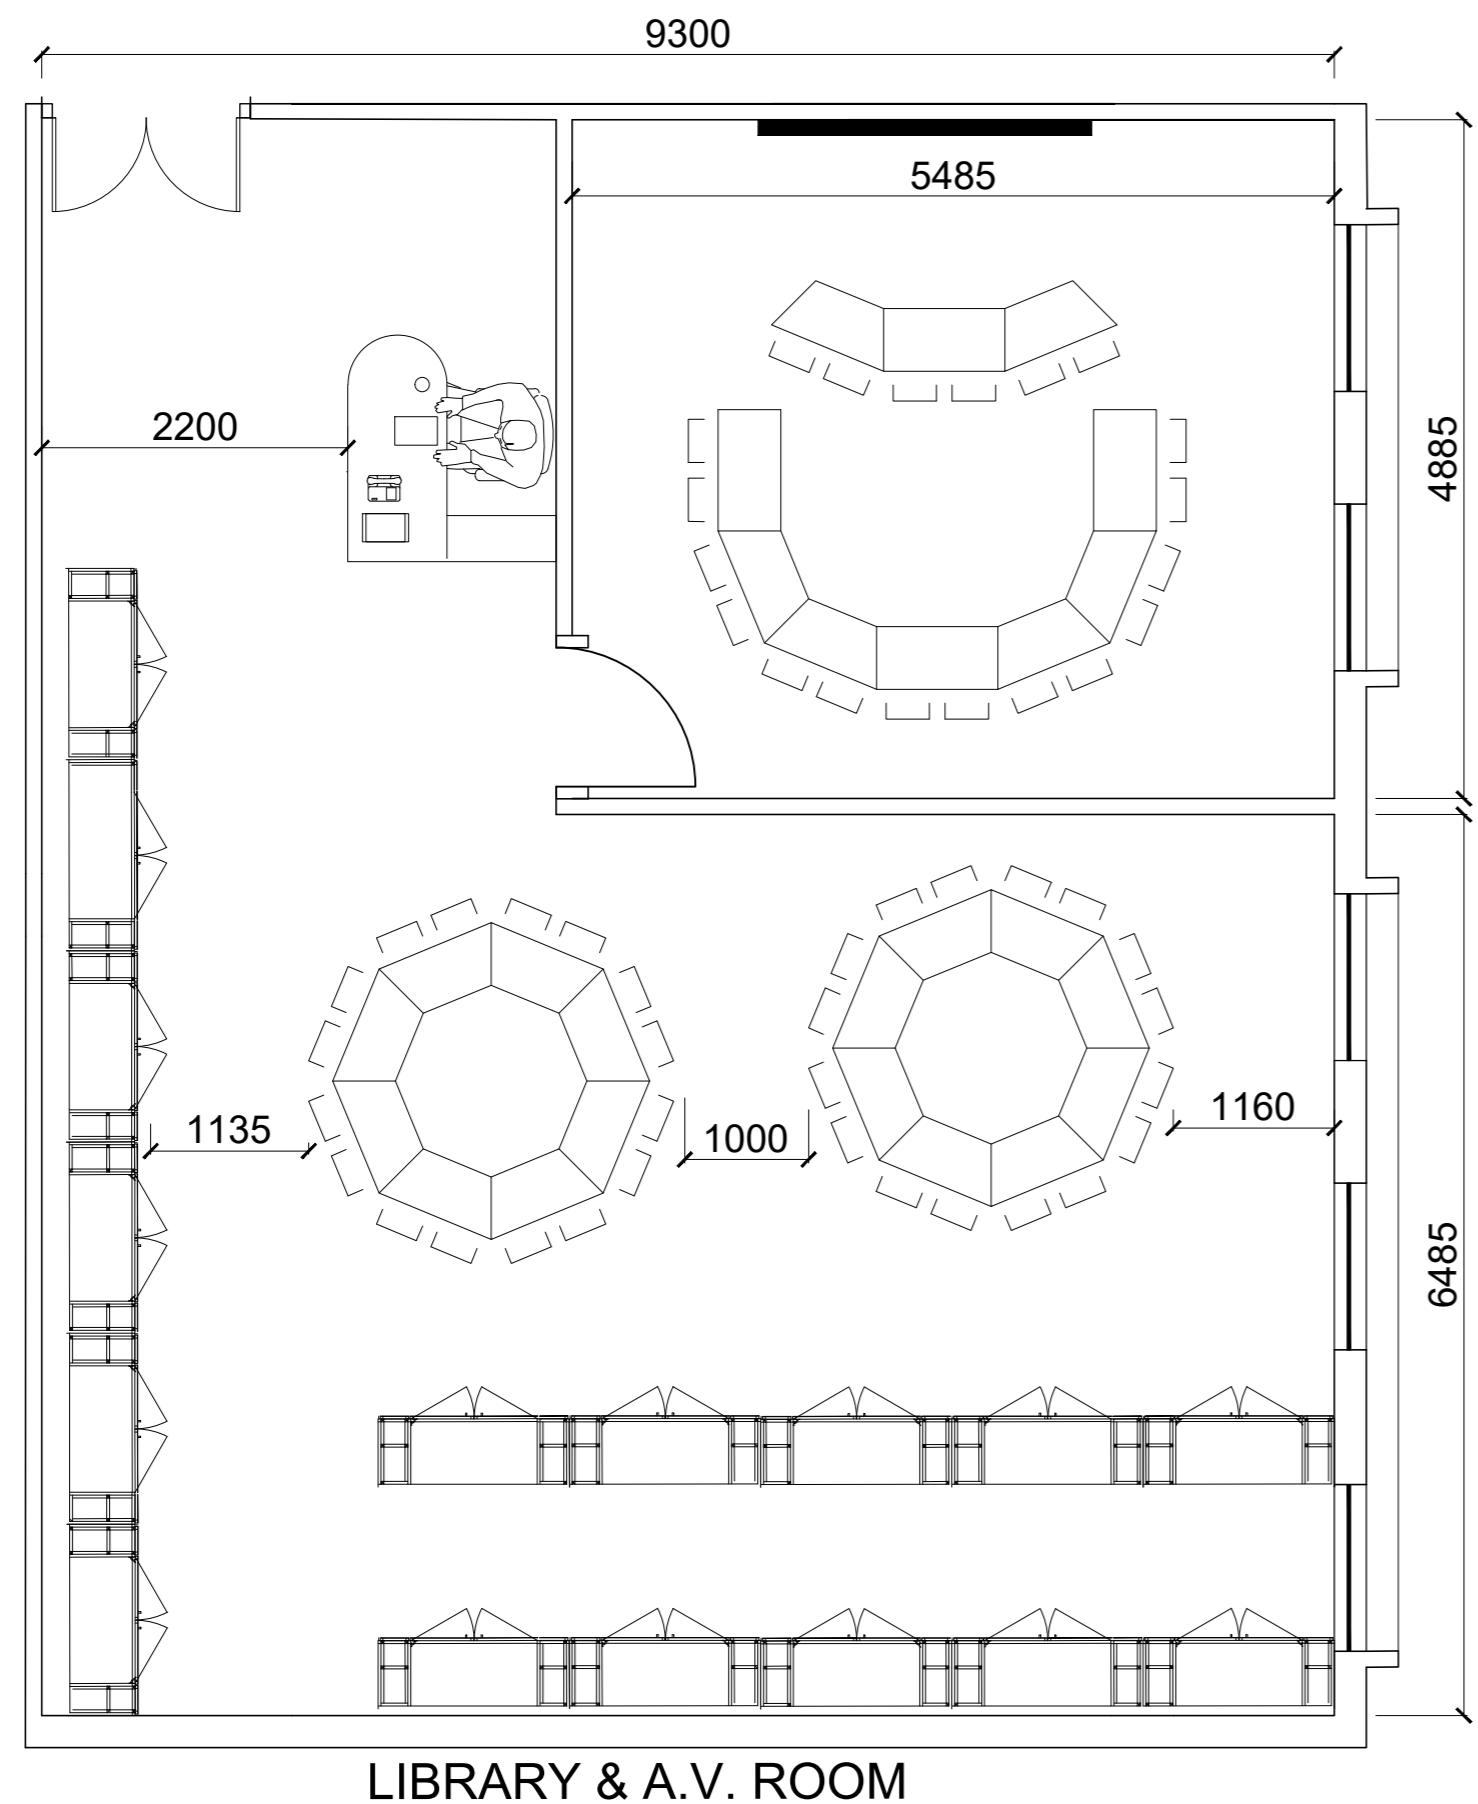



SECTION AA'

GD GOENKA UNIVERSITY, SOHNA SoAP (SEM-IV)	PROPOSED PRIMARY SCHOOL DESIGN (SITE- M3M GOLF ESTATE, SECTOR- 65)	SCALE- 1:150	FACULTIES- MRS. HARMAN MR. VIKAS GOYAL	SUBMITTED BY- YASH VARDHAN GOYAL
---	---	--------------	---	----------------------------------

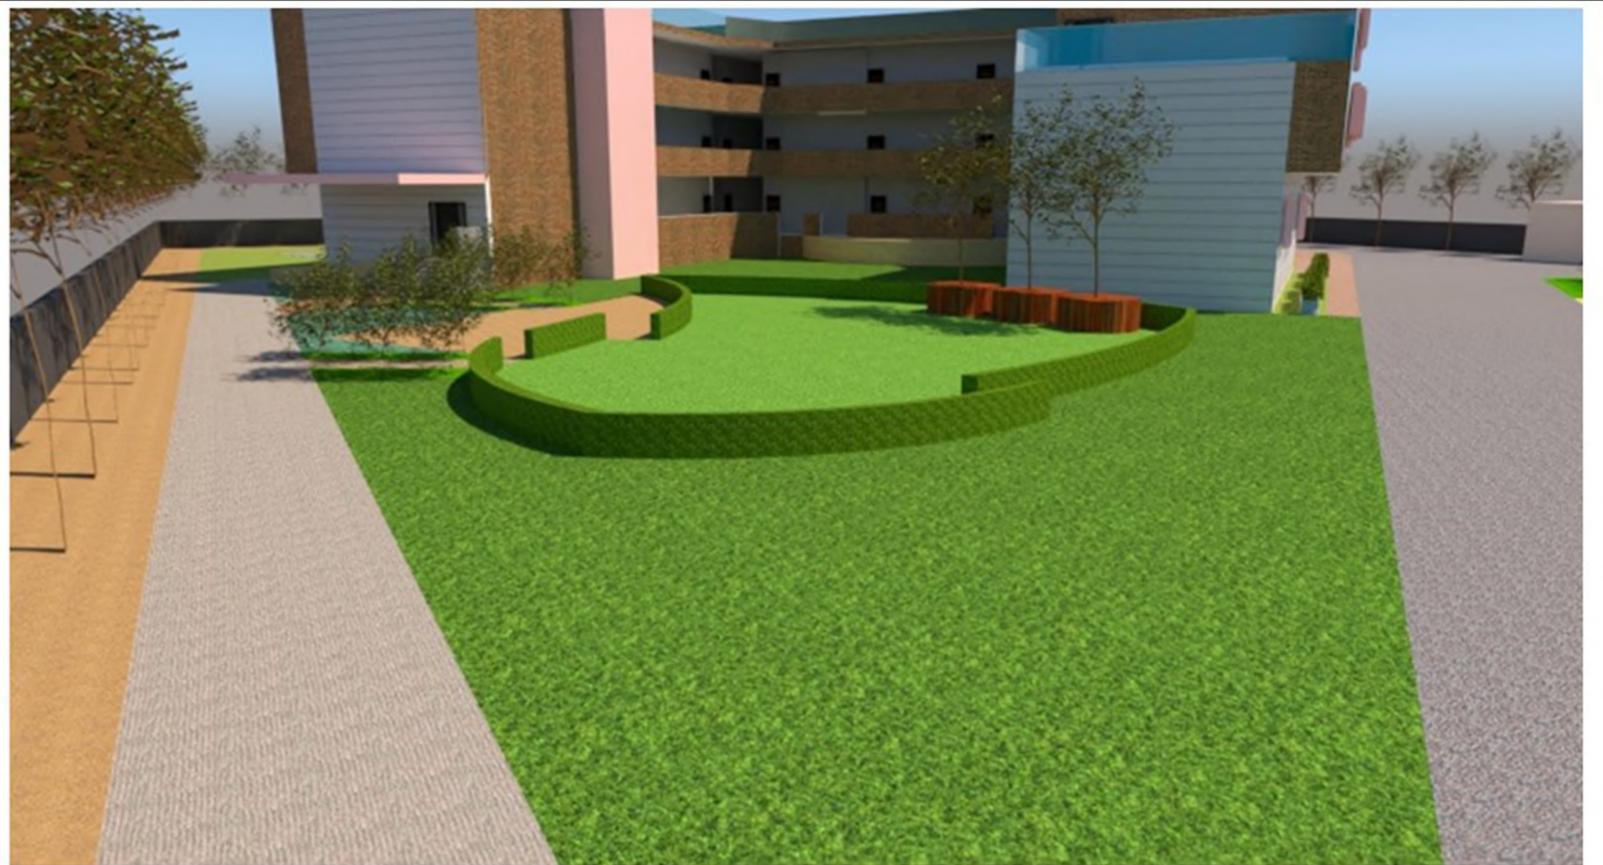

BIRD EYE VIEW




GD GOENKA  
UNIVERSITY, SOHNA  
SoAP (SEM-IV)

PROPOSED PRIMARY SCHOOL DESIGN  
(SITE- M3M GOLF ESTATE, SECTOR- 65)

SITE VIEWS

FACULTIES- MRS. HARMAN  
MR. VIKAS GOYAL

SUBMITTED BY- YASH VARDHAN GOYAL

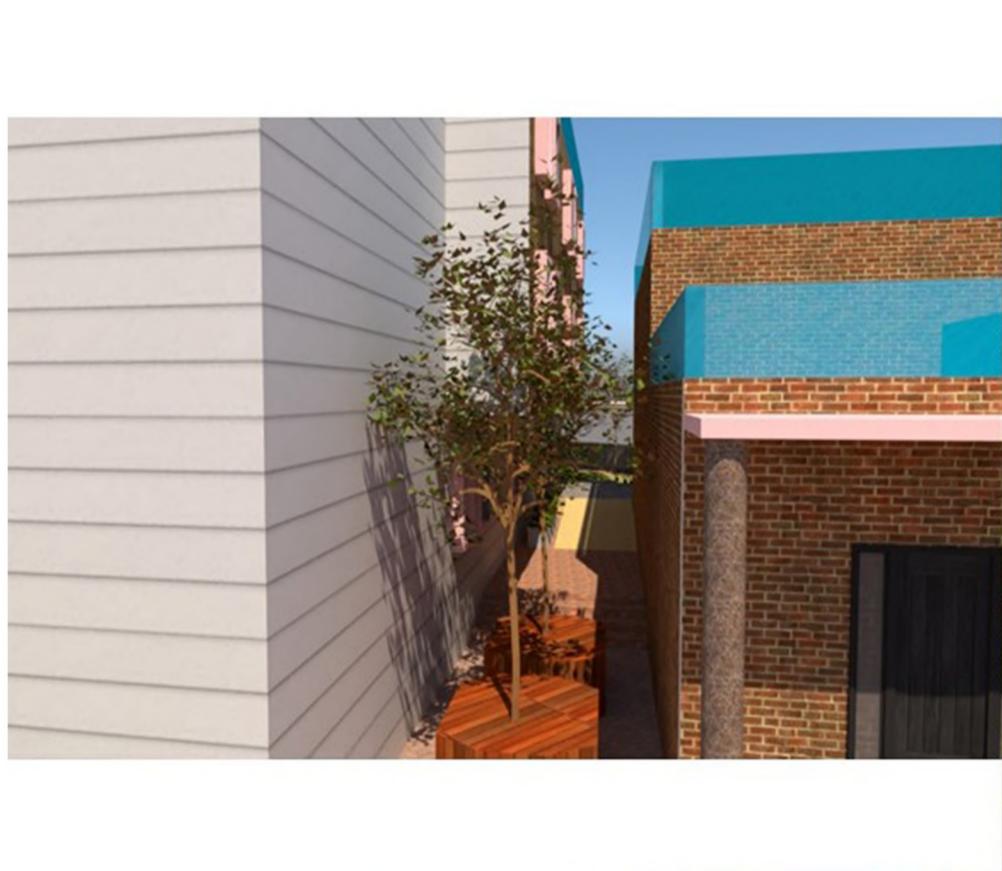

GD GOENKA  
UNIVERSITY, SOHNA  
SoAP (SEM-IV)

PROPOSED PRIMARY SCHOOL DESIGN  
(SITE- M3M GOLF ESTATE, SECTOR- 65)

SITE VIEWS

FACULTIES- MRS. HARMAN  
MR. VIKAS GOYAL

SUBMITTED BY- YASH VARDHAN GOYAL